


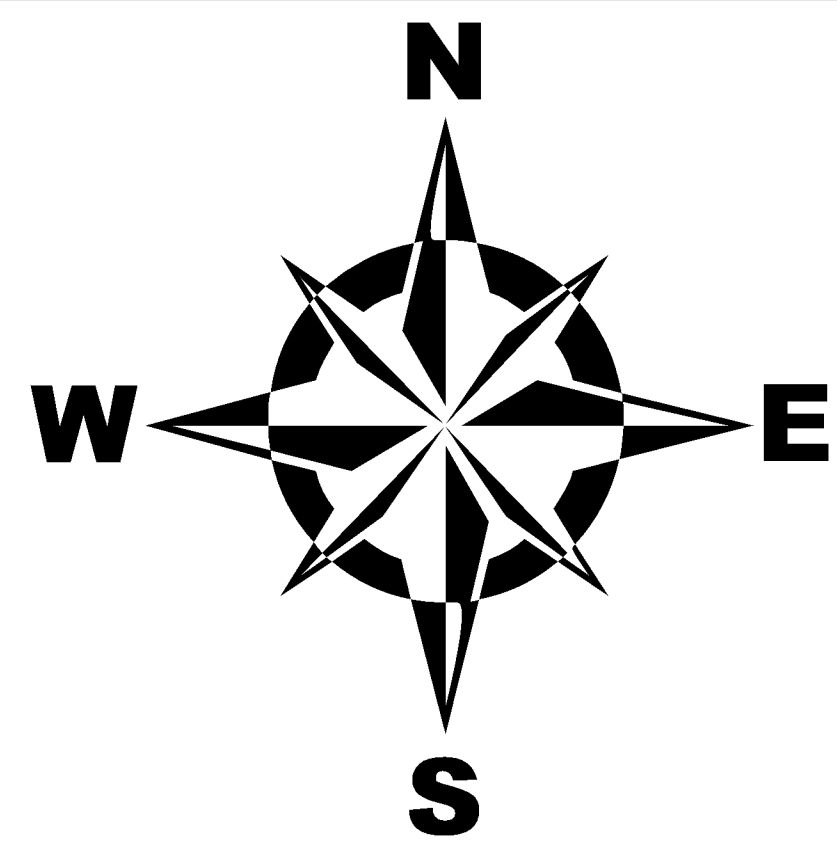

ГЕНЕРАЛЬНИЙ ПЛАН село ВОЛОДИМИРІВСЬКЕ ПЛАН ІСНУЮЧОГО ВИКОРИСТАННЯ ТЕРИТОРІЇ ЗІ СХЕМОЮ ІСНУЮЧИХ ПЛАНУВАЛЬНИХ ОБМЕЖЕНЬ Масштаб 1:5000

УМОВНІ ПОЗНАЧЕННЯ

- Межа міської, селищної, сільської ради
- Межа населеного пункту існуюча
- Житлова вулиця
- Житловий будинок існуючий капітальний
- Громадська будівля існуюча
- Виробнича будівля (споруда) існуюча
- залізниця існуюча
- Повітряна лінія електропередач 10 кВ існуюча
- Повітряна лінія електропередач 35 кВ
- Повітряна лінія електропередач 150 кВ існуюча
- Водопровід існуючий
- Газопровід існуючий
- Каналізація існуюча
- Трансформаторна підстанція існуюча
- Комплектна трансформаторна електропідстанція (КТП) існуюча
- Газорозподільний пункт (ГРП, ШРП) існуючий
- АЗС існуюча
- Місце збору води для потреб пожежегасіння (пожежний водозбір)
- Територія громадської забудови існуюча
- Територія житлової багатоквартирної забудови існуюча
- Територія житлової садибної забудови існуюча
- Територія виробнича існуюча
- Територія транспортної інфраструктури існуюча
- Територія інженерної інфраструктури існуюча
- Територія сільськогосподарського призначення існуюча
- Територія зелених насаджень загального користування існуюча
- Територія зелених насаджень спецпризначення існуюча
- Територія кладовища існуюча
- Охоронна зона інженерних мереж
- Територія об'єкту культурної та археологічної спадщини
- Прибережна-захисна смуга

ЕКСПЛІКАЦІЯ

- ЗАГАЛЬНООСВІТНІЯ ШКОЛА
- ДИТЯЧИЙ ДОШКІЛЬНИЙ ЗАКЛАД
- ЦЕРКВА
- КАФЕ ТА БІЛЬЯРДНИЙ КЛУБ
- МАГАЗИН ДЕКОРАТИВНИХ РОСЛИН
- ОБ'ЄКТИ ТОРГІВЛІ
- ПРОМИСЛОВО-ТОРГІВЕЛЬНИЙ ЦЕНТР
- РИНОК
- СПОРТИВНИЙ КОМПЛЕКС
- ТОРГІВЕЛЬНИЙ КОМПЛЕКС
- ТОРГІВЕЛЬНО-ПОКУПОВИЙ КОМПЛЕКС
- ТОРГІВЕЛЬНО-СЕРВІСНИЙ ЦЕНТР
- СЕРВІСНИЙ КОМПЛЕКС
- АВТОЗАПРАВНА СТАНЦІЯ
- АВТОСЕРВІС
- ГАРАЖНИЙ КООПЕРАТИВ
- МАЙДАНЧИК ЗБЕРІГАННЯ ТРАНСПОРТНИХ ЗАСОБІВ
- КОТЕЛЬНЯ
- ПЛАНТАЦІЯ ДЕКОРАТИВНИХ БАГАТОРІЧНИХ НАСАДЖЕНЬ
- СІЛЬСЬКОГОСПОДАРСЬКЕ ПІДПРИЄМСТВО БЕЗ СЗЗ
- СКЛАД ЗЕРНА
- СТОЯНКА СІЛЬСЬКОГОСПОДАРСЬКОЇ ТЕХНІКИ
- ТЕРИТОРІЯ ІНДИВІДУАЛЬНОГО САДІВНИЦТВА
- ЦЕХ ДЛЯ ВИРОБНИЧО-СІЛЬСЬКОГОСПОДАРСЬКИХ ПОТРЕБ
- ЦЕХ РОЗЛИВУ ОЛІЇ
- ВИРОБНИЦТВО ПО ОБ'ЄКТАМ ХАРЧОВИХ ПРОДУКТІВ ТА СМАКОВИХ РЕЧОВИН
- ВИРОБНИЧА БАЗА
- ВИРОБНИЧО-РЕМОНТНИЙ КОМПЛЕКС
- ПРОМИСЛОВА БАЗА
- СКЛАД ЛІСОМАТЕРІАЛІВ
- КЛАДОВИЩЕ

Система координат: Україна 2000 GK Zone 4
Проекція: Gauss-Kruger
Датум: Україна 2000
False Easting: 6 500 000,0000
False Northing: 0,0000
Central Meridian: 23,0000
Scale Factor: 1,0000
Latitude Of Origin: 0,0000
Единиця вимірювання: Метри



ФОП Прудка

ОБ'ЄКТ: ВОЛОДИМИРІВСЬКЕ ГЕНЕРАЛЬНИЙ ПЛАН СЕЛА ВОЛОДИМИРІВСЬКЕ ЗАПОРІЗЬКОГО РАЙОНУ ЗАПОРІЗЬКОЇ ОБЛАСТІ		ЛОГОВІР:
КРЕСЛЕНИЙ: ПЛАН ІСНУЮЧОГО ВИКОРИСТАННЯ ТЕРИТОРІЇ ЗІ СХЕМОЮ ІСНУЮЧИХ ПЛАНУВАЛЬНИХ ОБМЕЖЕНЬ		МАСШТАБ: 1:5000
ГОЛ. АРХИТЕКТОР ПРОЕКТУ	ПРУДКА	ДАТА: 2024р.
РОЗРОБИВ	ПРУДКА	

1 cm = 50 метрів

0 500 1 000 2 000 3 000 4 000 Метри