

ФО – П Прудка І. А.

Замовник:

Широківська сільська рада Запорізького району
Запорізької області

Генеральний план села Володимирівське Запорізького району
Запорізької області. Оновлення з розширенням меж населеного
пункту та план зонування села Володимирівське Запорізького району
Запорізької області (у складі генерального плану)

Основні положення генерального плану

Шифр: 1/23-ПЗ

ТОМ 2

Фізична особа підприємець _____ І. А. Прудка

Головний архітектор проекту _____ І. А. Прудка

2023 р.

Погоджено		

Зам. Інв. №

Підпис і дата

Інв. № об.

Погоджено				
Інв. № об.	Підпис і дата	Зам. Інв. №		

2																				
Позначення						Найменування				Примітка										
1/23-ПЗ						Зміст														
1/23-СП						Склад проекту														
1/23-ПД						Підтвердження ГАП														
1/23-ВУ						Відомості про учасників проектування														
1/23-ПЗ						Пояснювальна записка														
						Вступ														
						1.Характеристика структури та обсягів існуючого житлового фонду, об'єктів обслуговування, перелік об'єктів господарського комплексу, інженерно-транспортної інфраструктури, інженерної підготовки та благоустрою, захисту території від небезпечних природних і техногенних процесів.														
						2. Основні пріоритети та цільові показники соціального і демографічного розвитку території з метою формування повноцінного життєвого середовища														
						3. Характеристика території, необхідних для подальшого розвитку населеного пункту, а також території спільних інтересів суміжних територіальних громад.														
						4. Пропозиції щодо зміни меж населеного пункту.														
						5. Опис перспективної планувальної структури та функціонального зонування.														
						6. Характеристику територій та визначення заходів щодо їх освоєння.														
						7. Пропозиції щодо формування системи громадських центрів.														
						8. Обсяги житлового будівництва.														
						9. Напрями розвитку вулично – дорожньої мережі, транспорту, інженерної інфраструктури.														
						10. Заходи з інженерної підготовки та захисту територій від небезпечних														
						1/23-3														
Зм.						Кільк.				Арк.	№ док	Підпис	Дата	Зміст			Стадія	Аркуш	Аркушів	
Розробив						Прудка							12.23				ГП	1	1	
Перевірів																				
ГАП						Прудка							12.23				ФО-П Прудка І. А.			

--	--	

										4		
№ тому		Позначення			Найменування					Примітки		
					Текстові матеріали							
1.		1/21-ПЗ			Пояснювальна записка до генерального плану							
2.		1/21-ПЗ			Основні положення генерального плану							
3.		1/21-ПЗ			Пояснювальна записка до плану зонування території							
4.		1/21-ГП			Графічні матеріали							
		Аркуш 1			Схема розташування населеного пункту в системі розселення							
		Аркуш 2			План існуючого використання території. Схема існуючих планувальних обмежень М 1:2000							
		Аркуш 3			Генеральний план (основне креслення). Схема проектних планувальних обмежень М 1:2000.							
		Аркуш 4			Схема вулично – дорожньої мережі, міського (сільського) та зовнішнього транспорту М 1:2000							
		Аркуш 5			Схема інженерного обладнання території М 1:2000							
		Аркуш 6			Схема інженерної підготовки та захисту території М 1:2000							
		Аркуш 7			План зонування території М 1:2000							
					Інженерно-технічні заходи цивільного захисту (цивільної оборони)					У вигляді окремих томів		
						1/23-СП						
Зм.		Кільк.	Арк.	№ док	Підпис	Дата	Склад проекту			Стадія	Аркуш	Аркушів
Розробив			Прудка			12.23				ГП	1	1
Перевірив												
ГАП			Прудка			12.23						
										ФО-П Прудка І. А.		

Погоджено

Зам. Інв. №

Підпис і дата

Інв. № об.

Генеральний план села Володимирівське Запорізького району Запорізької області. Оновлення з розширенням меж населеного пункту та план зонування села Володимирівське Запорізького району Запорізької області (у складі генерального плану) виконано згідно з вимогами ДБН Б.1.1-15:2012 "Склад та зміст генерального плану населеного пункту", ДБН Б.1.1-22:2017 «Склад та зміст плану зонування території», ДБН Б. 2.2-12:2019 «Планування і забудова територій», екологічних, санітарно-гігієнічних та протипожежних норм, що діють на території України, а також Закону України «Про містобудівну діяльність».

Головний архітектор проекту

І. А. Прудка

Кваліфікаційний сертифікат відповідального виконавця окремих видів робіт (послуг), пов'язаних із створенням об'єкта архітектури (розроблення містобудівної документації) Серія АА №003280.

[illegible]

This image shows a completely blank white rectangular area enclosed within a thin black frame. There are no markings, text, or illustrations present on the page.

						1/23-ВУ			
Зм.	Кільк.	Арк.	№ док	Підпис	Дата	Відомості про учасників проектування	Стадія	Аркуш	Аркушів
Розробив		Прудка			12.23		ГП	1	1
Перевірив									
ГАП		Прудка			12.23				
							ФО-П Прудка І. А.		

Погоджено			

Інв. № об.	Підпис і дата	Зам. Інв. №
------------	---------------	-------------

--

ВСТУП

Замовником Генерального плану та плану зонування території с. Володимирівське є Широківська сільська рада Запорізького району Запорізької області.

69089, Запорізька область, м. Запоріжжя, вул. Розенталь, 7.

Виконавцем Генерального плану та плану зонування села Володимирівське

Запорізького району Запорізької області є:

Фізична особа підприємець Прудка І. А.

69039, м. Запоріжжя, пров. Великий (в минулому Вантажний), 13
ІНН 2803210762

Головний архітектор проекту – І. А. Прудка,

Кваліфікаційний сертифікат відповідального виконавця окремих видів робіт (послуг), пов'язаних із створенням об'єкта архітектури Серія АА № 003280 (розроблення містобудівної документації)

Свідоцтво про проходження підвищення кваліфікації за видом робіт «Розроблення містобудівної документації» № 4049 від 22 липня 2021 року.

Геодезична зйомка території надана Замовником у складі вихідних даних та надана розробнику в 2021 р., для виконання генерального плану, довідка про проведення топографо-геодезичних робіт (див. Додатки)

Тахеометрична зйомка виконувалась тахеометром та виконана у державній геодезичній системі координат ЧСК-2000. На креслені схема сучасного використання території наведена інформація щодо об'єктів державного земельного кадастру, таких як межі населених пунктів, існуючі відводи земельних ділянок, водні об'єкти, магістральні інженерні мережі, об'єкти енергетики, культурної спадщини інші об'єкти. Згідно ДБН 5.1.1-15:2012 «Склад та зміст генерального плану населеного пункту» інформація щодо власників земельних ділянок або їх землекористувачів та інформація про пункти Державної геодезичної мережі не вимагається в складі містобудівної документації.

Інформація що до структури та характеристики земель взята з публічного джерела публічної кадастрової карти України та сайту <https://ngo.land.gov.ua/uk/map/>.

Територія села межує з ділянками представленими ґрунтами шифр 54 чорнозему звичайні малозумусні які не є особливо цінними відповідно до наказу N 245 Державного комітету України по земельним ресурсам від 06.10.2003.

Підставою для розробки генерального плану та зонінгу села ВВолодимирівське є Рішення Широківської сільської ради, Запорізького району Запорізької області № 6 від 07.11.2018 року

Погоджено			
Зам. Інв. №			
Підпис і дата			
Інв. № об.			

Зм.	Кіл.	Арк.	№ док.	Підпис	Дата	12.23	1/23-ПЗ	Аркуш
-----	------	------	--------	--------	------	-------	---------	-------

Генеральний план населеного пункту виконаний відповідно до:
Схеми планування території Запорізької області, яка затверджена
Рішенням Обласної ради від 29.12.2011 №4.

- Земельний кодекс України
- Водний кодекс України
- Кодекс України про надра
- Закон України «Про основи містобудування»
- Закон України «Про архітектурну діяльність»
- Закон України «Про охорону культурної спадщини»
- Закон України «Про охорону археологічної спадщини»
- Закон України «Про регулювання містобудівної діяльності»
- Закон України «Про благоустрій населених пунктів»
- Закон України «Про автомобільні дороги»;

- ДБН Б 1.1-5-2007 «Система містобудівної документації (СМБД). Перша частина. Склад, зміст, порядок розроблення, погодження та затвердження розділу інженерно-технічних заходів цивільного захисту (цивільної охорони) на особливий період у містобудівній документації»

- ДБН Б.1.1-15:2012 «Склад та зміст генерального плану населеного пункту»

- ДБН Б.1.1-22:2017 «Склад та зміст плану зонування території (зонінг)»

- ДБН Б.2.2-5:2011 «Планування та забудова міст, селищ і функціональних територій. Благоустрій територій»

- ДБН Б.2.2-12:2019 «Планування і забудова територій»

- ДБН В.2.3-5:2018 «Вулиці та дороги населених пунктів»

1. Характеристика структури та обсягів існуючого житлового фонду, об'єктів обслуговування, перелік об'єктів господарського комплексу, інженерно-транспортної інфраструктури, інженерної підготовки та благоустрою, захисту території від небезпечних природних і техногенних процесів.

Територія населеного пункту складається з території об'єктів громадської забудови, житлової забудови, комунальних та промислових об'єктів, об'єктів інженерної та транспортної інфраструктури.

Житлова забудова села в існуючих межах складається з садибної та багатоквартирної забудови. В селі налічується 1614 домогосподарств, 8 багатоквартирних будинків.

Населення села складається з
654 осіб в віці від 0 до 19 років з них 130 дітей дошкільного віку
728 осіб в віці від 20 до 35 років
858 осіб в віці від 36 до 55 років
925 осіб в віці старше 55 років
Всього 3165 осіб.

Орієнтовний склад населення на теперішній час в нових межах населеного пункту становить - 7350 осіб з них 3000 осіб ВПО та 1200 осіб мешканці дачних та садибних кооперативів.

Основні об'єкти соціальної інфраструктури, які діють на території населеного пункту

Громадський центр села практично сформовано в існуючих межах.

Об'єкти культурно-побутового обслуговування знаходяться на різних ділянках, переважно в центральній частині населеного пункту.

На території села функціонує:

Володимирівський заклад загальної середньої освіти «Успіх» Широківської сільської ради Запорізького району Запорізької області, потужність 320 місць, фактична завантаженість 182 учня та 79 дітей дошкільного віку

- Адміністративний будинок сільської ради
- Бібліотека
- 4 крамниці змішаної торгівлі торгівельною площею 177,6 м2
- 4 продовольчі крамниці торгівельною площею 215,7 м2
- Кафе 2 одиниці
- Пошта, відділення зв'язку
- Амбулаторія
- Аптека
- Стадіон
- Храм Пресвятої Богородиці

Погоджено			
Зам. Інв. №			
Підпис і дата			
Інв. № об.			

Найблище пожежне депо функціонує в с. Широке за 25 км та проектне в с. Відрадне близько 10 км.

Транспортна інфраструктура

Транспорт є важливою галуззю економіки населеного пункту, ефективне функціонування якої є необхідною умовою стабілізації структурних перетворень економіки розвитку зовнішньоекономічної діяльності задоволення потреб населення та суспільного виробництва у перевезеннях.

З метою відведення транзитних потоків з вуличної мережі міста Запоріжжя проектом «Внесення змін до генерального плану м. Запоріжжя (коригування)» передбачається будівництво об'їзних доріг.

Зокрема проектом передбачається будівництво північної об'їзної дороги міста. Дана дорога проходитиме по проектному північному мостовому переходу та по магістральним вулицям безперервного руху. Будівництво об'їзної дороги дозволить вивести транспортні потоки, що рухаються з Кропивницького та Дніпра через Запоріжжя на Донецьк. Загальна протяжність ділянок об'їзної дороги, що проходить поза межами міста, становить 29,2 км, а загальна протяжність становить 43,7 км. Ширина магістральних вулиць в межах червоних ліній, на яких передбачається безперервний рух, становитиме 60-85 метрів.

В результаті будівництва об'їзної дороги перепробіг транспорту скоротиться на 7,2 км, час, необхідний на проїзд міста, скоротиться більш ніж в 2 рази. Проїзду частину північної об'їзної дороги пропонується звести за параметрами 1-б технічної категорії. Ці рішення враховані в Генеральному плані с. Володимирівське.

Генеральним планом частково враховані пропозиції по трасуванню проектних вулиць міста Запоріжжя, в Дніпровському районі міста під номерами Проектна 44 (ширина в червоних лініях 40 м), проектна 23 (ширина в червоних лініях 35 м),

Населений пункт с. Володимирівське забезпечений постійним транспортним сполученням з м. Запоріжжя та існує транспортне сполучення між населеними пунктами об'єднаної територіальної громади.

Дорожня мережа складається з твердого, шлакового та ґрунтового покриття. Асфальтовані дороги в задовільному стані. Необхідно проводити асфальтування всіх доріг села.

В селі існують 5 зупинок громадського транспорту. Існують 3 маршрути громадського транспорту.

Зовнішній автомобільний транспорт

Перевезення пасажирів у зовнішньому сполученні автомобільним транспортом здійснюється з автостанцій м. Запоріжжя, характеристики яких наведено нижче в таблиці.

Погоджено					
Інв. № об.	Підпис і дата	Зам. Інв. №			

Зм.	Кіл.	Арк.	№ док.	Підпис	Дата
-----	------	------	--------	--------	------

12.23

1/23-ПЗ

Аркуш

№	Найменування автостанції, адреса	Кількість відправлень автобусів на добу (од.)				Річний обсяг перевезень пасажирів за 2016р. (пас.)*			
		разом	міжміські	приміські	в т.ч. транзит	разом	міжміські	Приміські	
	Автостанції м. Запоріжжя:								
1	Запорізька АС-1 (АВ), пр.Соборності,20; I класу; 1,06 га; 1964р.	193	145	-	48	292,1	292,1	-	
2	Запорізька АС-2 Вул. Рекордна,37; II класу; 0,59 га; 1983р.	36	21	15	6	163,2	138,2	25,0	
3	Запорізька АС-3 вул.Жуковського,15 II класу; 0,11 га; 1963р.	53	39	14	-	193,6	142,1	51,5	
	Разом по АС м. Запоріжжя					648,9	572,4	76,5	
*в таблиці наведено офіційні дані по перевезенню пасажирів з автостанцій. В місті існують перевізники, які не надають звітних даних по перевезенню пасажирів та відправляються не з території діючих автостанцій									

Об'єкти господарського комплексу

ТОВ «НЕЗАЛЕЖНА АГРАРНА ІНДУСТРІЯ» вирощування зернових та технічних культур;

КП «БЛАГВОДСЕРВІС ШИРОКІВСЬКОЇ ГРОМАДИ» збір та обробка і розподіл води, будівництво водних споруд, електротехнічні та монтажні роботи, монтаж систем водопостачання, опалення та кондиціювання повітря;

ТОВ «ІНДУСТРІЯ, ЛТД» виробництво вапна та будівельного гіпсу, виробництво інших виробів із бетону, будівельного вапна та цементу, оптова торгівля лісоматеріалами, будівельними матеріалами та сантехнічним обладнанням, неспеціалізована оптова торгівля.

В селі функціонують такі фермерські господарства як:

ФГ «Азіс» (20473232)

ФГ «СКІФ» (20472681)

ФГ «Весна М» (33980959)

ФГ «РІС» (25478180)

ФГ «Буревісник» (22150935)

СФГ «ГАННА» (22150912)

Інженерна інфраструктура

Зм.	Кіл.	Арк.	№ док.	Підпис	Дата	12.23	1/23-ПЗ	Аркуш
-----	------	------	--------	--------	------	-------	---------	-------

с. Володимирівське забезпечене електропостачанням, газопостачанням, КП «Блазводсервіс Ширококівської громада» здійснює послуги з водопостачання.

Мережі водовідведення та дощової каналізації в селі відсутні.

В селі існує котельня.

Благоустрію та вертикальне планування виконані по всій території села в існуючих його межах і знаходяться в задовільному стані.

Небезпечних природних та техногенних процесів на території с. Володимирівське не зафіксовано.

2. Основні пріоритети та цільові показники соціального і демографічного розвитку території з метою формування повноцінного життєвого середовища

Метою оновлення Генерального плану є необхідність визначити пріоритетні пропозиції для перспективного розвитку с. Володимирівське на основі покращення умов проживання населення, забезпечення економічного зростання, удосконалення соціальної, виробничої, інженерно-транспортної інфраструктури поселення.

Основними пріоритетами подальшого розвитку с. Володимирівське є:

- створення комфортних умов для проживання населення,
- вдосконалення системи обслуговування, благоустрою та інженерно-транспортної інфраструктури,
- залучення інвестицій в сферу сільськогосподарської діяльності і обслуговування.

Перспективи розвитку с. Володимирівське визначаються в залежності від конкретних територіально-планувальних ресурсів, положення села в системі розселення, наявності і розподілу трудових ресурсів, враховуючи наявні санітарно-екологічні та інженерно-геологічні фактори, які створюють певні обмеження для розвитку села.

Основним місцем прикладання праці місцевих мешканців залишатиметься сільське господарство, яке необхідно вдосконалювати та відновлювати з метою покращення екологічного стану середовища та умов праці.

Рівень інвестиційної привабливості території с. Володимирівське можна вважати потенційно привабливим для інвестування у розвиток комерції та сільськогосподарського виробництва з модернізацією існуючих не діючих підприємств та розміщенням нових об'єктів підприємницької діяльності.

Згідно з Завданням на розроблення містобудівної документації проектна площа населеного пункту с. Володимирівське становитиме 1100 га.

Згідно з графічними матеріалами розрахункова проектна площа населеного пункту становитиме 924,40 га, в тому числі

Погоджено			
Інв. № об.	Зам. Інв. №		
	Підпис і дата		

територія житлової садибної забудови 591,19 га, територія житлової багатоквартирної забудови 22,60 га, відповідно до таблиці 6.1 ДБН Б.2.2-12:2019 ці території забезпечують нормативну численність населення в житловій садибній забудові $591,19:90=6568$ осіб, в житловій багатоквартирній забудові $22,60:8=2825$ осіб, сумарно-9393 особи, розрахункову чисельність населення можливо прийняти як 9800 осіб.

Орієнтовний склад населення на теперішній час в нових межах населеного пункту становить – 7350 осіб з них 3000 осіб ВПО та 1200 осіб мешканці дачних та садибних кооперативів.

Існуюча площа с. Володимирівське становить 499,48 га, проектна площа села в нових межах становить 924,40 га, населення 9800 осіб (станом на 01.01.2011 чисельність становила 3000 осіб, згідно з довідкою наданою замовником).

В даний час приріст населення села відбувається за рахунок ВПО (на даний час становить 3000 осіб), в органів місцевого самоврядування є наміри змінити межі села з метою включення інших територій, а саме території с. Сонячне, комеджного кварталу «Європа» та інші території промислового, інженерного та сільськогосподарського призначення, що призведе до суттєвого збільшення площі населеного пункту.

3. Характеристика території, необхідних для подальшого розвитку населеного пункту, а також території спільних інтересів суміжних територіальних громад.

Розширення меж населеного пункту здійснюється за рахунок території Широківської сільської ради Запорізького району Запорізької області.

Території, необхідні для подальшого розвитку населеного пункту, знаходяться в державній, колективній та приватній власності.

Територія населеного пункту в нових межах зі східного та південного напрямку межує з територією м. Запоріжжя, з північного та західного напрямку оточена сільськогосподарськими землями здебільшого приватної форми власності.

Відповідно до аналізу рівня соціально-економічного розвитку окремих токсинів Запорізької області Запорізький район відноситься до 3 типу токсинів із середнім показником потенціалу та середнім рівнем соціально-економічного та містобудівного розвитку. В районі планується розвиток багатоступеневої системи громадського обслуговування населення з розміщенням підприємств повсякденного та періодичного обслуговування.

4. Пропозиції щодо зміни меж населеного пункту.

Головною метою генерального плану є оптимізація структури об'єктів обслуговування, розвиток інженерної інфраструктури, забезпечення населення робочими місцями, вдосконалення

Погоджено					
Інв. № об.	Зам. Інв. №	Підпис і дата			

Зм.	Кіл.	Арк.	№ док.	Підпис	Дата
-----	------	------	--------	--------	------

1/23-ПЗ

Аркуш

транспортного обслуговування, включення додаткових територій, а саме з південного, південно-західного напрямків. Передбачено нова садибне будівництво та територія для багатоквартирного будівництва. В нові межі села включається територія існуючої садибної забудови с. Сонячного, комеджного кварталу «Європа», інших територій.

Планується розміщення локальних очисних споруд, мережі господарсько-побутової каналізації та мережі відведення поверхневих стічних вод з подальшим підключенням до мереж м. Запоріжжя.

Загальна площа населеного пункту збільшиться з 499,48 га, до 924,40 га.

5. Опис перспективної планувальної структури та функціонального зонування.

Проведений аналіз стратегічних напрямків територіального розвитку населеного пункту дозволив виявити перспективну модель територіально-планувального і функціонального розвитку міської структури з урахуванням усієї сукупності планувальних обмежень, властивостей і якостей території як села, так і прилеглої до неї території м. Запоріжжя.

Розроблена модель не має визначених часових рамок реалізації, вона покликана забезпечити сталість розвитку населеного пункту, його планувальної структури незалежно від важко прогнозованих інвестиційних процесів, які пов'язані з розвитком господарського комплексу. Рівень інвестицій в розвиток житлово-цивільного будівництва, інженерно-транспортної інфраструктури значною мірою не впливатиме на зміну функціонально-планувальних рішень, а лише на строки їх реалізації.

Модель перспективної планувальної структури населеного пункту дає можливість планомірного розвитку усіх функціональних зон на віддалену перспективу.

Існуюча частина села в існуючих його межах зберігається, перспективна планувальна структура села композиційно підпорядкована існуючій планувальній структурі, що склалася, Планувальна структура нових територій враховує транспортний коридор автомагістралі національного значення передбаченої Генеральним планом міста Запоріжжя, сформованої забудови міста.

Враховуючи значне збільшення території населеного пункту с. Володимирівське, планується розміщення додаткових підцентрів для забезпечення радіусів обслуговування. Так на території с. Володимирівське планується розміщення дитячих садків, школи, багатofункціонального спортивно – розважального центру з реконструкцію існуючого стадіона, об'єктів громадського харчування, інших об'єктів обслуговування населення.

На території комеджного кварталу «Європа» заплановане розміщення вбудованого в адмінбудинок дитячого садка та

Погоджено		
Інв. № об.	Зам. Інв. №	Підпис і дата

підприємства громадського харчування, передбачається розміщення об'єктів обслуговування населення.

В центральній частині села Володимирівське, в нових його межах, заплановане розміщення багатоквартирної житлової забудови вздовж нової вулиці, що є продовженням вул. Товариської м. Запоріжжя та прокладається до вул. Петра Калнишевського с. Володимирівське з розміщенням об'єктів обслуговування на перших поверхах житлових будинків, або окремо розташованих.

Планується збільшення території зелених насаджень в центрі населеного пункту та на нових територіях населеного пункту. Ділянки громадських центрів мають транспортні та пішохідні зв'язки з існуючою забудовою.

Існуюче кладовище планується к закриттю, нове розміщуються за межами населеного пункту.

Транспортна структура села вдосконалюється за рахунок нових територій, уточнюються поперечні профілі вулиць, доріг та проїздів. Передбачається тверде покриття всіх вулиць населеного пункту.

Типи територіальних зон, встановлених в межах населеного пункту

ГРОМАДСЬКІ ЗОНИ	Г-2 п	Ділова зона
	Г-3	Навчальна зона
	Г-3-1 п	Зона шкіл та ДНЗ (проектна)
	Г-4 п	Культурна та спортивна зони (проектна)
	Г-4-4	Зона розміщення культових та обрядових споруд
	Г-6	Торгівельна зона
ЖИТЛОВІ ЗОНИ	Ж-1	Зона садибна забудова
	Ж-1 п	Зона садибна забудова (проектна)
	Ж-4	Багатоквартирна забудова
	Ж-4 п	Багатоквартирна забудова (проектна)
ЛАНДШАФТНО-РЕКРЕАЦІЙНІ ЗОНИ	Р-3 п	Рекреаційна зона озелених територій загального користування (проектна)
ЗОНИ ТРАНСПОРТНОЇ ІНФРАСТРУКТУРИ	ТР-1	1 зона транспортної інфраструктури
	ТР-2	2 зона транспортної інфраструктури
	ТР-1-3	Зона транспортної інфраструктури населеного пункту
	ТР-1-3 п	Зона транспортної інфраструктури населеного пункту (проектна)
ЗОНИ ІНЖЕНЕРНОЇ ІНФРАСТРУКТУРИ	ІН-1	Зона об'єктів електромережі
КОМУНАЛЬНО-СКЛАДСЬКІ ЗОНИ	КС-3	Зона розміщення об'єктів 3-го класу санітарної класифікації
	КС-5	Зона розміщення об'єктів 5-го класу санітарної класифікації

Інв. № об. Підпис і дата Зам. Інв. №

Погоджено

12.23

1/23-ПЗ

Аркуш

Зм. Кіл. Арк. № док. Підпис Дата

	КС	Зона розміщення об'єктів без необхідності екологічних наслідків
	КС п	Зона розміщення об'єктів без необхідності екологічних наслідків (проектна)
ВИРОБНИЧІ ЗОНИ	В-4	Зона підприємств 4 класу шкідливості
	В-5	Зона підприємств 5 класу шкідливості
	В-6	Зона розміщення підприємств без екологічних наслідків
СПЕЦІАЛЬНІ ЗОНИ	СВ-1	Зона земель сільськогосподарського призначення
	СВ-2	Зона сільськогосподарських підприємств, установ та організацій
	С-4	Зона озеленення спеціального призначення
	С-4 п	Зона озеленення спеціального призначення (проектна)

6. Характеристика території та визначення заходів щодо їх освоєння.

В межах населеного пункту розташовані різні за призначенням території, а саме:

Територія громадської забудови.

Організація системи громадського обслуговування створює умови для раціонального забезпечення всебічних потреб населення у різних видах послуг, які реалізуються в установах і підприємствах обслуговування.

Об'єкти обслуговування об'єднуються за ознакою спільності свого функціонального призначення та утворюють відповідні мережі установ і підприємств (навчально – виховні установи, установи культури, охорони здоров'я, спортивні та фізкультурно – оздоровчі, підприємства торгівлі, громадського харчування, побутового обслуговування та ін.).

Сукупність мереж установ і підприємств обслуговування утворює єдину систему обслуговування, яка є важливим елементом соціальної інфраструктури населеного пункту.

Основним принципом розміщення установ та підприємств обслуговування є створення зручних умов для одержання населенням необхідного виду, рівня та якості послуг.

Розвиток місцевої мережі, яка забезпечує комплексність забудови відбуватиметься в напрямку доведення до нормативних показників забезпеченості населення об'єктами обслуговування в районах як існуючої забудови, так і в районах перспективного будівництва.

Аналіз цих показників дає можливість зробити висновок про недостатній розвиток деяких видів обслуговування, в зв'язку з

Погоджено		
Інв. № об.	Зам. Інв. №	
	Підпис і дата	

чим виникає потреба в розміщенні додаткових об'єктів для задоволення потреб населення.

Незважаючи на те, що кількість місць в загальній школі задовольняє потреби населення в ній, є потреба в збільшенні кількості об'єктів за рахунок новобудов у районах нового житлового будівництва.

В с. Володимирівське проектом генерального плану передбачається вдосконалення система розміщення нових об'єктів обслуговування та збереження існуючих для забезпечення повсякденних і періодичних потреб населення села та територіальної громади.

Торгівельні об'єкти концентруються біля адміністративного центру та підцентрів рівномірно розташованих на всій території села.

Таким чином, проектом оновленого генерального плану передбачається розвиток систем повсякденного та періодичного обслуговування населення на первинному рівні з реконструкцією існуючих об'єктів та будівництвом нових.

Розміщення нових дитячих дошкільних установ передбачене в районах нової забудови та в районах реконструкції житлової забудови.

Для традиційного захоронення населення передбачено кладовище в районі с. Високозірне – 50 га

Територія житлової забудови.

Проектом генерального плану на розрахунковий період збережена існуюча житлова забудова, крім того, проектом пропонується упорядкування існуючої житлової забудови шляхом використання всіх вільних ділянок в межах існуючої житлової забудови населеного пункту. Передбачене розташування додаткової садибної забудови. Основний вид забудови – житлові будинки садибного типу.

Генеральним планом також передбачене багатоквартирне житлове будівництво в центральній частині населеного пункту в нових його межах.

Територія ландшафтна – рекреаційна.

Проектом генерального плану передбачається розвиток системи зелених насаджень в с. Володимирівське та місць відпочинку селян. Рекреаційна зона включає організацію природньої зони відпочинку в центральній частині села.

Доповнює розвиток рекреаційної зони парк в центральній частині села з дитячим ігровим майданчиком.

Зелена зона в селі формується також за рахунок озеленених ділянок громадських будівель та індивідуальних садиб. Зелені насадження, розташовані на ділянках рекреаційної зони, вуличної мережі, громадських будівель, житлової садибної забудови

Погоджено			
Інв. № об.	Підпис і дата		Зам. Інв. №

Зм.	Кіл.	Арк.	№ док.	Підпис	Дата	12.23	1/23-ПЗ	Аркуш
-----	------	------	--------	--------	------	-------	---------	-------

Територія сільськогосподарського призначення використовується для вирощування сільськогосподарських культур, садівництва, вирощування декоративних рослин, тощо.

До сільськогосподарських територій відносяться території сільськогосподарських підприємств розташовані в північно-східній, східній та інших частинах села в існуючих та нових його межах.

7. Пропозиції щодо формування системи громадських центрів.

Згідно до ДБН Б.2.2-12:2018 площа громадського центру сільського населеного пункту повинна розраховуватися 10-20 м² на особу. Розрахунковий розмір площі громадського центру села становитиме:

$9800 \text{ мешканців} \times (10)20 \text{ м}^2 = (98000 \text{ м}^2) 196000 \text{ м}^2 \text{ або } 19,60 \text{ га.}$

Зона громадського центру на розрахунковий період становить 32,45 га, тобто $324500 \text{ м}^2 / 9800 \text{ мешканців} = 33,11 \text{ м}^2$ на одного мешканця.

Розвиток центру здійснюються шляхом реконструкції та технічного переоснащення існуючих громадських будинків та споруд, перепрофілювання існуючих об'єктів, будівництво нових об'єктів: суміщення об'єктів різного типу, розміщення об'єктів повсякденного та періодичного обслуговування у вбудовано-прибудованих приміщеннях, в тому числі у перших поверхах садибних та багатоквартирних будинків.

Окремий громадський центр формується вздовж вул. Проектна 23, яка охопить більшість мешканців населеного пункту.

Також мешканці населеного пункту використовують інші об'єкти інфраструктури Широківської об'єднаної територіальної громади та м. Запоріжжя

Перелік і розрахункові показники нормативної забезпеченості об'єктами громадського обслуговування населення в с. Володимирівське відповідно до Додатку Е.1 (обов'язковий) ДБН Б.2.2-12:2019 з розрахунку на 1000 жителів

№ п/ п	Установи та організації	Одиниц я виміру	Повсяк денним и	Періодичними та епізодичними	Примітки	
					існуючі	додаткові
1.	Заклади дошкільної освіти	місць	3-6 років 100%	По завданню	120 місць	291 місць
	Загально	місць	100%	Те саме		

2	освітні школи		I-II ступені в 90% III ступеня		320 учнів	255 В існуючих учбових закладах територіальної громади
3	Кабінети сімейних лікарів загальної практики, амбулаторії	Відвідувань в зміну	-	-	Амбулаторія	
4	Аптеки	Об'єкт (м2 заг. площі)	-	-	1	-
5	Спортивні зали загального користування	м2 заг. площі	40	40	-	400
6	Басейни	місць	20 м2 дзеркала води	20	-	200
7	Бібліотеки	місць	2 місця	2	-	20
8	Клубні приміщення	місць	15-20	-	-	150-200
9	Культові споруди	по завданню		По завданню	1	-
10	Магазини продовольчі	м2 торг. площі	15	10	215,7	-
11	Магазини непродовольчі	М2 торг. площі	20	12	177,6	30
12	Ринки	м2 торг. пл.	-	20-30	-	200-300
12	Підприємства громадського харчування	пос/місць	7	20	2об'єкти	-
13	Підприємства побутового обслуговування	робочих місць	1,5-2	3	-	15-20
14	Центри адміністративні	Об'єкт	-	По завданню	-	В с. Широке

Погоджено		

Зам. Інв. №

Підпис і дата

Інв. № об.

12.23

1/23-ПЗ

Аркуш

Зм. Кіл. Арк. № док. Підпис

Дата

	их послуг					
15	Відділення зв'язку	Об'єкт	0,16	-	-	10
16	Відділення банків	Операції не місце	-	1-2	-	10-20
17	Відділення поліції	Об'єкт	-	По завданню	-	В с. Широке
18	Пожежні депо	пожежних машин	-	По завданню	-	1 об'єкт На 2 авто
19	Громадські будиральні	прилад	1	-		В громадських об'єктах
20	Кладовище	за	-	0,24-0,35		2,4-3,5

8. Обсяги житлового будівництва.

Обсяг і структура житлового будівництва в межах села Володимирівське визначені виходячи з необхідності досягнення цільових стандартів житла, тобто забезпечити кожному родину окремою квартирою або будинком виглядає таким чином: існуючий стан в існуючих межах - 161 садиб та 8 багатоквартирних будинків.

Орієнтовний склад населення на теперішній час в нових межах населеного пункту становить - 7350 осіб з них 3000 осіб ВПО та 1200 осіб мешканців дачних та садибних кооперативів.

Розрахункова чисельність населення 9800 осіб.

Згідно оновленої планувальної структури с. Володимирівське плануються нові садибні та багатоквартирні будинки з громадською забудовою на всіх майданчиках.

Розподіл земельних ділянок які плануються для житлового садибного та багатоквартирного фонду, та трасування житлових вулиць та проїздів в межах кварталів виконати при розробці детального плану території (за необхідністю)

9. Напрями розвитку вулично – дорожньої мережі, транспорту, інженерної інфраструктури.

Мережа вулиць населеного пункту села Володимирівське наразі переважним чином сформована і в цілому забезпечує зручні зв'язки між усіма функціональними зонами в існуючих межах.

Оновленим генеральним планом передбачено впорядкування вулично – дорожньої мережі на території існуючої громадської та садибної забудови, нової садибної забудови та території сільськогосподарських підприємств.

Погоджено			
Інв. № об.	Підпис і дата	Зам. Інв. №	

Зм.	Кіл.	Арк.	№ док.	Підпис	Дата	12.23	1/23-ПЗ	Аркуш
-----	------	------	--------	--------	------	-------	---------	-------

Головними вулицями села є вул. Петра Калнишевського, вул. Шкільна, вул. Шевченка в північній його частині, житловими є вул. Л. Українки, Польова, Грушевського, Стуса, Ювілейна, Кринична, Жемчужна, Космічна та інші. В східній частині села головними є вул. Лісна та Ясна. В центральній частині села вул. Дніпровські пороги та Вишнева. В південно-західному напрямку головними вулицями є вул. Ярослава Мудрого, Олександрівська, Виноградна, житловими є вул. Степова, Будівельників та інші.

На територіях нової житлової забудови генеральним планом передбачено будівництво нових вулиць і продовження існуючих.

Більшість вулиць має тверде асфальтобетонне покриття і освітлення, проте тротуари переважно відсутні. Частина вулиць в периферійній частині населеного пункту має ґрунтове покриття. Необхідне удосконалення або заміна існуючого асфальтобетонного покриття, яке знаходиться в незадовільному стані та влаштування нового асфальтобетонного покриття на ґрунтових проїзних частинах, влаштування тротуарів і загалом приведення параметрів поперечного профілю вулиць у відповідність до рекомендацій ДБН В.2.3-5:2018 "Вулиці та дороги населених пунктів"

Ширина вулиць і доріг визначається залежно від категорії, складу елементів, які розміщуються в межах поперечного профілю, з урахуванням санітарно – гігієнічних вимог і вимог цивільної оборони.

Класифікація вулиць і доріг сільських населених пунктів визначають згідно з ДБН Б.2.2-12:2019.

Поперечні профілі вулиць, доріг та проїздів наведені на кресленні Схема руху транспорту та пішоходів.

Вулично-дорожня мережа населеного пункту – вільної конфігурації. Радіуси заокруглення на перехрестях вулиць прийняті 9,0 м. Рух транспортних засобів по вулицях двосторонній, ширина смуги руху прийнята 3,0 м, ширина проїзної частини – 6,0 м.

Уздовж проїжджої частини житлових вулиць проектом передбачено організацію вело доріжок поєднану з тротуаром, шириною від 2,5 м. Згідно з таблицею 5.1 ДБН В.2.3-5:2018 «Вулиці та дороги населених пунктів» можуть бути передбачені проїзди з шириною смуги 2,75 м якщо проектується 2 смуги або шириною 4 м при одній смузі.

Транспорт.

Рейсовий пасажирський транспорт для внутрішньо сільських перевезень влаштовувати недоцільно. Використовуються пішохідний та велосипедний рух, а також особистий авто- і мототранспорт. Місця зберігання транспортних засобів на території присадибних ділянок. Для короткострокового паркування в необхідних місцях вулиць і доріг слід передбачати автостоянки і місця для зберігання велосипедів.

Погоджено					
Інв. № об.	Зам. Інв. №	Підпис і дата			

Зм.	Кіл.	Арк.	№ док.	Підпис	Дата	12.23	1/23-ПЗ	Аркуш
-----	------	------	--------	--------	------	-------	---------	-------

здійснювати відповідно до діючих норм технологічного проектування зазначених об'єктів.

Спеціальні заходи з інженерної підготовки.

Як засіб попередження виникнення негативних природних і техногенних факторів потрібно використовувати природні властивості природних систем та їх компонентів.

Також слід застосовувати агролісотехнічні заходи, зокрема підтримувати в належному стані і поповнювати зелені насадження як в спеціальних зонах, так і в зонах загального користування.

11. Пропозиції щодо охорони навколишнього середовища, подолання та запобігання впливу проявів негативних природно – техногенних факторів для поліпшення життєвого середовища.

При проектуванні розвитку існуючих сільських поселень слід користуватися вимогами наведеними в ДБН Б.2.2-12:2019 та вимогами наведеними в розділі 8 ДСП 173-96 «Державні санітарні правила планування і забудови населених пунктів»

Охорона навколишнього середовища повинна забезпечуватись комплексом захисних заходів планувального, технологічного, санітарно-технічного і організаційного характеру з метою створення сприятливих умов проживання, праці та відпочинку населення, збереження і зміцнення здоров'я мешканців.

Генеральним планом передбачені санітарно-захисні зони навкруги діючих підприємств, комунальних та інших об'єктів. В санітарно-захисних зонах необхідно дотримуватися вимог п. 5.12, 5.13, 5.14 ДСП 173-96.

Площа кладовища для сільських населених пунктів повинна бути з розрахунку 0,1 га на 1000 мешканців. Відповідно до п. 4.2.30 ДБН Б 2.2-1:2008 «Кладовища, крематорії та колумбарії. Норми проектування» проектується захисна зона зелених насаджень спеціального призначення навколо кладовища за вширшки 20 метрів. Генеральним планом пропонується закриття кладовищ з подальшим зменшенням санітарно-захисних зон до 100 метрів. Відповідно до додатку Е.1 ДБН Б.2.2-12:2019 площа кладовища традиційного поховання становить 0,24-0,35 га. На 1000 мешканців з СЗЗ 300м.

Генеральним планом передбачені охоронні зони вздовж ПЛЕ. Визначені санітарно – захисні зони існуючих об'єктів інженерної інфраструктури та діючих підприємств і споруд.

Необхідно виконати озеленення санітарно-захисних смуг у відповідності до вимог ДСП 173-96

Покращувати озеленення житлових і громадських територій, а також озеленених територій загального користування і ландшафтно-рекреаційних територій.

З метою охорони і оздоровлення навколишнього середовища та для забезпечення екологічної стійкості території до техногенного навантаження у проекті рекомендовано виконати ряд планувальних

Погоджено										
Інв. № об.	Підпис і дата	Зам. Інв. №								
Зм.	Кіл.	Арк.	№ док.	Підпис	Дата	12.23			1/23-ПЗ	Аркуш

і технічних заходів. Намічений комплекс заходів повинен реалізовуватись через дію законів України щодо екологічного стану та санітарно- епідеміологічного контролю території, місцевого самоуправління.

Стосовно формування і зменшення СЗЗ території виробництва, комунально-складських, сільськогосподарських підприємств, 4-5 класу шкідливості, необхідно зазначити, що в умовах сьогодення це надзвичайно складне питання. У відповідності з ДСН 173-96 (п. 5.14) проекти організації СЗЗ слід розробляти в комплексі з проектом будівництва (реконструкції) підприємства з першочерговою реалізацією заходів передбачених в СЗЗ, тобто проблема організації СЗЗ є складовою виробничо-технологічного процесу самих підприємств. Враховуючи те, що в умовах сформованого населеного пункту витримати вимоги по територіальних розривах СЗЗ у більшості випадків неможливо, головне завдання підприємств що їх створюють полягає у впровадженні новітніх технологій які впроваджуються при розробці спеціалізованих проектів з подальшим погодженням скорочення даних нормативів СЗЗ до мінімально-можливих розмірів центральними державними санітарно-епідеміологічними службами МОЗ України. Механізмом реалізації даних вимог є законодавча база по охороні довкілля через механізм приписів, штрафів, компенсаційно-соціальних виплат та закриття виробництв державними контролюючими органами.

Для забезпечення санітарно-гігієнічних умов на території житлової забудови пропонується:

-заборона підхоронення на місці існуючого поховання в межах ділянок існуючого кладовища, з метою зменшення їх СЗЗ після закінчення кладовищного періоду; дотримання СЗЗ до житлової забудови при відведенні нової ділянки під кладовище;

Щодо охорони атмосферного повітря:

-інвентаризація всіх джерел викидів, забезпечення контролю за нештатними ситуаціями, запровадження сучасних технологій на підприємствах-забруднювачах повітря з розробкою їх екологічних паспортів та планувальною організацією території підприємства і упорядкуванням та озелененням їх СЗЗ;

-екологічно спрямовані напрямки розвитку зовнішніх і внутрішніх транспортних зв'язків, вулично-магістральної мережі та транспортних засобів міста: відведення транзитних транспортних потоків; раціональна організація руху транспорту; подальший розвиток вулично-дорожньої мережі – будівництво нових та реконструкція існуючих з сучасними технічними параметрами доріг, транспортних розв'язок тощо;

-створення зелених насаджень вздовж вулиць для захисту від шуму та загазованості території житлово-громадського призначення.

-впровадження новітнього устаткування для обприскування дерев, що мінімізують розпилення хімічних засобів захисту рослин в оточуюче середовище та створюють мінімальні параметри зони санітарного розриву від ділянок садів, що обприскуються

Погоджено					
Інв. № об.	Підпис і дата		Зам. Інв. №		

Зм.	Кіл.	Арк.	№ док.	Підпис	Дата	12.23	1/23-ПЗ	Аркуш
-----	------	------	--------	--------	------	-------	---------	-------

(застосування сучасної техніки з розпилювачами високого ступеню точності для садових культур, що мають мінімальні параметри розсіювання аерозолів у повітрі та не здійснюють шкідливого впливу на прилеглий території житлової забудови) У разі неможливості застосування аерозольних методів обприскування, з метою створення необхідного санітарного розриву, переведення частини ділянок садів, що безпосередньо межують з житловою та громадською забудовою, в ділянки селекції інших культур, умови вирощування яких дозволяють забезпечити санітарно-гігієнічні умови на прилеглих ділянках житлово-громадської забудови, або перевести ділянки в землі іншого функціонального призначення.

Щодо охорони водного басейну:

- підземні та підруслові води, що відповідають санітарно-гігієнічним вимогам, повинні використовуватись переважно для господарсько-питного водопостачання. Використання підземних вод питної якості для потреб, що не пов'язані з господарсько-питним водопостачанням не допускається;

- налагодження сучасної системи централізованого водовідведення з будівництвом каналізаційної мережі та підключення всього існуючого і проектного житлового фонду та інших об'єктів водоспоживання до централізованої системи водовідведення;

У плані охорони ґрунтів:

- проведення геохімічного обстеження ділянок нового будівництва;

- дотримання вимог щодо санітарного очищення території, забезпечення 100% охоплення сільської території планово-подвірною санітарною очисткою, розвиток системи роздільного збору сміття, ліквідація несанкціонованих звалищ побутових відходів та інші

- проведення рекультивції порушених ділянок; бережливе ставлення до родючого шару ґрунтів які зазнають його механічного зняття, залуження та закріплення його на ділянках поверхневого змиву тощо;

- впровадження комплексу заходів з інженерної підготовки території, в тому числі що зазнають впливу несприятливих природних процесів: регулювання поверхневого стоку, ліквідація підтоплення, благоустрою і розчищення водоїм; розчистка русел струмків та балок з ліквідацією штучних перепон для поверхневого стоку і ін.

Щодо фізичних факторів впливу на навколишнє середовище (шум, електромагнітне випромінювання та інші):

Основним джерелом шумового забруднення є автомобільний транспорт.

При прийнятті проектних рішень враховуються зазначені зони акустичного впливу.

Забезпечення нормативного санітарно-гігієнічного стану в тому числі в плані акустичного забруднення прилеглих до автомобільних магістральних вулиць території забезпечується переважно за рахунок створення придорожніх захисних зелених

Погоджено			
Інв. № об.	Підпис і дата		Зам. Інв. №

Зм.	Кіл.	Арк.	№ док.	Підпис	Дата	12.23	1/23-ПЗ	Аркуш
-----	------	------	--------	--------	------	-------	---------	-------

насаджень та дотримання правил землекористування в межах захисних смуг доріг з дотриманням санітарних розривів

В межах червоних ліній магістральної вуличної мережі пропонується застосування також конструктивних шумозахисних заходів для першої лінії забудови (шумозахисні екрани, шумозахисні віконні блоки, шумопоглинаючі облицювальні матеріали).

Для забезпечення нормативних рівнів шуму на території житлової забудови пропонується:

- від вуличної мережі на вільних територіях в межах існуючої житлової забудови в межах червоних ліній та на ділянках нового містобудівного освоєння організація протишумового озеленення відповідно вимог ДСН 173-96 (п.5.25);

- на ділянках де досягти нормативних рівнів шуму за рахунок озеленення неможливо, впровадження конструктивних шумозахисних заходів для першої лінії забудови (шумозахисні екрани, шумозахисні віконні блоки, шумопоглинаючі облицювальні матеріали);

- При проектуванні нових та реконструкції існуючих автомобільних доріг для забезпечення акустичного режиму необхідно враховувати вимоги ПП. 4.5, 5.25, 5.26, 8.40 ДСП 173-96 у відповідності до п. 5.14 цих норм. та розробка розділу «Захист від шуму» у складі проектної документації, інструментальні вимірювання шуму.

- Заходи по забезпеченню акустичного режиму в населеному пункті від автотранспортних доріг «Вулиці та дороги населених пунктів» ДБН В.2.3-5:2018, відповідно до п. 4.6.5 передбачити заходи із шумо-захисту: улаштування шумозахисних споруд, смуг шумозахисних зелених насаджень, відведення частини транспортного потоку на інші вулиці (дороги), організацію переважно безупинного руху транспорту.

- Відповідно до п 4.6.6 Технічні рішення і параметри шумозахисних споруд, конструкцій та матеріали для їх виготовлення повинні визначатися відповідно до їх акустичних характеристик довговічними, стійкими до різних природних впливів, простими при будівництві та експлуатації, відповідати архітектурі прилеглої забудови, забезпечувати належне та безпечне водовідведення з проїзної частини. Шумозахисні споруди не повинні перешкоджати пішоходам під час переходу вулиці та погіршувати режим інсоляції прилеглої території.

Ландшафтно-планувальні заходи:

- проведення інвентаризації системи зелених насаджень населеного пункту у відповідності з вимогами п. 6.8 „Правил утримання зелених насаджень міст та інших населених пунктів”;

- формування зелених насаджень спеціального призначення (санітарно-захисні зони, протишумове озеленення в межах впливу автодоріг); формування зелених насаджень обмеженого використання: озеленення та ландшафтне впорядкування при домових територіях;

- формування локальних місць рекреаційного використання (скверів, парків) з їх благоустроєм та ландшафтною організацією

Погоджено					
Інв. № об.	Підпис і дата	Зам. Інв. №			
Зм.	Кіл.	Арк.	№ док.	Підпис	Дата

12.23

1/23-ПЗ

Аркуш

(дендрологічний склад, малі архітектурні форми); утримання зелених насаджень в здоровому, упорядкованому стані, створення та формування декоративних та ефективних в екологічному відношенні, стійких до техногенних навантажень насаджень паркових зон;

- організація екологічної мережі за рахунок зелених насаджень загального користування, гідрографічних систем, їх прибережних захисних смуг тощо, як джерел відновлення і збереження екологічного балансу та забезпечення сталого розвитку території міста; виконання заходів по впорядкуванню та догляду за станом зелених насаджень території природно-заповідного фонду;

- з метою охорони та збереження природних екосистем та для додержання вимог законодавства у сфері регулювання земельних відносин, використання та охорони земель для існуючих об'єктів ПЗФ необхідно виконати винесенням їх меж в натурі відповідно Технічної документації із землеустрою щодо встановлення меж земельних ділянок;

- налагодження в селі системи моніторингу навколишнього природного середовища (повітряний та водний басейни, ґрунт) з організацією стаціонарних постів та пунктів контролю в межах житлової, рекреаційної зони та в місцях впливу виробничих та комунальних об'єктів

Впровадження вищезазначених заходів сприятиме покращенню умов проживання, оздоровленню навколишнього середовища та підвищенню його екологічної стійкості до техногенних навантажень.

З метою охорони і оздоровлення навколишнього середовища та для забезпечення екологічної стійкості території до техногенного навантаження у проекті рекомендовано виконати ряд планувальних і технічних заходів.

Для територіально-планувальної організації села з урахуванням планувальних обмежень як зон регулювання та обмеження забудови.

Охорона навколишнього середовища повинна забезпечуватись комплексом захисних заходів планувального, технологічного, санітарно-технічного і організаційного характеру з метою створення сприятливих умов проживання, праці та відпочинку населення, збереження і зміцнення здоров'я мешканців.

При проектуванні нових та реконструкції існуючих автомобільних доріг для забезпеченню акустичного режиму необхідно враховувати вимоги ПП. 4.5, 5.25, 5.26, 8.40 ДСП 173-96 у відповідності до п. 5.14 цих норм. та розробка розділу «Захист від шуму» у складі проектної документації, інструментальні вимірювання шуму.

Заходи по забезпеченню акустичного режиму в населеному пункті від автотранспортних доріг «Вулиці та дороги населених пунктів» ДБН В.2.3-5:2018, відповідно до п. 4.6.5 передбачити заходи із шумо-захисту: улаштування шумозахисних споруд, смуг шумозахисних зелених насаджень, відведення частини

Погоджено					
Інв. № об.	Підпис і дата		Зам. Інв. №		

Зм.	Кіл.	Арк.	№ док.	Підпис	Дата	12.23	1/23-ПЗ	Аркуш
-----	------	------	--------	--------	------	-------	---------	-------

транспортного потоку на інші вулиці (дороги), організацію переважно безупинного руху транспорту.

Відповідно до п 4.6.6 Технічні рішення і параметри шумозахисних споруд, конструкцій та матеріали для їх виготовлення повинні визначатися відповідно до їх акустичних характеристик довговічними, стійкими до різних природних впливів, простими при будівництві та експлуатації, відповідати архітектурі прилеглої забудови, забезпечувати належне та безпечне водовідведення з проїзної частини. Шумозахисні споруди не повинні перешкоджати пішоходам під час переходу вулиці та позіршувати режим інсоляції прилеглої території.

Генеральним планом передбачений вивіз твердих побутових відходів з території села на найближчий полігон ТПВ. На території Широківської сільської ради біля с. Зеленопілля, розташована земельна ділянка під будівництво полігону ТПВ №3, після введення в експлуатацію якого, питання вивозу відходів з території громади буде вирішено остаточно.

Для зменшення негативного впливу на навколишнє середовище пропонується влаштування санітарно-захисних зон навкруги всіх сільськогосподарських підприємств та встановлення охоронних зон навкруги, або вздовж інженерних мереж та об'єктів. Покращують ситуацію запроектовані зелені насадження спеціального призначення та загального користування біля існуючого кладовища. Оскільки в трьохсотметрову санітарно-захисну зону існуючого кладовища потрапляють значні території житлової забудови, кладовище підлягає закриттю. Після припинення нових захоронень та завершення кладовищного періоду (15 чи 20 років) слід розглянути можливість скорочення СЗЗ до 100 м. При цьому необхідно оформлення відповідного висновка згідно з п. 3.12 ДСанПіН 2.2.2.028-99; п.п. 5.7-5.9 ДСП 173-96.

В СЗЗ від кладовищ заборонено користуватися водою з колодязів та підземних джерел; необхідне першочергове 100% охоплення житлових будинків, що знаходяться у 300-метровій СЗЗ кладовищ централізованими мережами водопостачання та водовідведення, а крім того, необхідний постійний контроль за якістю продукції, що вирощується на цих ділянках (з метою попередження отруєнь). Дані обмеження включаються до будівельних паспортів відповідних ділянок.

12. Пропозиції щодо збереження та нерухомих пам'яток культурної спадщини, територій, що мають статус земель історико – культурного призначення.

Запорізька обласна державна адміністрація своїм листом № 04144/08-27 від 22.05.2019 «Про визначення та врахування державних та регіональних інтересів під час розроблення генерального плану села Володимирівське» зазначила що при розробленні містобудівної документації необхідно дотримання вимог

Погоджено					
Інв. № об.	Підпис і дата	Зам. Інв. №			

Зм.	Кіл.	Арк.	№ док.	Підпис	Дата	12.23	1/23-ПЗ	Аркуш
-----	------	------	--------	--------	------	-------	---------	-------

Законів України «Про охорону культурної спадщини» і «Про охорону археологічної спадщини».

На території та за сучасними межами села Володимирівське Запорізького району розташована пам'ятка археології місцевого значення, взята на облік рішенням виконкому Запорізької обласної ради народних депутатів від 26.11.1985 № 434–курзанний могильник з 3 курганів, охоронний № 2334, розташований на південно-західній околиці села Володимирівське.

13. Рекомендації щодо встановлення режиму використання територій, визначених для майбутніх містобудівних потреб.

Проектним рішенням оновленого генерального плану села Володимирівське нове житлове будівництво передбачається здійснювати відповідно до структури житлової забудови.

При забудові сільбищних територій, території громадського центру та під центрів, територій сільськогосподарського, комунального та промислового призначення необхідно керуватися вимогами зонінга, який розроблений в розвиток генерального плану і являється його невід'ємною частиною.

У разі виникнення потреби в межах існуючих ділянок передбудови старих або будівництва нових об'єктів, необхідно передбачати заходи щодо розміщення об'єктів в межах земельної ділянки згідно зонуванню території на вільних від забудови територіях.

Суттєвим є те що в нові межі села включаються досить велика кількість земель які в дійсний час мають існуючу житлову та іншу забудову.

Велике значення для структури села має збільшення зелених зон загального користування.

Генеральним планом частково враховані рішення транспортної мережі міста Запоріжжя.

14. Рекомендації щодо розроблення плану зонування території або черговості виконання плану зонування його окремих частин та детальних планів територій.

Генеральний план з планом зонування села Володимирівське, у відповідності до існуючого законодавства, публікується в засобах масової інформації, сільська рада ініціює і організовує обговорення проекту. Проект погоджується з відповідними службами і затверджується сільською радою.

У відповідності до першочергових заходів виділяються об'єкти, на які розробляється проектна документація для подальшого будівництва, за необхідністю детальні плани окремих функціональних зон, робочі проекти окремих будівель та споруд, враховуючи суттєве збільшення території села та численності його мешканців.

Погоджено					
Інв. № об.	Підпис і дата				
Зам. Інв. №					

15. Розрахункові показники та заходи що до розвитку Житлового будівництва.

Згідно з Завданням на розроблення містобудівної документації проектна площа населеного пункту с. Володимирівське становитиме 1100,00 га. Згідно з графічними матеріалами розрахункова проектна площа населеного пункту становитиме 924,40 га, в тому числі територія житлової садибної забудови 591,19 га, територія житлової багатоквартирної забудови 22,60 га, відповідно до таблиці 6.1 ДБН Б.2.2-12:2019 ці території забезпечують нормативну численність населення в житловій садибній забудові $591,19:90=6568$ осіб, в житловій багатоквартирній забудові $22,60:8=2825$ осіб, сумарно-9393 особи, розрахункову чисельність населення прийнято як 9800 осіб.

Відповідно до довідки сільської ради населеній пункт налічує 1614 садиб та 8 багатоквартирних будинків. В старих та нових межах села налічуються незабудовані ділянки.

Додаткова територія садибної забудови на розрахунковий період складає 247,12 га, тобто 1647 ділянки по 0,1500 га з житловим фондом в 197640 м² з орієнтовною площею одного будинку для 3-4 осіб 120 м².

Багатоквартирна додаткова територія 21,50 га для розміщення житлових 3-х поверхових будинків, тобто згідно табл. 6.1 ДБН Б.2.2-12:2019 цієї території вистачає для розміщення 2150 осіб $\times 35,0 \text{ м}^2/\text{осіб} = 75250 \text{ м}^2$ додаткової площі багатоквартирної забудови.

Проектним рішенням нове житлове будівництво, а саме освоєння ділянок для нового садибного будівництва пропонується здійснювати відповідно до структури житлової забудови, пропонується садибна забудова на вільних ділянках.

Багатоквартирне будівництво планується в центральній частині села..

Системи громадських центрів.

Згідно до ДБН Б.2.2-12:2018 площа громадського центру сільського населеного пункту повинна розраховуватися 10-20 м² на особу. Розрахунковий розмір площі громадського центру села становитиме:

$9800 \text{ мешканців} \times (10)20 \text{ м}^2 = (98000 \text{ м}^2) 196000 \text{ м}^2$ або 19,60 га.

Зона громадського центру на розрахунковий період становить 32,45 га.

Розвиток громадського центру та підцентрів здійснюються шляхом реконструкції та технічного переоснащення існуючих громадських будинків та споруд, перепрофілювання існуючих об'єктів, будівництво нових об'єктів: суміщення об'єктів різного типу, розміщення об'єктів повсякденного та періодичного

Погоджено		

Зам. Інв. №

Підпис і дата

Інв. № об.

Зм.	Кіл.	Арк.	№ док.	Підпис	Дата	12.23	1/23-ПЗ	Аркуш

об'їзної дороги, що проходить поза межами міста, становить 29,2 км, а загальна протяжність становить 43,7 км. Ширина магістральних вулиць в межах червоних ліній, на яких передбачається безперервний рух, становитиме 60–85 метрів.

Вулично – дорожня мережа існуюча та проектна планується з твердим покриттям.

Головними вулицями села є вул. Петра Калнишевського, вул. Шкільна, вул. Шевченка в північній його частині, житловими є вул. Л. Українки, Польова, Грушевського, Стуса, Ювілейна, Кринична, Жемчужна, Космічна та інші. В східній частині села головними є вул. Лісна та Ясна. В центральній частині села вул. Дніпровські пороги та Вишнева. В південно-західному напрямку головними вулицями є вул. Ярослава Мудрого, Олександрівська, Виноградна, житловими є вул. Степова, Будівельників та інші.

Інженерної інфраструктури за видами (водопостачання, водо відведення, газо -, електро -, теплопостачання).

Водопостачання.

Існуюче положення.

Джерело водопостачання с. Володимирівське є поверхневі води р. Дніпро. Водопостачання міста здійснюється централізованим комунальним водопроводом і локальними системами підприємств і організацій.

Головні споруди (водозабори, станції очищення та знезараження води) розташовані правому березі Дніпра в північній частині міста вище зредлі. Джерело водопостачання та головні споруди забезпечені нормативними зонами санітарної охорони.

ДВС-2 забезпечує питною водою с. Володимирівське та правобережну частину міста Запоріжжя, та інші населені пункти громад Запорізького району.

Проектні пропозиції

Генеральним планом пропонується вдосконалення водопровідних мереж для забезпечення питною водою всіх мешканців населеного пункту. Водопровідна мережа закріплюється. На ділянках нового будівництва прокладаються нові водопровідні об'єкти.

Норми господарсько-побутового питного водопостачання та коефіцієнти, добової нерівномірності споживання води прийняті у відповідності до ДБН В.2.5-74:2013. Витрати питної води на благоустрій території прийняті у відповідності з додатком «А» зазначеного ДБН.

Розрахункові витрати води на господарсько-побутові потреби населення зазначені в таблиці. Для повного забезпечення

Погоджено					
Зам. Інв. №					
Підпис і дата					
Інв. № об.					


Зм.	Кіл.	Арк.	№ док.	Підпис	Дата	12.23	1/23-ПЗ	Аркуш
-----	------	------	--------	--------	------	-------	---------	-------

селища водою питної якості необхідно будівництво кільцевих водопровідних мереж.

Проектом передбачено здійснити ввід водогінної мережі в усі житлові будинки, а також в будівлі і споруди громадського і культурно-побутового та іншого призначення.

З водопровідної мережі питна вода буде подаватись на господарсько-питні потреби населення, об'єкти громадсько-культурного і побутового призначення, а також на виробничі потреби сільськогосподарських підприємств, яким за технологією виробництва необхідна вода питної якості. Для економії енергетичних ресурсів та скорочення невиробничих витрат води генеральним планом передбачена обладнання всіх споживачів приладами обліку. Норми водоспоживання на господарсько-питні потреби населення, пожежогасіння, полив зелених насаджень і вулиць прийняті у відповідності з ДБН Б.2.2-12:2019 та ДБН В.2.5-74:2013.

Погоджено									
Інв. № об.	Підпис і дата		Зам. Інв. №						
Зм.	Кіл.	Арк.	№ док.	Підпис	Дата	1/23-ПЗ			
						Аркуш			

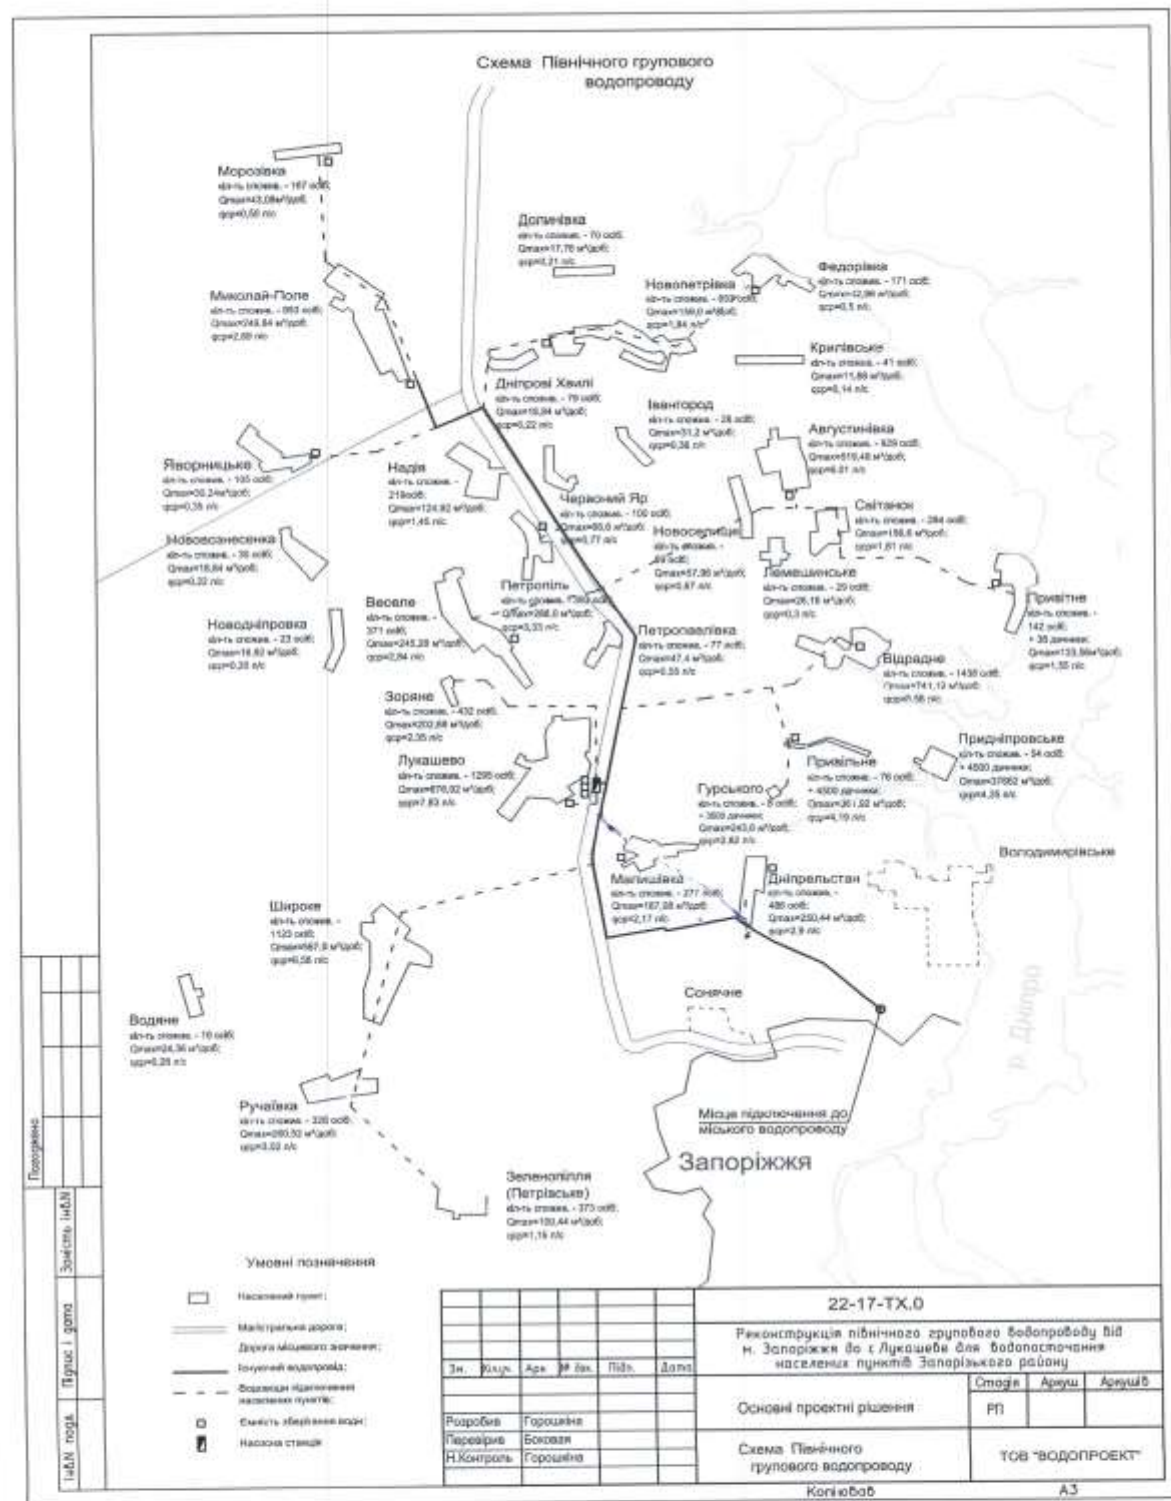

Погоджено

Зам. Інв. №

Підпис і дата

Інв. № об.

Зм.	Кіл.	Арк.	№ док.	Підпис	Дата
					12.23

1/23-ПЗ

Аркуш

Розрахунок водопостачання села Володимирівське (градпрогноз)

№ поз.	Найменування	Од. виміру	Норма водоспоживання, л/добу	Розрахунковий строк (15-20р.)	
				Кількість, осіб	Витрата, л/добу
1	2	3	4	7	8
1	Садибна забудова будинками, обладнаними внутрішнім водопроводом та каналізацією з ваннами і місцевими водопідігрівачами	осіб	230	9800	2231000
4	Дитячий садок	осіб	21	303	6363
5	Спортивний клуб	осіб	100	20	2000
6	Культові споруди	осіб	10	50	500
7	Адміністративні будинки	осіб	12	20	24
8	Амбулаторія	осіб	13	25	325
9	Будинок культури, ЦНАП	осіб	8	200	1600
10	Крамниці	осіб	250	10	2500
11	Кафе	страви	16	10	160
12	Виробничі потреби	осіб	25	40	1000
13	Виробничі потреби з урахуванням 20% на невраховані технологічні витрати				1.2
	Всього				163889

Тобто кількість води потребується по розрахунку близько 165 м3. Потужність існуючих мереж задовольняє потреби.

На наступних стадіях проектування необхідно уточнення прийнятих проектних пропозицій.

Водогони та мережі господарсько-питного водопроводу прокладаються на глибині 1,50 - 1,80м від поверхні землі і передбачаються з поліетиленових труб типу ПЕ-100 (питні) за ГОСТ 18599-83.

На кільцевих водопровідних мережах села встановлюються пожежні гідранти - 125мм за ГОСТ 8220-85. Відстань між пожежними гідрантами не перевищує 150м.

Водопровідні колодязі в проекті приймаються із збірних залізобетонних елементів за ТПР 901-09-11.84.

На наступних стадіях проектування необхідно уточнення прийнятих проектних пропозицій.

Зам. Інв. №

Підпис і дата

Інв. № об.

Зм.	Кіл.	Арк.	№ док.	Підпис	Дата
-----	------	------	--------	--------	------

1/23-ПЗ

Аркуш

Зони санітарної охорони

Згідно з ДБН В.2.5-74:2013 для забезпечення санітарно-епідеміологічної безпеки та охорони від забруднення джерел і водопровідних споруд системи централізованого питного водопостачання передбачається створення зон санітарної охорони.

Для водоводів ширина санітарно-захисної смуги при прокладанні в сухих ґрунтах не менше ніж 10 метрів при умовному діаметрі до 1000 мм, в мокрих ґрунтах – не менше ніж 50 метрів.

В генеральному плані використані існуючі обмеження – зони санітарної охорони м. Запоріжжя.

Протипожежні заходи

Для забезпечення пожежної безпеки с. Володимирівське передбачається виконання переліку заходів щодо організації зовнішнього пожежогасіння.

Розрахункова витрата води на зовнішнє пожежогасіння (згідно ДБН В.2.5-74:2013) з населенням більш однієї тисячі осіб та поверховості забудови до двох поверхів дорівнює 10 л/с, розрахункова кількість одночасних пожеж – 1, тривалість пожежі – 3 години.

Необхідний протипожежний запас води становитиме:

$$10 \text{ л/с} \times 670 \text{ с} \times 3 \text{ години} \times 0,001 \text{ м}^3 = 20 \text{ м}^3.$$

Таким чином, загальна витрата води на пожежогасіння села Володимирівське складе 20,0 м³.

Пожежне депо існуюче в с. Широке та заплановане в с. Відрадне Широківської сільської ради, Запорізького району..

Зовнішнє пожежогасіння території села передбачається від пожежних гідрантів установлених на кільцевих водопровідних мережах на відстані не більше 150 метрів один від одного (п.12.12. ДБН Б. 2.4-1-94). У місцях розташування пожежних гідрантів на опорах ЛЕП 0,4 кВт встановлюються світлові показники «ПГ», згідно з ГОСТ 12.04.009-83. Конкретні місця розташування пожежних гідрантів і світлових показників «ПГ» вирішується на подальшій стадії проектування (стадія «Проект» в «Робоча документація»).

Каналізація.

Існуюче положення.

Централізована каналізація в селі Володимирівське частково відсутня. Населення користується вигрібними ямами та септиками для збору побутових стічних вод.

Адміністративні об'єкти та комунальні заклади і підприємства користуються септиками.

Погоджено			
Інв. № об.	Підпис і дата	Зам. Інв. №	

Зм.	Кіл.	Арк.	№ док.	Підпис	Дата	1/23-ПЗ	Аркуш

Проектні пропозиції.

Проектом передбачається здійснення каналізування усіх житлових будинків, нової та існуючої забудови в тому числі об'єктів сільськогосподарського призначення та виробничих об'єктів.

Очисні споруди правобережжя ЦОС-2 розташовані за межами міста Запоріжжя, нижче за течією Дніпра, нормативна санітарно-захисна зона забудови забезпечена. Продуктивність їх відповідає об'єму надходження стічних вод.

Кількість стічних вод від житлової забудови села визначається відповідно до чисельності населення, характеру забудови та норм водовідведення згідно з ДБН В.2.5-75:2013.

Каналізаційна мережа запроектована самотливна з пластмасових (поліпропіленових) труб: самотливних – діаметрами 150 – 400 мм, до південно-західної околиці села. Далі стоки подаються каналізаційною насосною станцією через напірний колектор на очисні споруди.

Сумарна потужність сільських очисних споруд 0,160 тис.м³/добу, санітарно захисна зона 150 м згідно з додатком п. 12 ДСП 173-96.

Розрахунок водовідведення села Володимирівське (зрадпрогноз) становитиме 90% від об'єму водопостачання тобто 0,16 тис.м³/добу $0,9 = 0,144$ тис.м³/добу.

На наступних стадіях проектування необхідно уточнення прийнятих проектних пропозицій.

Газопостачання:

Існуюче положення:

На сьогоднішній день газопостачання Запорізького району та м. Запоріжжя на базі використання природного газу здійснюється відводами від магістрального газопроводу Шеделінка – Дніпро – Кривий Ріг – Ізмаїл через ГРС – 1,2,3 розташованих відповідно з північно-східного боку, з заходу та півдня міста, через ГРП (ШРП) та систему розподільчих газопроводів високого I та II категорії (1,2 МПа, 0,6 МПа), середнього (0,3 МПа) та низького (0,005 МПа) тисків.

Наразі, в селі Володимирівське газопостачання існує по території всього села.

Проектні пропозиції:

Проектом передбачено забезпечення газопостачанням від існуючих мереж всіх об'єктів житлового, громадського, виробничого та сільськогосподарського призначення.

Погоджено			
Зам. Інв. №			
Підпис і дата			
Інв. № об.			

Зм.	Кіл.	Арк.	№ док.	Підпис	Дата	12.23	1/23-ПЗ	Аркуш
-----	------	------	--------	--------	------	-------	---------	-------

Електропостачання.

Існуюче положення

На території села Володимирівське функціонує система електропостачання, проте потрібні капіталовкладення для його реконструкції, ремонту та модернізації.

Проектні пропозиції

Даним проектом передбачено джерело електропостачання залишити без змін, з виконанням його реконструкції та збільшенням потужності. Необхідно забезпечити електричними мережами проєктовану житлову та громадську забудову, підприємства.

Проектні рішення передбачають збільшення споживаної потужності. Пропонується передбачити встановлення додаткових трансформаторних підстанцій для проєктованих об'єктів.

Для забезпечення електроенергією споживачів села передбачається збудувати необхідну кількість трансформаторних підстанцій. Кількість, розміщення ТП і траси ліній електропередачі вирішуються під час подальшого проєктування згідно з Технічними умовами енергопостачальної компанії.

Внутрішні електромережі будівель і споруд передбачається виконувати за типовими і індивідуальними проектами.

Облік споживаної електроенергії індивідуальних житлових приватних будівель передбачається здійснювати електронними лічильниками, встановленими у вологозахисних щитах (IP54) на зовнішніх стінах будинків.

Облік споживаної електроенергії в громадських будівлях і комунальних спорудах передбачається виконувати електронними лічильниками, встановленими у ВРУ.

Мережі зовнішнього освітлення пропонується виконати самонесучим ізольованим проводом на опорах мережі 0,4 кВ та кабельними лініями. Як варіант зовнішнє освітлення може бути виконано автономними світильниками з сонячними батареями.

Світильники пропонуються типу ЖКУ-250 і РТУ-125 на металевих опорах.

Управління зовнішнім освітленням здійснюється автоматично від щитів низької напруги існуючих і проєктованих ТП. Основні положення, прийняті в розробленому проєкті, повинні бути прийняті за основу під час виконання робочих креслень електропостачання села.

Погоджено		
Інв. № об.	Зам. Інв. №	
	Підпис і дата	

					12.23	1/23-ПЗ	Аркуш
Зм.	Кіл.	Арк.	№ док.	Підпис	Дата		

Вивезення сміття здійснюється у місця, відведені та погоджені з відповідними органами санітарно-епідеміологічної служби та органами охорони навколишнього середовища.

Базовим підприємством із перероблення та захоронення ТПВ буде полігон №3 площею 18,0 га в межах Широківської сільради, що відповідає рішенням Схеми планування території Запорізької області.

Дощової каналізації, інженерної підготовки та захисту території.

Генеральним планом надані принципові рішення, які стосуються організації відведення дощових та талих вод, вертикальному плануванню та водовідведенню на території населеного пункту.

Генеральним планом передбачена дощова каналізація з подальшим підключенням до мереж дощової каналізації м. Запоріжжя.

В місті існує роздільна система каналізації. Проте існуюча міська мережа дощових колекторів не забезпечує нормативний відвід поверхневого стоку з міських територій. Стан зливової каналізації на сьогоднішній день укр. незадовільний. Очисні споруди дощової каналізації відсутні. Випуски неочищених стоків здійснюються в річку Дніпро, Суха та Мокра Московки, балка Капустяна, у стічні канаби, в балки, на поверхню землі за рельєфом. Скид в річки неочищених стоків дощової каналізації та неорганізованого стоку поверхневих вод з забудованих територій, вулиць та проїздів приводить до інтенсивного замулення русел річок та водойм, а також до їх забруднення шкідливими речовинами від осідання викидів промислових підприємств, витоків паливно-мастильних речовин, вимивання речовин руйнування дорожнього покриття.

Згідно схеми дощових колекторів, розробленої при інвентаризації водостоків та дренажів м. Запоріжжя, яка проводилась в 1981-1983 рр., в місті існує достатньо розгалужена мережа дощової каналізації. Усього в місті нараховується близько 185 км дощової каналізації та більше 130 випусків (у тому числі локальних) неочищеного поверхневого стоку.

Всі існуючі випуски дощової каналізації підключаються в проектну та існуючу мережу дощової каналізації, з подальшим випуском до проектних очисних споруд міста.

Для території комунально-складських зон, промислових, автотранспортних підприємств, ринків, автостоянок, автозаправних станцій, гаражів, смітників та інших джерел забруднення, необхідно створити локальні відомчі системи водовідведення та очищення поверхневих і дощових вод різного ступеня складності в залежності від особливостей функціонального використання території, їх масштабів, з максимальною можливістю оборотного використання очищених стоків. В разі неможливості оборотного використання стоків для виробничих потреб або поливу території, попередньо очищені поверхневі води скидаються до міської дощової каналізації з подальшим доочищенням на очисних спорудах.

Погоджено					
Інв. № об.	Зам. Інв. №				
	Підпис і дата				

					12.23	1/23-ПЗ	Аркуш
Зм.	Кіл.	Арк.	№ док.	Підпис	Дата		

Генпланом розроблені тільки принципові рішення по відводу дощових і поверхневих вод з території житлової забудови та вулиць. При подальшому проектуванні необхідно доручити спеціалізованій організації розробити проект дощової каналізації с. Володимирівське, з визначенням типу очисних споруд та методів очищення поверхневого стоку. Розроблена схема дощової каналізації підтверджує можливість здійснення планувального вирішення території, потребує уточнення і береться за основу на наступних стадіях проектування

-виконувати вертикальне планування ділянки забудови, якісно заповнювати пазики котлованів та траншей;

-при улаштуванні водо акумулюючи споруд і водо несучих комунікацій виключити витікання води;

-підвищенням міцності і загальної просторової жорсткості споруд, збільшенням їх піддатливості за допомогою гнучких та розрізних конструкцій, улаштуванням пристосування для вирівнювання конструкцій, а також використанням методів, що забезпечують нормальну роботу обладнання при деформаціях основи.

Погоджено		

Інв. № об. Підпис і дата Зам. Інв. №

Зм.	Кіл.	Арк.	№ док.	Підпис	Дата	12.23	1/23-ПЗ	Аркуш

Основні показники генерального плану населеного пункту

Ч. ч.	Назва показника	Одиниця виміру	Існуючий стан в старих межах	Існуючий стан в нових межах	Розрахунковий етап 15-20 років
1.	Населення	осіб	3165	7350	9800
2.	Територія в межах населеного пункту, всього:	га	499,48	924,40	924,40
	Житлової садибної забудови	»	277,98	344,07	591,19
	Житлової багатоквартирної забудови		1,10	1,10	22,60
	Громадські забудови	»	4,34	8,55	32,45
	Транспортної інфраструктури	»	0,20	4,57	13,71
	Виробнича територія	»	1,40	11,84	11,84
	Територія кладовища	»	0,77	0,77	0,77
	Зелених насаджень спецпризначення	»	0,90	9,21	42,92
	Зелені насадження загального користування	«	20,88	93,38	104,63
	Сільськогосподарського призначення	«	174,67	366,05	27,28
	Інженерної інфраструктури		-	4,67	4,67
	Територія комунальна		-	-	2,23
	Територія під дорогами		17,20	52,91	70,11
3.	Житловий фонд				
	Садибна забудова	од	1614	-	3261
	Багатоквартирна забудова	од.	8	-	17
4.	Довжина доріг	п/м	35638	-	89004
5.	Інженерне забезпечення				
	Водопостачання	п/м	4607	-	49851
	Каналізація	п/м	9037	-	70361
	Повітряні лінії високої напруги	п/м	68917	-	68917
	Газопровід	п/м	28332	-	14481,75
6.	Санітарне очищення території				
	Обсяги твердих побутових відходів	кг/рік	949500	2205000	2940000

Погоджено

Зам. Інв. №

Підпис і дата

Інв. № об.