село Зеленопілля
Запорізького району, Запорізької області

План існуючого використання території.
Схема існуючих планувальних обмежень
М 1:2000

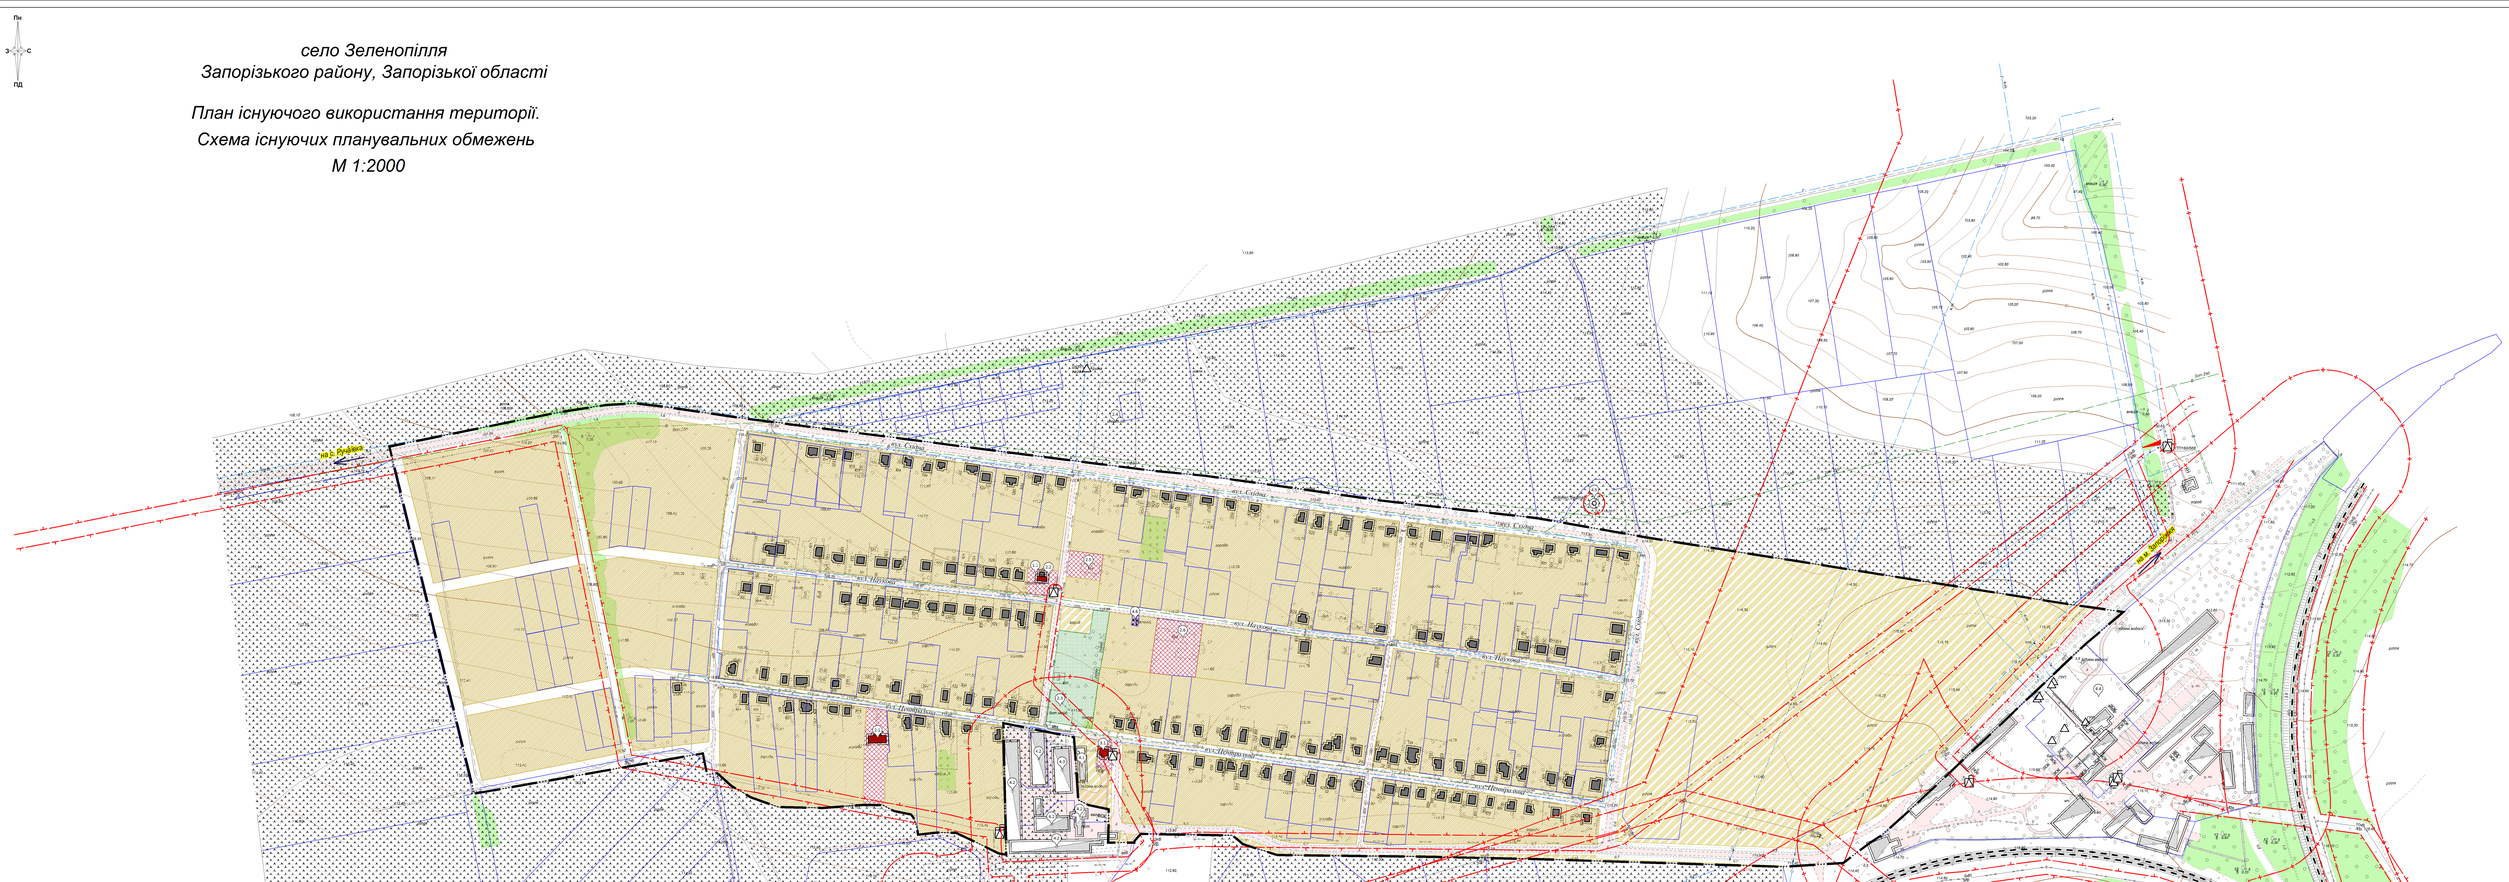

Експлікація будівель та споруд

№ п/п	Найменування	Примітка
1.	*Установи охорони здоров'я*	
1.1	*Фельдшерський пункту ЦПМСД Широківської сільської ради*	
2.	*Установи культури та мистецтва, культові споруди, фізкультурні та спортивні споруди, учбові заклади та дитячі установи*	
2.1	*Будівля клубу*	*зруйнован.*
2.2	*Бібліотека КУ "ЦКДСМСТ" Широківської сільської ради*	
2.3	*Торговий майданчик*	
2.4	*Спортивний майданчик*	*за меж. н.с.*
2.5	*Дитячий садок*	*зруйнован.*
2.6	*Школа*	*зруйнован.*
3.	*Підприємства торгівлі, громадського харчування та побутового обслуговування*	
3.1	*Крамниця змішаної торгівлі*	
4.	*Комунальні підприємства, склади, бази, інше*	
4.1	*Складська будівля*	
4.2	*Комплекс складських будівель СЗЗ 50 м.*	*за меж. н.с.*
4.3	*ТСК СЗЗ 100 м.*	
4.4	*Виробнича база ВАТ АК Південтрансгаз СЗЗ 100 м.*	*за меж. н.с.*
4.5	*Вежа Рожковського ЗСО 15 м.*	*за меж. н.с.*
4.6	*Вежа мобільного зв'язку*	

Умовні позначення

Існуючі	Проект	Найменування
		Межа населеного пункту
		Об'єкти Державного земельного кадастру
		Територія житлової садибної забудови
		Територія громадської забудови
		Територія сільськогосподарського призначення
		Територія зелених насаджень загального користування
		Територія інженерної інфраструктури
		Житловий будинок
		Громадська будівля
		Виробнича будівля та споруда
		Залізниця
		Особливо цінні землі (сільськогосподарські угіддя)
		Комплектна трансформаторна підстанція (КТП)
		Газорозподільний пункт (ГРП, ШРП)
		Водонапірна башта
		Охоронна зона
		Санітарно-захисна зона
		1-й пояс зони санітарної охорони

Примітка:

1. *Межі особливо цінних груп пунктів нанесені за матеріалами сайту - ЗАГАЛЬНОНАЦІОНАЛЬНА (ВСЕУКРАЇНСЬКА) НОРМАТИВНА ГРОШОВА ОЦІНКАЗЕМЕЛЬ СІЛЬСЬКОГОСПОДАРСЬКОГО ПРИЗНАЧЕННЯ доступному в режимі читання за посиланням https://rngo.land.gov.ua/ua/map/#*
2. *Територія біля села Зеленопілля відноситься до: природно-сільсько-господар-ської зони - СТЕПОВА природно-сільсько-господарської провінції - СТЕПОВА ЛІВОБЕРЕЖНА природно-сільсько-господарського округу - ДОНЕЦЬКО-ДНІПРОВСЬКИЙ*
3. *Повний перелік особливо цінних груп пунктів затверджено наказом Державним комітетом України по земельним ресурсам № 245 від 06.10. 2003 р.*

							2693-2018-ГП
							Генеральний план села Зеленопілля Запорізького району Запорізької області
							Основання з розширення меж населеного пункту та план зонування села Зеленопілля Запорізького району Запорізької області (у межах генерального плану)
Змін.	Кільк.	Арк.	№док.	Підп.	Дата	Замовник: Широківська сільська рада	Стадія: ГП; Аркуш: 2; Аркушів: 7
ГАП		Грубка				План існуючого використання території. Схема існуючих планувальних обмежень. М 1:2000	ФОП Грубка І.А.
Перевірив							
Коротун		Грубка					

Формат 1800 х 1200