


село Лукашеве
Запорізького району, Запорізької області

Схема інженерної підготовки та
захисту території
М 1:5000

Умовні позначення

Існуючі	Проект	Найменування
	—+—+—+—	Межа населеного пункту
		Об'єкти Державного земельного кадастру
		Територія житлової садибної забудови
		Територія житлової багатоквартирної забудови
		Територія сільськогосподарського призначення
		Територія громадської забудови
		Територія інженерної інфраструктури
		Територія комунальних об'єктів
		Територія виробнича
		Територія зелених насаджень загального користування
		Територія зелених насаджень спецпризначення
		Територія кладовища
		Водний об'єкт
		Житловий будинок
		Виробнича будівля (споруда)
		Громадська будівля
		Пройзд
		Червоні лінії
		Комплектна трансформаторна підстанція (КТП)
		Газорозподільний пункт (ГРП, ШРП)
		Водонапірна башта
		Пожарний резервуар
		Проектна відмітка. Натурна відмітка
		Напрямок ухилу в промілі. Відстань в метрах
		Лоток
		Розчищення водоєм та водосховищ

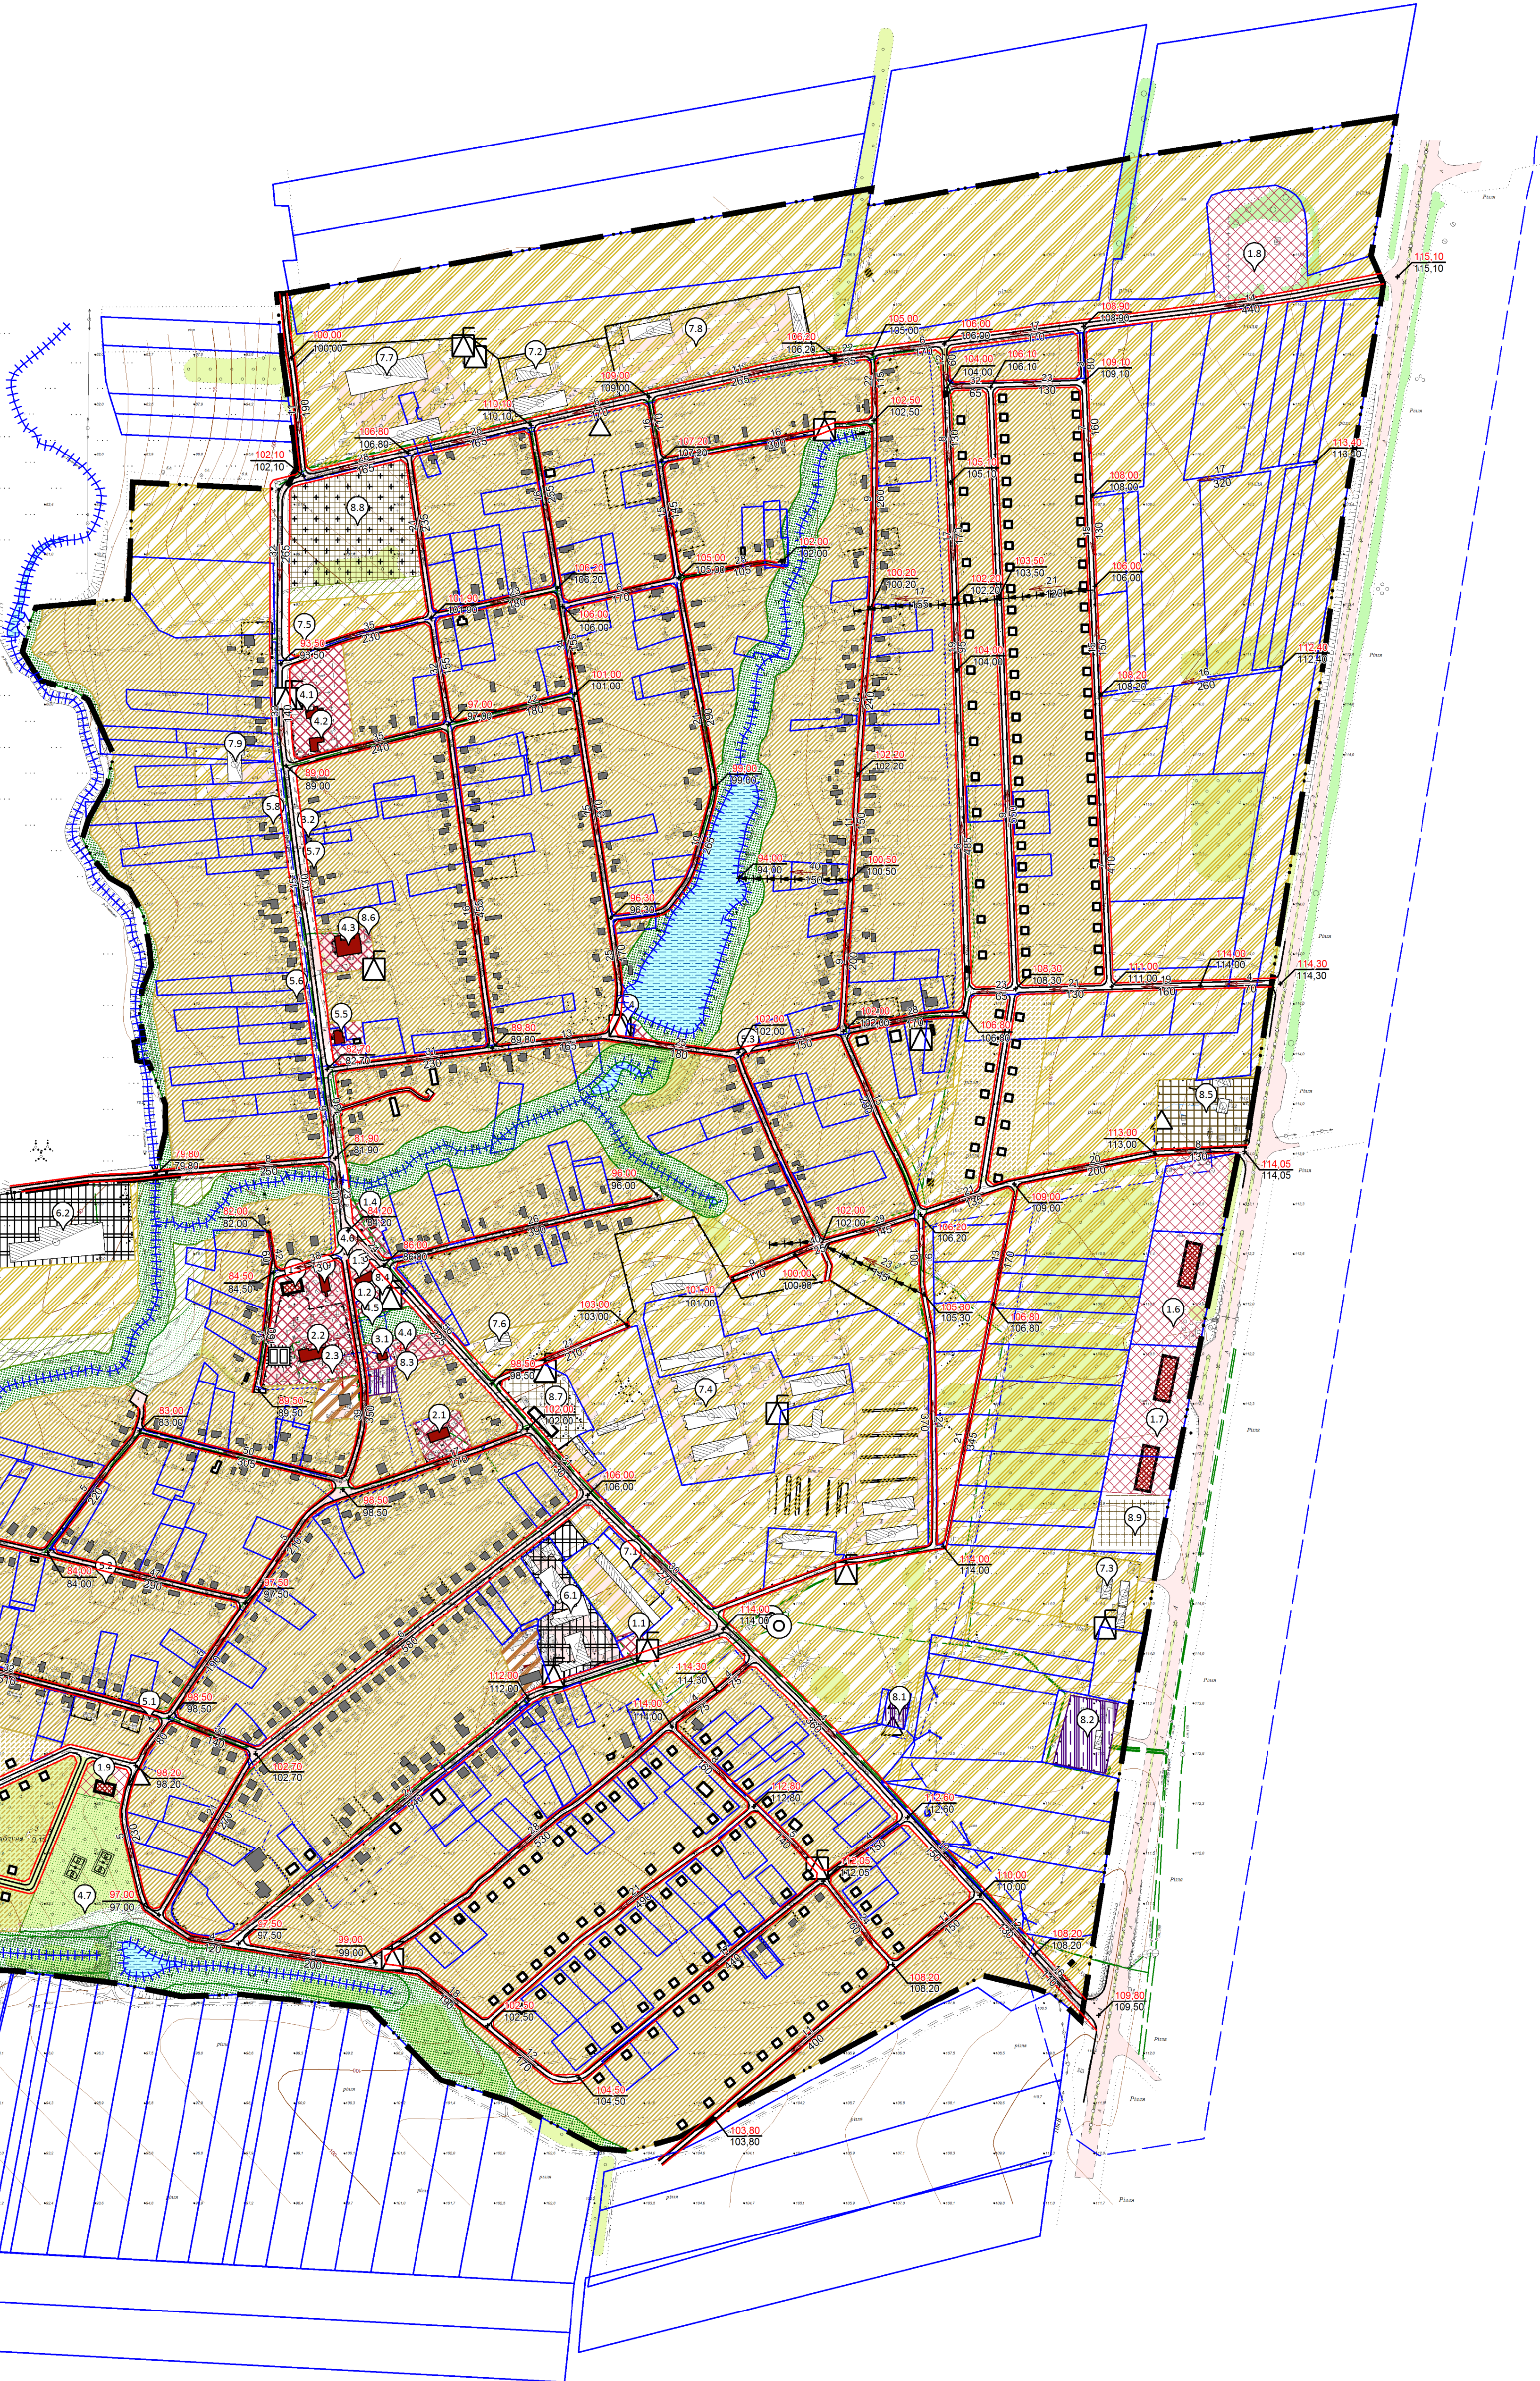

Експлікація будівель та споруд

№ п/п	Найменування	Примітка
1.	Адміністративні та громадські установи	
1.1	Адміністративна будівля Запорізького управління водного господарства	
1.2	Адміністративна будівля	
1.3	Адміністративна будівля	
1.4	Будівля побутового обслуговування населення	Проектн.
1.5	Відділення банку, пошти	Проектн.
1.6	Торгов. виставков. будівлі, логістичні центр	Проектн.
1.7	Готель, кафе	Проектн.
1.8	Ринок сільськогосподарської продукції	Проектн.
1.9	Спортивний зал	Проектн.
2.	Учбові заклади та дитячі установи	
2.1	Дитячий садок Лукашівський НВК	
2.2	Школа Лукашівський НВК	
2.3	Спортивний майданчик	Проектн.
3.	Установи охорони здоров'я	
3.1	ФАП, приміщення для реабілітації	Реконстр.
3.2	Стоматологія	
4.	Установи культури та мистецтва, культові споруди	
4.1	Церква	
4.2	Будівля недільної школи храму	
4.3	Будинок культури з бібліотекою	
4.4	Братська могила радянських воїнів та пам'ятник воїнам - односельчанам	
4.5	Сільський парк	
4.6	Пам'ятник Шевченку Т.Г.	
4.7	Парк з спортивним та дитячим майданчиком	Проектн.
5.	Підприємства торгівлі, громадського харчування та побутового обслуговування	
5.1	Торгівельний павільйон	
5.2	Крамниця змішаної торгівлі	
5.3	Крамниця	
5.4	Торгівельний павільйон з літнім майданчиком	
5.5	Крамниця змішаної торгівлі	
5.6	Крамниця змішаної торгівлі з кафе	
5.7	Крамниця промислових товарів, кафе	
5.8	Крамниця ветеринарних та зооповарів	
5.9	Об'єкт громадського харчування, туристичних послуг	
6.	Промислові підприємства	
6.1	Виробництво електротехнічної продукції ПП «Еліт» СЗЗ 50 м	
6.2	Цегельний завод СЗЗ 100 м	
7.	Сільськогосподарське підприємство	
7.1	Комплекс по зберіганню зерна СЗЗ 50 м	
7.2	Комплекс по зберіганню зерна, овочів СЗЗ 50 м	
7.3	Підприємство по переробці зерна СЗЗ 100 м	
7.4	Склади сільськогосподарської продукції СЗЗ 50 м	
7.5	Територія вирощування декоративних рослин	Проектн.
7.6	Склади зберігання зерна СЗЗ 50	
7.7	Підприємство по переробці зерна СЗЗ 100 м	
7.8	Підприємство по технічному обслуговуванню та ремонту сільськогосподарської техніки СЗЗ 100 м	
7.9	Сільськогосподарське підприємство з складом, ваговою та обслуговуванню сільськогосподарської техніки СЗЗ 100 м	
8.	Комунальні заклади, склади, бази, підприємства транспорту та зв'язку	
8.1	ГРП ОЗ 10 м	
8.2	Насосна ЗСО 15 м	
8.3	ЗТП ОЗ 3 м	
8.4	Газова котельня ОЗ 10 м	
8.5	Господарські будівлі служби автомобільних доріг СЗЗ 100 м	
8.6	Вишка мобільного зв'язку	
8.7	Будівельний двір з виготовлення металевих конструкцій СЗЗ 50 м	Проектн.
8.8	Кладовище СЗЗ 100 м.	
8.9	АЗС, АГЗП СЗЗ 100 м.	Проектн.

						1407-2017
						Генеральний план, План зонування території села Лукашеве Запорізького району Запорізької області.
Змін.	Київ.	Арх.	№ док.	Підп.	Дата	
						Замовник: Широкивська сільська рада
						Стадія
						Арх.
						6
						7
ГАП	Пруда					Схема інженерної підготовки та захисту території М 1:5000
Перевірив	Пруда					ФОРМ 1015 к 750
Розробив	Пруда					