село Зеленопілля
Запорізького району, Запорізької області

План зонування території
М 1:2000

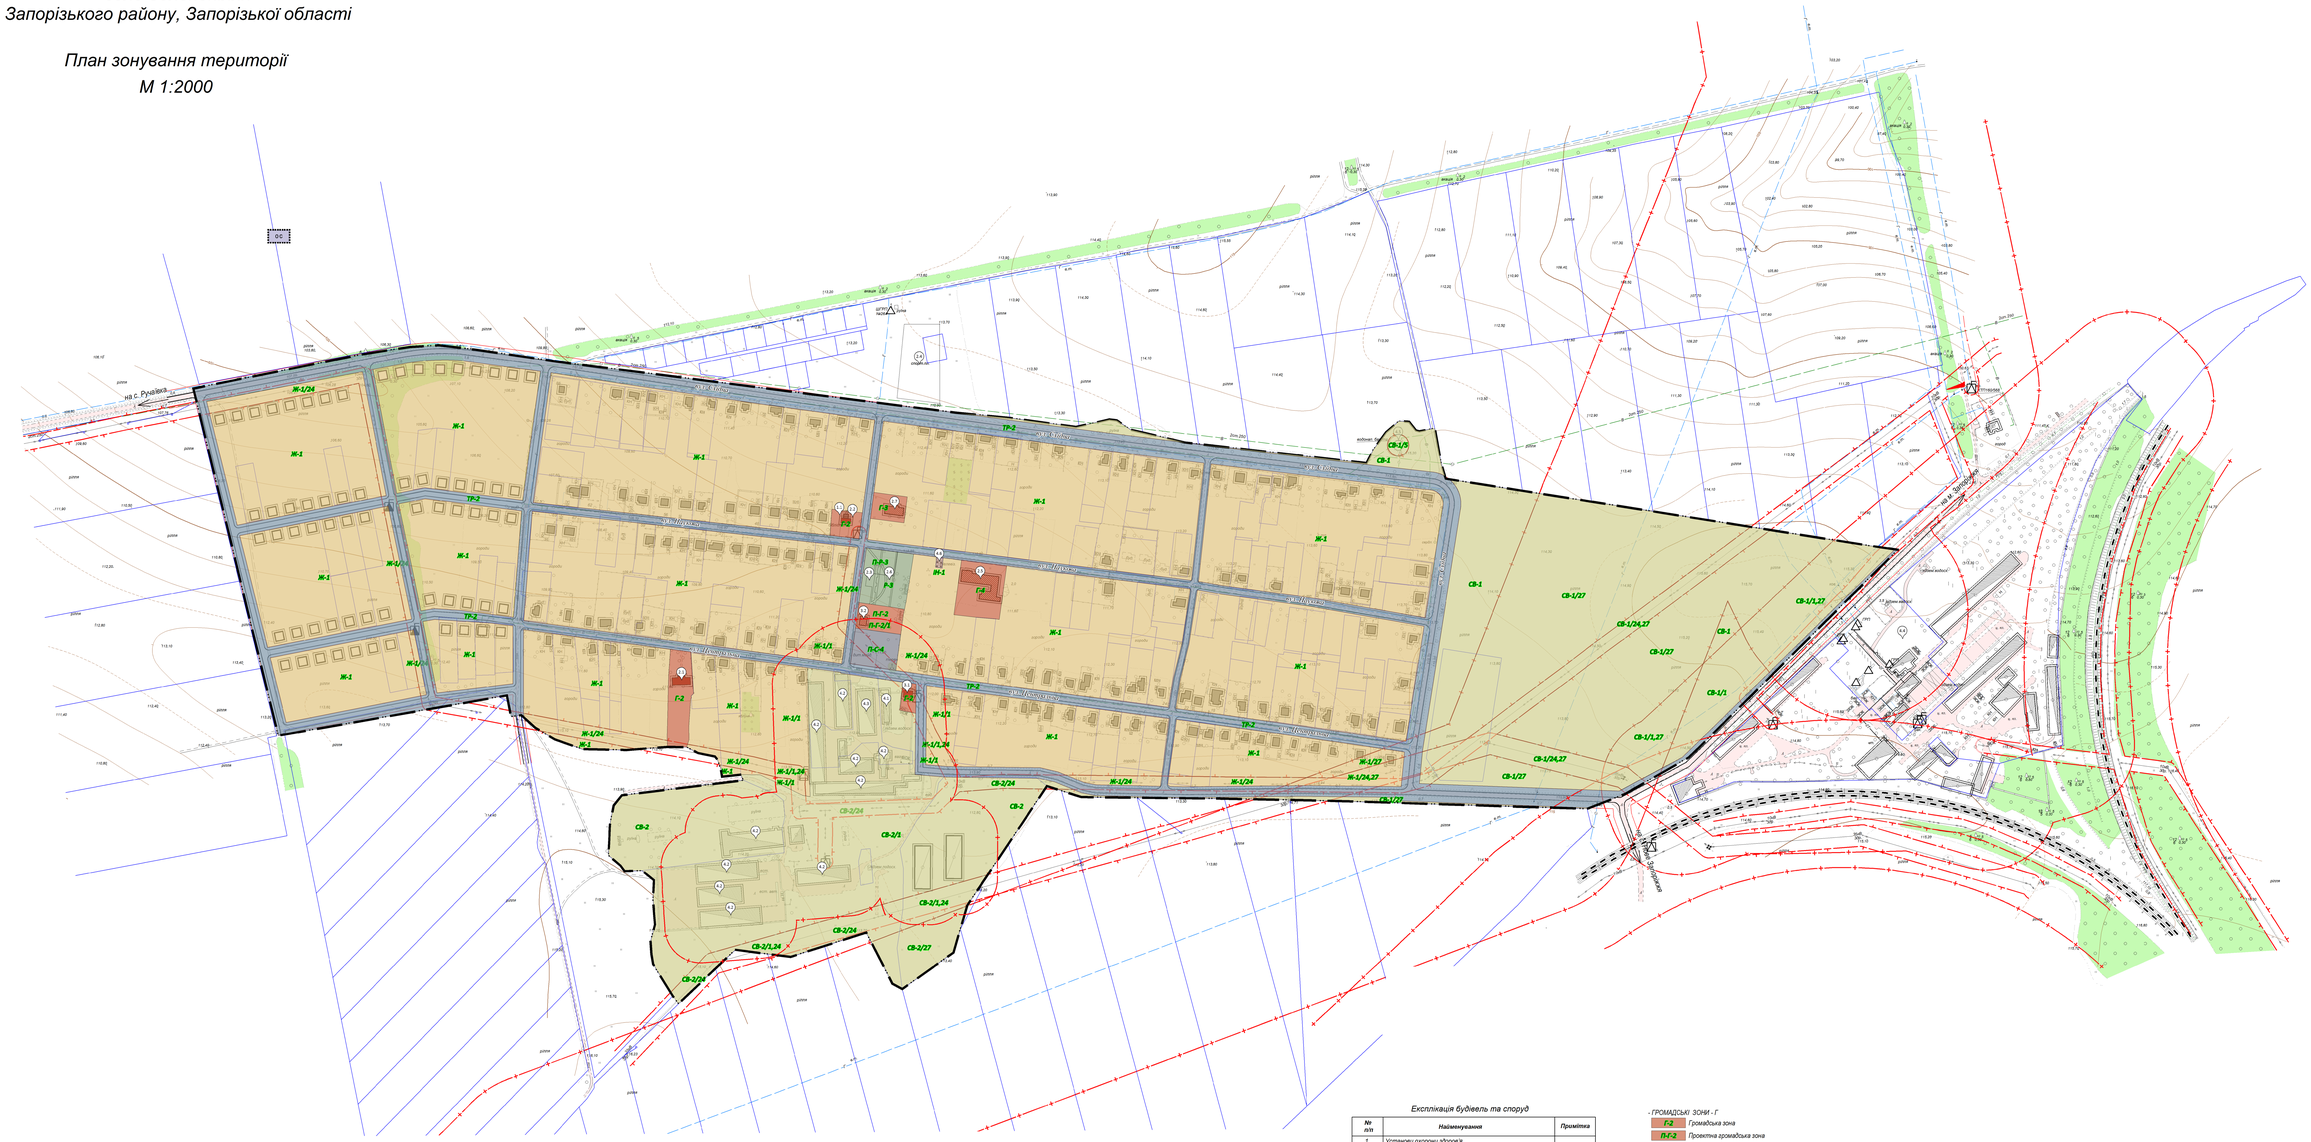

Експлікація будівель та споруд

№ п/п	Найменування	Примітка
1.	*Установи охорони здоров'я*	
1.1	*Фельдшерський пункту ЦПМСД Широківської сільської ради*	
2.	*Установи культури та мистецтва, культові споруди, фізкультурно та спортивні споруди, учбові заклади та дитячі установи*	
2.1	*Центр дозвілля*	*проект.*
2.2	*Бібліотека КУ "ЦКДСМСТ" Широківської сільської ради*	
2.3	*Ігровий майданчик*	*проект.*
2.4	*Спортивний майданчик*	*за межі н.с.*
2.5	*Спортивний комплекс з адмін. приміщеннями*	*проект.*
2.6	*Парк*	*проект.*
2.7	*Дитячий садок на 50 місць*	*проект.*
3.	*Підприємства торгівлі, громадського харчування та побутового обслуговування*	
3.1	*Крамниця змішаної торгівлі*	
3.2	*Крамниця продовольчих та не продовольчих товарів*	*проект.*
4.	*Комунальні підприємства, склади, бази, інше*	
4.1	*Складська будівля*	
4.2	*Комплекс складських будівель СЗЗ 50 м.*	
4.3	*ТОК СЗЗ 100 м*	
4.4	*Виробнича база ВАТ АК Південтрансенерго СЗЗ 100 м*	*за межі н.с.*
4.5	*Вежа Рожковського ЗСО 15 м.*	
4.6	*Вежа мобільного зв'язку*	

- ГРОМАДСЬКІ ЗОНИ - Г

- **Г-2** *Громадська зона*
- **П-Г-2** *Проектна громадська зона*
- **П-Г-2/1** *Проектна громадська зона в санітарно-захисній зоні промислових підприємств I-V класу шкідливості, сільськогосподарських, комунальних, складських територій*
- **Г-3** *Навчальна зона*
- **Г-4** *Культурна та спортивна зона*

- ЖИТЛОВІ ЗОНИ - Ж

- **Ж-1** *Зона садибної забудови*
- **Ж-1/1** *Зона садибної забудови в санітарно-захисній зоні промислових підприємств I-V класу шкідливості, сільськогосподарських, комунальних, складських територій*
- **Ж-1/24** *Зона садибної забудови в охоронній зоні магістральних електромереж та об'єктів на них*
- **Ж-1/27** *Зона садибної забудови в охоронній зоні газо-, нафто- та продуктопроводів, а також об'єктів на них*

- ЛАНДШАФТНО-РЕКРЕАЦІЙНІ ЗОНИ - Р

- **Р-3** *Рекреаційна зона озеленених територій загального користування*
- **П-Р-3** *Проектна рекреаційна зона озеленених територій загального користування*

- ЗОНИ ТРАНСПОРТНОЇ ІНФРАСТРУКТУРИ - ТР

- **ТР-2** *Зона транспортної інфраструктури*

- ЗОНИ ІНЖЕНЕРНОЇ ІНФРАСТРУКТУРИ - ІН

- **ІН-1** *Зона інженерної інфраструктури*

- ЗОНИ ЗЕМЕЛЬ СІЛЬСЬКОГОСПОДАРСЬКОГО ПРИЗНАЧЕННЯ - СВ

- **СВ-1** *Зона земель сільськогосподарського призначення*
- **СВ-1/1** *Зона земель сільськогосподарського призначення в санітарно-захисній зоні промислових підприємств I-V класу шкідливості, сільськогосподарських, комунальних, складських територій*
- **СВ-1/5** *Зона земель сільськогосподарського призначення в зоні санітарної охорони споруд та мереж водопостачання*
- **СВ-1/24** *Зона земель сільськогосподарського призначення в охоронній зоні магістральних електромереж та об'єктів на них*
- **СВ-1/27** *Зона земель сільськогосподарського призначення в охоронній зоні газо-, нафто- та продуктопроводів, а також об'єктів на них*
- **СВ-2** *Зона сільськогосподарських підприємств, установ та організацій*
- **СВ-2/1** *Зона сільськогосподарських підприємств, установ та організацій в санітарно-захисній зоні промислових підприємств I-V класу шкідливості, сільськогосподарських, комунальних, складських територій*
- **СВ-2/24** *Зона сільськогосподарських підприємств, установ та організацій в охоронній зоні магістральних електромереж та об'єктів на них*
- **СВ-2/27** *Зона сільськогосподарських підприємств, установ та організацій в охоронній зоні газо-, нафто- та продуктопроводів, а також об'єктів на них*

- СПЕЦІАЛЬНІ ЗОНИ - С

- **П-С-4** *Проектна зона озеленення спеціального призначення*

									2803-2019-ГП
									Генеральний план села Зеленопілля Запорізького району Запорізької області
									Оновлення з розширенням меж населеного пункту та план зонування села Зеленопілля Запорізького району Запорізької області (у складі генерального плану)
Змін.	Кільк.	Арк.	№док.	Підп.	Дата	Замовник: Широківська сільська рада		Стадія	Аркуш	Аркушів
								ГП	7	7
ГАП		Грубка				План зонування території М 1:2000		ФОП Грубка І.А.		
Перевірив										
Розробив		Грубка								

Формат 1800 х 1200