

ФО – П Прудка І. А.

69039 м. Запоріжжя, пров. Вантажний, буд. 13
email: 2136006@ ukr.net.

Замовник:

Широківська сільська рада Запорізького району
Запорізької області

Генеральний план селища Сонячне Запорізького району
Запорізької області. Оновлення з розширенням меж населеного
пункту та План зонування селища Сонячне Запорізького району
Запорізької області(у складі Генерального плану)

Пояснювальна записка генерального плану

Шифр: 117/2017-ПЗ

ТОМ 1

Фізична особа підприємець _____ І. А. Прудка

Головний архітектор проекту _____ І. А. Прудка

2018 р.

Погоджено		

Зам. Інв. №

Підпис і дата

Інв. № об.

												2											
Позначення						Найменування						Примітка											
117/2017-З						Зміст																	
117/2017-СУ						Склад проекту																	
117/2017-ПД						Підтвердження ГАП																	
117/2017-ВУ						Відомості про учасників проектування																	
117/2017-ПЗ						Пояснювальна записка																	
						Розділ 1. Вступ.																	
						Розділ 2. Аналітична частина																	
						2.1. Географічне розташування населеного пункту, його адміністративний статус, відомості про площу території та численність населення, місце в системі розселення.																	
						2.2. Оцінка реалізації попереднього генерального плану, характеристика стану території населеного пункту та проблем її використання.																	
						2.3. Аналіз зовнішніх та внутрішніх факторів, що визначають конкурентні переваги та обмеження розвитку населеного пункту.																	
						2.4. Характеристика структури та обсягів існуючого житлового фонду, об'єктів обслуговування, перелік об'єктів господарського комплексу, інженерно-транспортної інфраструктури, інженерної підготовки та благоустрою, захисту території від небезпечних природних і техногенних процесів.																	
						2.5. Аналіз відомостей про стан навколишнього середовища.																	
						2.6. Аналіз ресурсного потенціалу, тенденцій розвитку населеного пункту та прилеглих територій.																	
						Розділ 3. Обґрунтування та пропозиції.																	
						3.1. Основні пріоритети та цільові показники соціального і демографічного розвитку території з метою формування повноцінного життєвого середовища																	
						117/2017-З																	
Зм.		Кільк.		Арк.		№ док		Підпис		Дата		Зміст			Стадія		Аркуш		Аркушів				
Розробив				Прудка						05.18					ДПТ		1		1				
Перевірив																							
ГАП				Прудка						05.18													
																		ФО-П Прудка І. А.					

Погоджено

Зам. Інв. №

Підпис і дата

Інв. № об.

		4
	• Системи громадських центрів	
	• Соціальної інфраструктури державної та комунальної власності	
	• Озелених територій загального користування, ландшафтно – рекреаційних територій населеного пункту	
	• Вулично – дорожньої мережі за її категоріями з виділенням ділянок нового будівництва та реконструкції, будівництва мостів	
	• Інженерної інфраструктури за видами (водопостачання, водо відведення, газо -, електро -, тепlopостачання)	
	• Мережі розташування об'єктів і місць утилізації побутових відходів, а також місць захоронення тварин	
	• Дощової каналізації, інженерної підготовки та захисту території	
	• Основні показники генерального плану	
	Розділ 4. Додатки	

Погоджено			

[illegible]

												5								
№ пом у		Позначення				Найменування				Примітки										
						Текстові матеріали														
1.		117/2017-ПЗ				Пояснювальна записка до генерального плану														
2.		117/2017-ПЗ				Основні положення генерального плану														
3.		117/2017-ПЗ				Пояснювальна записка до плану зонування території														
4.						Графічні матеріали														
		Лист 1				Схема розташування населеного пункту в системі розселення (у довільному масштабі) М 1:25000														
		Лист 2				План існуючого використання території М 1:5000.														
		Лист 3				Схема існуючих планувальних обмежень М 1:5000.														
		Лист 4				Генеральний план (основне креслення) М 1:5000.														
		Лист 5				Схема проектних планувальних обмежень М 1:5000.														
		Лист 6				Схема вулично – дорожньої мережі, міського (сільського) та зовнішнього транспорту М 1:5000														
		Лист 7				Схема інженерного обладнання території М 1:5000														
		Лист 8				Схема інженерної підготовки та захисту території М 1:5000														
		Лист 9				План зонування території М1:5000														
						Інженерно-технічні заходи цивільного захисту (цивільної оборони)				У вигляді окремих томів										
Погоджено Зам. Інв. № Підпис і дата Інв. № об.												117/2017-СП								
												Зм. Кільк. Арк. № док Підпис Дата						Стадія Аркуш Аркушів		
												Розробив Прудка						ДТП 1 1		
												Перевірив								
												ГАП Прудка								
																		ФО-П Прудка І. А.		

Склад проекту

Генеральний план, план зонування території селища Сонячне Широківської сільської ради Запорізького району Запорізької області. Оновлення з розширенням меж населеного пункту виконано згідно з вимогами ДБН Б.1.1-15:2012 "Склад та зміст генерального плану населеного пункту", ДСТУ-Н Б Б.1.1-12:2011 «Настанова про склад та зміст плану зонування території (зонінг)», ДБН 360-92** «Містобудування. Планування і забудова міських і сільських поселень», екологічних, санітарно-гігієнічних та протипожежних норм, що діють на території України, а також Закону України «Про містобудівну діяльність».

Головний архітектор проекту

І. А. Прудка

Кваліфікаційний сертифікат відповідального виконавця окремих видів робіт (послуг), пов'язаних із створенням об'єкта архітектури (розроблення містобудівної документації) Серія АА №003280

Погоджено												
Інв. № об.	Підпис і дата	Зам. Інв. №							117/2017-ПД			
			Зм.	Кільк.	Арк.	№ док.	Підпис	Дата	Підтвердження ГАП	Стадія	Аркуш	Аркушів
			Розробив	Прудка			05.18	ДТП		1	1	
			Перевірив									
			ГАП	Прудка			05.18	ФО-П Прудка І. А.				

						117/2017-ВУ			
						Відомості про учасників проектування	Стадія	Аркуш	Аркушів
Зм.	Кільк.	Арк.	№ док	Підпис	Дата		ДТП	1	1
Розробив		Прудка			05.18				
Перевірив									
ГАП		Прудка			05.18				
						ФО-П Прудка І. А.			

Погоджено			

Πίθνυς ἰ δαμα

ИВБ. № 08.

Πίθνυς i θαλα

РОЗДІЛ 1. ВСТУП

Замовником Генерального плану та плану зонування території є Широківська сільська рада Запорізького району Запорізької області.

Виконавцем Генерального плану та плану зонування є:

Фізична особа підприємець Прудка І. А.

69039, м. Запоріжжя, пров. Вантажний, 13.

ІНН 2803210762, м. Запоріжжя, ЗРУ «ПРИВАТБАНК», МФО 313399, р/р 26005060729170, платник єдиного податку

Головний архітектор проекту – І. А. Прудка, кваліфікаційний сертифікат Серія АА № 003280 (розроблення містобудівної документації).

Геодезична зйомка території надана Замовником у складі вихідних даних та надана розробнику в 2017 р., для виконання генерального плану. Що до структури та характеристики земель, і інформації щодо їх власників, взято в публічного джерела Публічної кадастрової карти України, <http://map.land.gov.ua/kadastrova-karta> та застосуванням програмного забезпечення QGIS Desktop 3.0

Підставою для розробки генерального плану селища Сонячне є Рішення Широківської сільської ради Запорізького району Запорізької області №15 від 31 серпня 2017 року Про розробку містобудівної документації «Генеральний план селища Сонячне Запорізького району Запорізької області. Оновлення з розширенням меж населеного пункту та План зонування селища Сонячне Запорізького району Запорізької області(у складі Генерального плану)».

Завдання на проектування генерального плану та плану зонування території селища Сонячне Запорізького району Запорізької області.

Необхідність розробки генерального плану викликана змінами, які відбуваються в соціально-економічній діяльності країни і пов'язані з переходом до ринкової економіки, а також відсутністю сучасної, в концептуальному відношенні, проектної містобудівної документації, спрямованої на перспективний розвиток поселення.

Генеральний план населеного пункту виконаний відповідно до: Схеми планування території Запорізької області, яка затверджена Рішенням Обласної ради від 29.12.2011 №4.

Нормативно правова база:

- Водний кодекс України
- Земельний кодекс України
- Закон України «Про основи містобудування»
- Закон України «Про регулювання містобудівної діяльності»
- Закон України «Про Генеральну схему планування території України»
- Закон України «Про охорону навколишнього природного середовища»
- Закон України «Про автомобільні дороги»

• Постанова Кабінету Міністрів України від 04.03.1997 №209 «Про затвердження Правил охорони електричних мереж»

• ДБН 360-92** «Містобудування. Планування і забудова міських і сільських поселень» (зі змінами №1-4)

• ДБН Б.1.1-15:2012 «Склад та зміст генерального плану населеного пункту»

Погоджено		
Інв. № об.	Підпис і дата	
	Зам. Інв. №	

117/2017-ПЗ						Аркуш
Зм.	Кіл.	Арк.	№ док.	Підпис	Дата	

- ДСТУ-НББ.1-1-12:2011 «Настанова про склад та зміст плану зонування території (зонінг)»
- ДСТУ Б Б.1.1-17:2013 Умовні позначення графічних документів містобудівної документації
- ДБН 360-92** «Містобудування. Планування і забудова міських і сільських поселень» (зі змінами №1-4)
- ДСП 173-96 «Державні санітарні правила планування та забудови населених пунктів»
- ДБН Б.1.1-14:2012 «Склад та зміст детального плану території»
- ДБН Б.2.2-5:2011 «Планування та забудова міст, селищ і функціональних територій. Благоустрій територій»
- ДБН В.1.1.7-2016 «Пожежна безпека об'єктів будівництва»
- ДБН В.1.1-25-2009 «Інженерний захист територій та споруд від підтоплення та затоплення»
- ДБН В.2.3-4-2015 «Споруди транспорту. Автомобільні дороги»
- ДБН В.2.3-5-2017 «Вулиці та дороги населених пунктів»
- ДБН В.2.5-20-2001 «Інженерне обладнання будинків і споруд. Зовнішні мережі та споруди. Газопостачання»
- ДБН В.2.5-64:2012 «Внутрішній водопровід та каналізація»
- ДБН В.2.5-74:2013 «Водопостачання. Зовнішні мережі та споруди»
- ДБН В.2.5-75:2013 «Каналізація. Зовнішні мережі та споруди»

Головна мета розробки генерального плану населеного пункту полягає у обґрунтуванні потреб і визначенні основних напрямків використання території; урахуванні державних, громадських і приватних інтересів під час планування і використання території; визначення меж функціональних зон, пріоритетних і допустимих видів використання та забудови території; формуванні планувальної структури та просторової композиції забудови селища; оцінці загального стану довкілля населеного пункту і визначенні містобудівних заходів щодо поліпшення екологічного та санітарно-гігієнічного стану, а також визначенні території, які мають інженерно-будівельні, санітарно-гігієнічні, природоохоронні та інші обмеження їх використання.

Згідно з пунктом 12 статті 17 Закону України «Про регулювання містобудівної діяльності» експертизі містобудівної документації на місцевому рівні підлягають виключно генеральні плани міст, тому генеральний план селища Сонячне не потребує експертизи.

Розрахунковий термін проекту прийнятий до 2038 року, і складає 20 років з відокремленням першої черги – 5 років, до 2023 р.

Розділ «Інженерно-технічні заходи цивільного захисту (цивільної оборони)» розробляється за спеціальним завданням окремим томом відповідно до ДБН Б.1.1-5:2007 «Склад, зміст, порядок розроблення, погодження та затвердження розділу інженерно-технічних заходів цивільного захисту (цивільної оборони) у містобудівній документації».

Погоджено			
Інв. № об.	Підпис і дата		
	Зам. Інв. №		

Зм.	Кіл.	Арк.	№ док.	Підпис	Дата	117/2017-ПЗ	Аркуш

РОЗДІЛ 2. АНАЛІТИЧНА ЧАСТИНА.

2.1. Географічне розташування населеного пункту, його адміністративний статус, відомості про площу території та численність населення, місце в системі розселення.

Селище Сонячне примикає до міста Запоріжжя (район Осипенківський). Поруч проходять автомобільна дорога Н08 Запоріжжя – Дніпро і залізниця, станція Хортиця за 1 км. 1927 – дата заснування села як Приміське. Селище Сонячне входить до Широківської територіальної громади.

Загальна площа населеного пункту 223,20 га. Загальна кількість населення станом на 01.01.2017–915 осіб, в тому числі дорослих 640, пенсіонерів 107, дітей дошкільного віку 59, школярів 109.

2.2. Оцінка реалізації попереднього генерального плану, характеристика стану території населеного пункту та проблем її використання.

14 червня 2007 року Рішенням Сонячної сільської ради Запорізького району Запорізької області був затверджений проект коригування генерального плану забудови сел. Сонячне Сонячної сільської ради Запорізького р-ну., розроблений Державно-кооперативним проектно-вишукувальним інститутом «Запоріжзагропроект».

Проектом передбачена площа населеного пункту 203,1 га.

З об'єктів обслуговування передбачалось будівництво дитячого садка та магазину, ці наміри не були реалізовані. Садибна забудова виконана в значній кількості. Транспортна схема досить точно відповідає рішенням попереднього генерального плану. Вільних ділянок для будівництва об'єктів соціальної інфраструктури в межах населеного пункту, в тому числі дитячого садочку не залишилось.

Мешканці населеного пункту обслуговуються об'єктами соціальної інфраструктури м. Запоріжжя.

2.3. Аналіз зовнішніх та внутрішніх факторів, що визначають конкурентні переваги та обмеження розвитку населеного пункту.

Генеральний план населеного пункту розробляється та затверджується в інтересах відповідної територіальної громади з урахуванням державних, громадських та приватних інтересів.

Відповідно до планувальних рішень Схеми планування території Запорізької області, яка затверджена рішенням Запорізької обласної ради від 29.12.2011 №4, територія селища Сонячне за функціональним зонуванням відноситься до територій з пріоритетним розвитком високотехнологічних галузей промисловості та окремих метрополітарних (фінанси, наука, виставкова діяльність тощо) видів діяльності та до

Погоджено		
Зам. Інв. №		
Підпис і дата		
Інв. № об.		

Північної (Запорізької) підзони урбанізації-з критичним рівнем виробничо-містобудівного освоєння території.

Перспективи розвитку району пов'язано із використанням переваг транспортно-географічного положення.

2.4. Характеристика структури та обсягів існуючого житлового фонду, об'єктів обслуговування, перелік об'єктів господарського комплексу, інженерно-транспортної інфраструктури, інженерної підготовки та благоустрою, захисту території від небезпечних природних і техногенних процесів.

Існуючий житловий фонд селища представлений садибними та багатоквартирними будинками. Садибна забудова 352 одиниці, загальною площею-50298 м2, житловою площею-23712 м2.

Багатоповерхових будинків-2. П'ятиповерховий будинок по вул. Інститутська-2126,9 м2 загальної площі, п'ятиповерховий будинок по вул. Весняна-2704,8 м2. В селищі існують два магазини продовольчих товарів торгівельною площею 51,2 та 46,6 м2. В селищі існують дитячий майданчик площею 550,70 м2 по вул. Весняна,1 та спортивний майданчик площею 275,36 м2 по вул.Весняна,1.

В межах населеного пункту розташована Адмінбудівля Інституту Олійних культур орієнтовною площею 3,8502 га.(Державний акт на право постійного користування землею ІІ-ЗП №002385 від 27.05.2004 за №5).

Селище забезпечене електропостачанням, існує 16 розподільчих підстанцій які отримують живлення від ПЛ-10кВ ПС 35/10 кВ «Українська».

Існують мережі водопостачання, каналізування, газопостачання. Будівля Інституту олійних культур та багатоповерхова забудова забезпечені теплопостачанням та гарячою водою від міських мереж.

2.5. Аналіз відомостей про стан навколишнього середовища.

Навколишнє середовище знаходиться в нормальному стані. Негативного впливу промислових об'єктів не зафіксовано. Інженерні мережі, що перетинають ділянку мають відповідні охоронні зони які відображені на листі сучасного використання території. На розвиток території впливає розташування ландшафтного заказника місцевого значення-«Балка Хуторська» та ботанічного заказника місцевого значення-«Цілинна Ділянка» тому необхідно враховувати вимоги ст. 59 Закону України «Про охорону навколишнього середовища».

Кліматичні умови.

-Середня температура повітря +9,0 гр., липня-22,8 гр. січня-мінус 4,9 гр.;

-Абсолютний мінімум-мінус 34 гр.;

-Абсолютний максимум-плюс 41 гр.;

-Найбільш холодна п'ятиденка-мінус 23 гр.;

-Зимова вентиляційна-мінус 8,5 гр.;

-Опалювальний період-175 днів, середня температура-мінус 0,4 гр.;

Погоджено			
Інв. № об.	Підпис і дата		
	Зам. Інв. №		

117/2017-ПЗ						Аркуш
Зм.	Кіл.	Арк.	№ док.	Підпис	Дата	

- Середня глибина промерзання ґрунтів-80 см.;
- Середня кількість опадів-480 мм.;
- Середня висота снігового покриву-14 см.;
- Домінуючи вітри-північно-східні (17,4%), північні-(15,2), східні-(14,8).;
- Середня швидкість вітру-3,8 м/с.;

Геологічні умови.

- Просадність ґрунтів, потужність(м)-1,5-2,0 величина просадки(см)-3-50, глибина ґрунтових вод(м)-1-19, тип ґрунтових умов I,II.
- Рельєф території спокійний з перепадом висот від 87,0 м до 106,0 м. Стан навколишнього природного середовища задовільний.

2.6. Аналіз ресурсного потенціалу, тенденції розвитку населеного пункту та прилеглих територій.

Відповідно до листа № 11165/08-24 від 17.01.2018 Запорізької обласної державної адміністрації про визначення державних вимог та Схеми планування території Запорізької області, яка затверджена рішенням Запорізької обласної ради від 29.12.2011 №4, на території селища Сонячне передбачено:

Зона впливу автомобільного транспортного коридору Європа-Азія;

Будівництво транспортних розв'язок в різних рівнях;

Будівництво автостоянки для відстою вантажного транспорту.

Важливим є вплив на потенціал території траси Запоріжжя-Дніпро та близькість Осіпенківського району м. Запоріжжя, в тому числі його промислових комунальних об'єктів та структури об'єктів обслуговування.

Погоджено		

Зам. Інв. №

Підпис і дата

Інв. № об.

Зм.	Кіл.	Арк.	№ док.	Підпис	Дата	117/2017-ПЗ	Аркуш

РОЗДІЛ 3. ОБГРУНТУВАННЯ ТА ПРОПОЗИЦІЇ

3.1. Основні пріоритети та цільові показники соціального і демографічного розвитку території з метою формування повноцінного життєвого середовища

Станом на 01.01.2017 чисельність населення становить 915 осіб. В даний час приросту населення не відбудується, але є звернення садівничих товариств та мешканців вул. Талалихіна, щодо включення їх територій в межі селища Сонячне. Органи місцевого самоврядування мають наміри змінити межі селища з метою включення цих та інших територій, а саме нової садибної та громадської забудови до меж селища. Передбачається також розміщення об'єктів логістики, торгівлі, транспорту, комунального призначення, альтернативної енергетики тощо. В першу чергу пропонується розмістити центр ПМД (ФАП) Широківської ОТГ, адміністративна будівля, спортивний майданчик (футбольне поле з штучним покриттям), спортивно-оздоровчий комплекс, спортивно-оздоровчий центр, адміністративно-торгівельний центр.

На вільних територіях в нових межах селища розміщується школа, дитячий садок, адміністративний центр з об'єктами торгівлі, паркова зона з майданчиками відпочинку.

3.2. Цільові показники і галузева структура економічної діяльності та зайнятості населення

Основні фактори що стимулюють перспективний розвиток селища – це екологічні, територіальні та транспортні ресурси.

Мешканці населеного пункту у зв'язку з приміським його положенням працевлаштовані в м. Запоріжжі.

У якості територіальних ресурсів розглядаються вільні від забудови землі, що розташовані в північно-західному напрямку від існуючої межі селища. Транспортний коридор Запоріжжя-Дніпро дає можливість активно розвивати об'єкти логістичного та транспортного напрямку.

Планується розміщення торгових, виставкових та логістичних центрів, багатofункціонального торгівельно-виставкового комплексу.

В південно-західному напрямку, на території міста Запоріжжя знаходиться завод «Армаліт», інші підприємства.

3.3. Характеристика територій, необхідних для подальшого розвитку населеного пункту, а також території спільних інтересів суміжних територіальних громад.

Відповідно до аналізу рівня соціально-економічного розвитку окремих токсинів Запорізької області Запорізький район відноситься до 3 типу

Погоджено					
Інв. № об.	Зам. Інв. №		Підпис і дата		

117/2017-ПЗ						Аркуш
Зм.	Кіл.	Арк.	№ док.	Підпис	Дата	

токсинів із середнім показником потенціалу та середнім рівнем соціально-економічного та містобудівного розвитку. В районі планується розвиток багатоступеневої системи громадського обслуговування населення з розміщенням підприємств повсякденного та періодичного обслуговування.

Територією спільних інтересів суміжних територіальних громад є садибна забудова вздовж вул. Талалихіна, гаражного та садибного кооперативів. Генеральним планом передбачається включення цих територій в межі селища Сонячне.

Відповідно до Рішення сільської ради та Завдання на проектування проектом генерального плану передбачається змінити площу та межі населеного пункту за рахунок територій, що приєднуються. Прогнозна чисельність населення селища в 1200 осіб на розрахунковий період, відповідно до Завдання на проектування, при приєднанні території вул, Талалихіна, розміщенні нової садибної забудови кількість садибних ділянок становитиме орієнтовно 1234 ділянки. Таким чином при $k=3,5$ розрахункова чисельність населення становитиме $1234 \times 3,5 = 4319$ осіб. Крім того орієнтовна чисельність жителів в п'ятиповерхових будинках складає $2126,9 + 2704,8 = 4831,7 : 35 = 138$ мешканців. Всього розрахункова чисельність 4457 осіб.

Дітей до працездатного віку (до 16 років) $4457 \times 0,126$ буде 562 дитини, з них 198 дошкільного віку та 364 школяра.

3.4. Пропозиції щодо зміни меж населеного пункту.

Головною метою генерального плану є приєднання садибних товариств з північно-східного напрямку до меж селища, садибних товариств з північно-західного напрямку до меж селища, включення до меж селища території для майбутньої садибної забудови та об'єктів обслуговування з західного напрямку, включення в межі селища садибництва, садибної забудови та гаражного кооперативу вздовж вул. Талалихіна. Вздовж транспортного коридору Запоріжжя-Дніпро розміщуються багатофункціональні торгівельно-виставкові та логістичні центри, пропонується ділянка для альтернативної енергетики.

Площа селища Сонячне в старих межах була 223,20 га, в нових 523,7728 га.

3.5. Опис перспективної планувальної структури та функціонального зонування.

Планувальна структура селища Сонячного, в старих межах, принципів змін не потребує. Планується влаштування продільних доріг, які об'єднують проектну автомагістраль зі східного напрямку всю існуючу та проектну забудову з магістраллю Запоріжжя-Дніпро в західному напрямку. Планується система поперечних доріг та проїздів для зручного автомобільного та пішохідного зв'язку

Погоджено					
Інв. № об.	Підпис і дата				
	Зам. Інв. №				

Враховуючи значну відстань між західною та східною частинами селища, пропонується організація двох громадських підцентрів в існуючій забудові та проектній.

Планується влаштування переходу через трасу Запоріжжя-Дніпро в районі південного садівництва для зручного сполучення південної та північної частини селища.

Зона розміщення об'єктів обслуговування транспортної інфраструктури розташована вздовж існуючої траси Запоріжжя-Дніпро.

3.6. Характеристика територій та визначення заходів щодо їх освоєння.

В межах населеного пункту розташовані різні за призначенням території, а саме:

- території житлової садибної забудови;
- території багатоквартирної забудови;
- землі громадської забудови;
- територія транспортної інфраструктури;
- території інженерної інфраструктури;
- територія комунальних об'єктів;
- територія рекреаційного призначення;
- територія оздоровчого призначення;
- території зелених насаджень загального користування;
- території зелених насаджень спеціального призначення;

3.7. Пропозиції щодо формування системи громадських центрів.

Згідно до п. 2.19 ДБН 360-92** площа громадського центру сільського населеного пункту повинна розраховуватися 8-12 м² на людину. Розрахунковий розмір площі громадського центру села становитиме:

$$4319 \text{ мешканців} \times (8)12 \text{ м}^2 = (34552) 51828 \text{ м}^2.$$

Мешканці населеного пункту використовують також об'єкти інфраструктури Широківської об'єднаної громади та м.Запоріжжя.

Загальна місткість мережі установ та підприємств культурно – побутового обслуговування населення

№п/п	Найменування об'єкту	Одиниця виміру	Потрібно за розрахунком	Існуючи що зберігаються	Додаткові
1.	Дитячі дошкільні установи	місць	198x0,8=158	-	200
2	Загально освітні школи	місць	364	-	400
3	Професійно – технічні та	учнів	По завданню на проектування	-	-

117/2017-ПЗ

Аркуш

Зм.	Кіл.	Арк.	№ док.	Підпис	Дата
-----	------	------	--------	--------	------

Погоджено

Зам. Інв. №

Підпис і дата

Інв. № об.

						16
	середні спеціальні заклади					
4	Лікарні	ліжко	6,9x4,457=31	-	-	
5	Поліклініки	відвідань за зміну	24x4,457=107	-	ФАП	
6	Аптеки	об'єкт	0,143x4,457=0,6	-	-	
7	Станція швидкої допомоги	автомобіль	-	-	-	
8	Фізкультурно – спортивні споруди	га	0,7x4,457=3,0	-	1майданчик	
9	Спортивні зали загального користування	м2 підлоги	80x4,457=357	-	В школі	
10	Клубні установи та центри дозвілля	місць відвідувачів	131,7x4,457=587	-	В школі	
11	Бібліотеки	читачів, місць	3x4,457=13,0	-	В школі	
12	Культові споруди	по завданню	-	існуюча	існуюча	
13	Магазини продовольчих товарів	м2 торгівельні й площі	85x4,457=379	51,2+46,6	280	
14	Магазини непродовольчих товарів	М2 торгівельні й площі	165x4,457=735	-	750	
15	Підприємства громадського харчування	місць	40x4,457=178	-	200	
16	Підприємства побутового обслуговування	робочих місць	5x4,457=22	-	-	
17	Пральні	кг /білизни /зміну	10x4,457=46	-	-	
18	Хімчистки	кг/речей зміну	4,0x4,457=18	-	-	
19	Бані, лазні	Пом. м.	5,7x4,457=25	-	-	
20	Відділення зв'язку	об'єкт	за нормами Мінзв'язку	1	-	
21	Відділення банків	операторська каса	-	1	-	
22	Організації установ управління	об'єкт	По завданню	1	-	
	Пожежні депо	пожежних	-	-	-	
Зм.	Кіл.	Арк.	№ док.	Підпис	Дата	117/2017-ПЗ
						Аркуш

23		машин			
24	Готелі	місць	$4,8 \times 4,457 = 21$	-	-
25	Громадські вбиральні	прилад	$1 \times 4,457 = 5$	-	В об'єктах обслуговува ння
26	Кладовище	га	$0,1 \times 4,457 = 0,46$	-	-

3.8. Обсяги житлового будівництва.

Обсяг і структура житлового будівництва в межах селища Сонячне визначені виходячи з необхідності досягнення цільових стандартів житла, тобто забезпечити кожну родину окремою квартирою або будинком виглядає таким чином: існуючий стан-352 садиби. Незабудованих ділянок в старих межах 585, в районі вул Талалухіна, що входить в нові межі селища, орієнтовно 117 садиб, на вільній від забудови території в західній частині -180 ділянок.

Тобто $585 + 180 = 765$ нових садибних житлових будинків.

3.9. Напрями розвитку вулично – дорожньої мережі, транспорту, інженерної інфраструктури.

Ширина вулиць і доріг визначається залежно від інтенсивності руху транспорту і пішоходів, складу елементів, які розміщуються в межах поперечного профілю, з урахуванням санітарно – гігієнічних вимог і вимог цивільної оборони.

Класифікація вулиць і доріг сільських населених пунктів визначають згідно з таблицею 7.3 ДБН 360-92**.

До категорії головних вулиць відноситься вулиці які мають поперечний профіль, в червоних лініях, 38, 30, 25 метрів. Вулиці 15 та 12 метрів-житлові, 10 метрів-проїзд. Генеральним планом м. Запоріжжя передбачається прокладання нової проектної магістралі безперервного руху в східній частині ДПТ, яка перетинатиме зелену зону, передбачається також реконструкція магістралі Запоріжжя-Дніпро в магістраль безперервного руху.

3.10. Заходи з інженерної підготовки та захисту території від небезпечних геологічних та гідрогеологічних процесів, організації відведення поверхневих вод.

Заходи з інженерної підготовки і захисту території проектується у відповідності до розділу 9 ДБН 360-92**.

Згідно з таблицею 9.1., враховуючи схил рельєфу від 0,5 до 8,0%, територія вважається сприятливою для будівництва. Беручи до уваги те що більшість ґрунтів на території є такими, що просідають першого типу, ділянка вважається малосприятливою. З точки зору затоплюваності

Погоджено			
Інв. № об.	Підпис і дата	Зам. Інв. №	

Зм.	Кіл.	Арк.	№ док.	Підпис	Дата	117/2017-ПЗ	Аркуш
-----	------	------	--------	--------	------	-------------	-------

територія являється сприятливою. Заболоченості, зсувів, карстів, ярів, заторфованості, гірських виробіток на території немає.

Відведення поверхневих вод проектується в бік балки в західному напрямку та зону зелених насаджень в східному напрямку.

Поверхнєве водовідведення поверхневих вод, згідно з п. 9.4. ДБН 360-92**, виконується відкритою водовідвідною мережею з улаштуванням труб на пересіканнях з вулицями, дорогами, поїздами та тротуарами.

Генеральним планом пропонується розчистка та благоустрій водних об'єктів на території селища для поліпшення екологічних та кліматичних умов, створення місць відпочинку.

3.11. Пропозиції щодо охорони навколишнього середовища, подолання та запобігання впливу проявів негативних природно – техногенних факторів для поліпшення життєвого середовища.

При проектуванні нових і розвитку існуючих сільських поселень слід користуватися вимогами наведеними в розділі 10 ДБН 360-92**.

Навкрузи водних поверхонь запроектовані прибережні захисні смуги 25 метрів. Генеральним планом передбачені охоронні зони вздовж ПЛЕ. Визначені санітарно – захисні зони існуючих об'єктів інженерної інфраструктури та діючих підприємств і споруд.

3.12. Пропозиції щодо збереження та охорони нерухомих пам'яток культурної спадщини, територій, що мають статус земель історико – культурного призначення.

Запорізька обласна державна адміністрація своїм листом №11165/08-24 від 17.01.2017 «Про визначення та врахування державних та регіональних інтересів під час розроблення генерального плану селища Сонячне» зазначила що при розроблені містобудівної документації необхідно врахувати розташування ландшафтного заказника місцевого значення – «Балка Хуторська» та ботанічного заказника місцевого значення «Цілинна Ділянка» та ст. 59 Закону України «Про охорону навколишнього природного середовища», п. «2» ст. 32 Закону України «Про відходи», ст.87,88,89 Водного кодексу України, ст.60,61 Земельного кодексу України.

В околицях селища Сонячне Запорізького району знаходяться пам'ятки археології місцевого значення, але всі вони за новими межами населеного пункту. Відповідно до статті 37 Закону будівельні, меліоративні, шляхові та інші роботи, що можуть призвести до руйнування, знищення чи пошкодження об'єктів культурної спадщини, проводяться тільки після повного дослідження цих об'єктів за рахунок коштів замовника зазначених робіт.

Беручи до уваги вищеперелічені об'єкти необхідним є дотримання вимог Законів України «Про охорону культурної спадщини» і «Про охорону археологічної спадщини».

Погоджено			
Інв. № об.	Підпис і дата		Зам. Інв. №

3.13. Рекомендації щодо встановлення режиму використання території, визначених для майбутніх містобудівних потреб.

У разі виникнення потреби в межах існуючих ділянок перебудови старих або будівництва нових об'єктів, необхідно передбачати заходи щодо розміщення об'єктів в межах земельної ділянки згідно зонувannya території.

Проектним рішенням нове житлове будівництво передбачається здійснювати відповідно до структури житлової забудови.

При забудові сільбищних територій, території громадського центру та підцентру, територій сільськогосподарського, комунального та промислового призначення необхідно керуватися вимогами зонінга, який розроблений в розвиток генерального плану і являється його невід'ємною частиною.

3.14. Рекомендації щодо розроблення плану зонування території або черговості виконання плану зонування його окремих частин та детальних планів територій.

Генеральний план з планом зонування селища Сонячне, у відповідності до існуючого законодавства, публікується в засобах масової інформації, сільська рада ініціює і організовує обговорення проекту. Проект погоджується з відповідними службами і затверджується сільською радою.

У відповідності до першочергових заходів виділяються об'єкти, на які розробляється проектна документація для подальшого будівництва, за необхідністю детальні плани окремих функціональних зон, робочі проекти окремих будівель та споруд.

3.15. Розрахункові показники та заходи що до розвитку:

• Житлового будівництва.

В діючий час в селищі Сонячне існує 352 садиби. Незабудованих ділянок в старих межах селища налічується 585, в районі вул Талалихіна, що входить в нові межі селища, орієнтовно 117 садиб, на вільній від забудови території в західній частині – 180 ділянок.

Тобто $585 + 180 = 765$ нових садибних житлових будинків.

Проектним рішенням нове житлове будівництво передбачається здійснювати відповідно до структури житлової забудови.

Нове багатоквартирне будівництво не планується.

Показники по житловому будівництву та інші наведені в таблиці «Основні показники генерального плану».

• Системи громадських центрів.

Враховуючи досить велику площу селища, значні відстані від східної до західної частини планується вдосконалення громадського центру що формується в південно-східній частині існуючої забудови та організація

Погоджено		
Зам. Інв. №	Підпис і дата	Інв. № об.

117/2017-ПЗ						Аркуш
Зм.	Кіл.	Арк.	№ док.	Підпис	Дата	

нового громадського центру в західній частині, на вільній від забудови території.

- **Соціальної інфраструктури державної та комунальної власності.**

Із об'єктів комунальної власності планується розміщення в першу чергу центр ПМД (ФАП) Широківської ОТГ, адміністративну будівлю, спортивний майданчик (футбольне поле з штучним покриттям), спортивно-оздоровчий комплекс, спортивно-оздоровчий центр, адміністративно-торгівельний центр.

На вільних територіях в нових межах селища розміщується школа, дитячий садок, адміністративний центр з об'єктами торгівлі, паркова зона з майданчиками відпочинку.

- **Озеленених територій загального користування, ландшафтно – рекреаційних територій населеного пункту.**

Територія володіє значним природо-ресурсним потенціалом для забезпечення відпочиваючих різними формами відпочинку. Основним об'єктом рекреаційних навантажень являються зелена зона, розташована в південно-східній частині території, яка спроможна максимально забезпечити відпочиваючих природними ресурсами.

На території населеного пункту розміщуються спортивно-оздоровчий центр та комплекс загального користування, парк, зберігається ботанічний заказник «Цілинна балка»

Формування планувальної структури з урахуванням ландшафтних особливостей та екологічно-допустимої рекреаційної ємності території: створення локальних місць рекреаційного використання з урахуванням асортименту зелених насаджень, охорони флори і фауни, та нормативне забезпечення рекреаційних зон системою зелених насаджень загального користування. Велике значення має в ландшафтно – рекреаційних ресурсах селища відіграє ландшафтний заказник «балка Хуторська», що знаходиться за межами селища в північному напрямку та ботанічний заказник місцевого значення «Цілинна ділянка».

Вулично – дорожньої мережі за її категоріями з виділенням ділянок нового будівництва та реконструкції, будівництва мостів.

Вулично – дорожня мережа існуюча. Передбачається улаштування всіх доріг населеного пункту з твердим покриттям.

Значний вплив на схему транспортного сполучення відіграють дві магістралі безперервного руху, які передбачені генеральним планом м. Запоріжжя.

До категорії головних вулиць відноситься вул. Академічна, вул. Першотравнева та вул. Лазурна, до категорії селищних доріг відносяться інші вулиці селища.

Погоджено		
Зам. Інв. №		
Підпис і дата		
Інв. № об.		

Зм.	Кіл.	Арк.	№ док.	Підпис	Дата	117/2017-ПЗ	Аркуш

- Інженерної інфраструктури за видами (водопостачання, водо відведення, газо -, електро -, теплопостачання).

Водопостачання.

Існуюче положення.

Наразі джерелом водопостачання даного населеного пункту є дніпровська вода водоводу належить КП «Водоканал».

Норми господарчо-побутового питного водопостачання та коефіцієнти, добової нерівномірності споживання води прийняті у відповідності до ДБН В.2.5-74:2013. Витрати питної води на благоустрій території прийняті у відповідності з додатком «А» зазначеного ДБН.

Розрахункові витрати води на господарсько-побутові потреби населення зазначені в таблиці. Для повного забезпечення селища водою питної якості необхідно:

- Будівництво кільцевих водопровідних мереж у районах нового будівництва та районах існуючої забудови, де водопровідні мережі відсутні;
- Провести перекладку і реконструкцію зношеної водопровідної мережі.

Проектом передбачено здійснити ввід водогінної мережі в усі житлові будинки а також в будівлі і споруди громадського і культурно- побутового та іншого призначення.

Мінімальний вільний тиск у водогінній мережі на вводі у будівлі приймається:

- При одноповерховій забудові – не менш ніж 10 м;
- При п'ятиповерховій забудові – 26 м і забезпечується зовнішньою водогінною мережею.

З водопровідної мережі питна вода буде подаватись на господарсько-питні потреби населення, об'єкти громадсько-культурного і побутового призначення, а також на виробничі потреби промислових підприємств, яким за технологією виробництва необхідна вода питної якості.

Проектом передбачається заміна старих, зношених водопровідних мереж та будівництво нових у районах нового будівництва з пластмасових

(поліетиленових) труб діаметрами 100 мм.

Для економії енергетичних ресурсів та скорочення невиробничих витрат води генеральним планом передбачена обладнання всіх споживачів приладами обліку.

Зони санітарної охорони

Згідно з ДБН В.2.5-74:2013 для забезпечення санітарно- епідеміологічної безпеки та охорони від забруднення джерел і

Погоджено		
Зам. Інв. №		
Підпис і дата		
Інв. № об.		

водопровідних споруд системи централізованого питного водопостачання передбачається створення зон санітарної охорони.

Для водоводів ширина санітарно-захисної смуги при прокладанні в сухих ґрунтах не менше ніж 10 метрів при умовному діаметрі до 1000 мм, в мокрих ґрунтах — не менше ніж 50 метрів.

Протипожежні заходи

Протипожежний водопровід, об'єднаний з господарсько-питним, проектується по кільцевій схемі, що дозволяє робити пожежогасіння пожежними гідрантами, які встановлюються в колодязях на трасах водогінних мереж уздовж проїздів з інтервалами не більше 150 м один від одного.

Необхідний напір для гасіння пожежі створюється пересувними автопомпами пожежних команд.

Розрахункова витрата води на пожежогасіння приймається згідно з ДБН В.2.5-74:2013 і становить 15 л/с при кількості одночасних пожеж — 2.

Витрата води на внутрішнє пожежогасіння враховується за найбільшою розрахунковою потребою на один будинок з водопроводом, і приймається з розрахунку 2 пожежні струмені продуктивністю 5 л/с. Тривалість пожежі — 3 години.

Каналізація.

Існуюче положення.

Наразі неподалеку від даної території проходить централізована мережа каналізації dy400 КП «Водоканал».

Стічні води від забудови, що каналізується, будуть надходити самотливом до місця приєднання.

Проектні пропозиції.

Проектом передбачається здійснення каналізування усіх житлових забудов, усієї нової та частково існуючої забудови.

Кількість стічних вод від житлової забудови селища визначена відповідно до чисельності населення, характеру забудови та норм водовідведення згідно з ДБН В.2.5-75:2013.

Для прийняття стічних вод від кафе та ресторанів необхідне будівництво жироловлівачів перед змішуванням жиромісних стоків з господарсько-побутовими стічними водами.

Каналізаційна мережа запроектована з пластмасових (поліпропіленових) труб: самотливних — діаметрами 150 — 400 мм.

Погоджено		
Зам. Інв. №	Підпис і дата	Інв. № об.

Зм.	Кіл.	Арк.	№ док.	Підпис	Дата	117/2017-ПЗ	Аркуш

ОСНОВНІ ПОКАЗНИКИ

Інженерне забезпечення		Існуючий стан	Етап 5-20 р.
Водопостачання			
Сумарний відпуск води	м3/добу		1145,7
Потужність головних споруд водопроводу	м3/добу		1150,0
Каналізація			
Загальне надходження стічних вод	м3/добу		1145,7
Сумарна потужність очисних споруд	м3/добу		1150,0

Газопостачання:Існуюче положення:

Наразі, в селища Сонячне газопостачання забезпечується від функціонуючих ГРП.

Проектні пропозиції:

Проектом передбачено забезпечення газопостачанням від існуючих мереж всіх об'єктів житлового та громадського призначення.

Електропостачання.

Електропостачання запроектовано відповідно до вимог ПУЕ-2017, ДБН В.2.5-23:2010.

На території селища Сонячне Запорізького району Запорізької області розташовано 16 розподільчих підстанцій 10/0,4кВ:

- КТПс 172/105- 160 кВА
- КТП 172/606 - 250 кВА
- КТП 172/670 - 400 кВА
- КТП 172/810 - 250 кВА
- КТП 172/815 - 250 кВА
- КТП 172/857 - 160 кВА
- КТП 172/980 - 315 кВА
- КТП 174/209 - 400 кВА
- КТП 174/630 - 250 кВА
- КТП 174/632 - 63 кВА
- КТП 174/784 -400 кВА
- КТП 174/799 - 100 кВА
- КТП 174/937 - 160 кВА

Погоджено		
Інв. № об.	Підпис і дата	Зам. Інв. №

- КТП 177/803 – 400 кВА
- КТП 177/668 – 100 кВА
- КТП 177/913 – 250 кВА

Існуючі трансформаторні підстанції 10/0,4кВ на території селища Сонячне отримують живлення від ПЛ-10кВ ПС 35/10кВ «Українська». Резервна потужність на існуючих трансформаторних підстанціях 10/0,4кВ присутня, але з урахуванням перспективи розвитку населеного пункту та територіального розташування не достатня.

Для електропостачання території селища Сонячне, що проектується, передбачено будівництво двох трансформаторних підстанцій 10/0,4кВ, що призведе до збільшення загальної потужності до 3508,0кВА. Лінії 10кВ передбачені повітряними з використанням типових залізобетонних опор. В обмежених умовах можливо використовувати кабельні лінії.

Передбачити будівництво двох КТП-10/0,4кВ потужністю 400кВА кожна.

Загальна розрахункова потужність (проект.) – 736,0 кВт.

В тому числі:

споживачі II категорії – 80кВт (школа загальноосвітня та дитячий садок)

споживачі III категорії – 565,0кВт

Довжина повітряних ліній 10кВ, що передбачені для проектування складає:

ПЛ-10кВ – 1064м

Довжина повітряних ліній 0,4кВ, що передбачені для проектування складає:

ПЛ-0,4кВ – 3968м.

Комплектні трансформаторні підстанції 10/0,4кВ прийняті типу КТПГС з одним трансформатором для споживачів III категорії.

Передбачено живлення споживачів II категорії від різних трансформаторних підстанцій.

Потужності трансформаторних підстанцій прийняті на основі розрахунків навантажень.

Повітряні лінії 0,4кВ передбачено виконувати з використанням залізобетонних опор та самоутримного ізольованого дроту типу СІП5нг.

В обмежених умовах можливо використовувати кабельні лінії.

Погоджено		

Зам. Інв. №

Підпис і дата

Інв. № об.

Електропостачання		Існуючий стан	Етап 5-20 р.
Сумарне споживання електроенергії	Млн. кВт год./рік	18,173	20,675
Потужність джерел покриття електронавантажень	Тис. кВт	5,345	6,081

Опалення:

Опалення садибної забудови селища Сонячне здійснюється від газових та електричних мереж та котлів на твердому паливі. В житловій садибній забудові використовуються також пічне опалення. Багатоповерхова забудова та будівлі інституту олійних культур забезпечені централізованим опаленням та гарячим водопостачанням.

- Мережі розташування об'єктів і місць утилізації побутових відходів, а також місць захоронення тварин.

Тверді побутові відходи в діюсний час вивозяться, відповідно до договорів з обслуговуючими компаніями на існуючий полігон ТПВ.

- Дощової каналізації, інженерної підготовки та захисту території.

Генеральним планом надані пропозиції по вертикальному плануванню та водовідведенню на території населеного пункту.

Виконати розчищення та озеленення прибережних захисних смуг.

Дощова каналізація в генеральному плані не передбачається, вона є обов'язковою для міст.

Погоджено		

Інв. № об. Зам. Інв. № Підпис і дата

Зм.	Кіл.	Арк.	№ док.	Підпис	Дата	117/2017-ПЗ	Аркуш

Основні показники генерального плану населеного пункту

Ч. ч.	Назва показника	Одиниця виміру	Існуючий стан в старих межах	Існуючий стан в нових межах	Розрахунковий етап
1.	Населення	осіб	915	-	4457
2.	Територія в межах населеного пункту, всього:	га	237,61	523,77	523,77
	у т.ч.: житлової забудови, всього	»	142,82	161,43	190,46
	садибної	»	139,77	160,39	189,43
	багатоквартирної	«	3,04	1,03	1,03
	Громадські забудови, всього	»	4,81	4,81	54,65
	Виробничої, всього	»			
	Комунальної, всього	»	0,36	16,94	21,44
	Складської, всього	»			
	Інженерної, всього	»	0,17	0,44	0,44
	Транспортної інфраструктури, всього:	»	-	7,77	7,77
	у т.ч. вулично-дорожньої мережі	«			
	Ландшафтно-рекреаційної та озелененої, всього	»			
	Загального користування (існуюча)	»	2,38	2,38	9,01
	Рекреаційного призначення	«	24,06	121,66	126,55
	Оздоровчого призначення	«	-	-	0,56
	Зелених насаджень спецпризначення	»	13,64	12,16	22,95
	Водних поверхонь	»	0,32	0,32	0,32
	Сільськогосподарських угідь та земель	»			
	Сільськогосподарського призначення	»	5,54	2,32	2,32
3.	Житловий фонд, всього	садибних	464	597	1234

117/2017-ПЗ

Аркуш

Зм. Кіл. Арк. № док. Підпис Дата

Погоджено

Зам. Інв. №

Підпис і дата

Інв. № об.

						27
		дагат оповер хових	2	2	2	
	у т. ч: непридатний житловий фонд	»	-	-	-	
	Розподіл житлового фонду за видами забудови:					
	Середня житлова забезпеченість населення житловою площею	м²/чол	31,19	31,19	35,00	
5.	Об'єкти громадського обслуговування:					
	Дитячі дошкільні заклади, всього	місць	-	-	200	
	Загальноосвітні школи, всього	місць	-	-	400	
	Магазини продоволарів	М2	97,8	97,8	280	
	Магазин непродовольчих товарів	М2	-	-	750	
	Об'єкт громадського харчування	Пос./м ісць	-	-	200	
	фельдшерсько – акушерський пункт, всього	об'єкт	-	-	1	
	Будинок дільничного з квартирою	об'єкт	-	-	1	
	пожежні депо, всього	об'єкт /поже жних автом обілів	-	-	-	
6.	Вулично-дорожня мережа та транспорт населеного пункту					
	Довжина проектних вулиць і доріг	км	-	-	46	
7.	Інженерне забезпечення					
	Теплопостачання	п/м	850,64	1489,77	1489,77	
	Водопостачання	п/м	17701,17	20704,99	28200,5	
	Каналізація самотливна	п/м	2444,71	3156,98	9683,1	
	Каналізація напірна	п/м	-	1538,64	1568,64	
	Телефона каналізація	п/м	529,35	2799,63	2799,63	
	Кабельні лінії електропередач	п/м	746,59	798,36	798,36	
	Повітряні лінії електропостачання	п/м	8923,83	19099,73	24131,89	
Зм.	Кіл.	Арк.	№ док.	Підпис	Дата	117/2017-ПЗ
						Аркуш

РОЗДІЛ 4. ДОДАТКИ.

1. Рішення Широківської сільської ради про розробку містобудівної документації «Генеральний план селища Сонячне Запорізького району Запорізької області. Оновлення з розширенням меж населеного пункту та план зонування селища Сонячне Запорізького району Запорізької області (у складі генерального плану).
2. Завдання на проектування генерального плану з планом зонування території селища Сонячне Запорізького району Запорізької області.
3. Лист Запорізької обласної державної адміністрації №11165/08-24 від 17.01.2018 «Про визначення та врахування державних та регіональних інтересів під час розроблення генерального плану селища Сонячне».
4. Листи Широківської сільської ради з додатками (вихідні данні)
5. Зменшені копії плану існуючого використання території та генерального плану (основне креслення).
6. Копія кваліфікаційного сертифіката серія АА № 003280 зареєстрованого 14 липня 2016 року. Розроблення містобудівної документації.

Погоджено		

Інв. № об. Підпис і дата Зам. Інв. №

Зм.	Кіл.	Арк.	№ док.	Підпис	Дата	117/2017-ПЗ	Аркуш



УКРАЇНА
ШИРОКІВСЬКА СІЛЬСЬКА РАДА
ЗАПОРІЗЬКОГО РАЙОНУ ЗАПОРІЗЬКОЇ ОБЛАСТІ
ШОСТА СЕСІЯ СЬОМОГО СКЛИКАННЯ

РІШЕННЯ

31 серпня 2017 року

№ 15

с. Широке

Про розробку містобудівної документації
«Генеральний план селища Сонячне За-
порізького району Запорізької області.
Оновлення з розширенням меж населено-
го пункту та План зонування селища Со-
нячне Запорізького району Запорізької
області (у складі Генерального плану)».

Враховуючи необхідність раціонального використання земель, ство-
рення належних умов для життєзабезпечення селища Сонячне та керую-
чись п.42 частини 1, ст.26 Закону України “Про місцеве самоврядування в
Україні”, ст.17 Закону України “Про регулювання містобудівної діяльнос-
ті”, Широківська сільська рада

ВИРІШИЛА:

1. Розробити містобудівну документацію «Генеральний план селища
Сонячне Запорізького району Запорізької області. Оновлення з розширен-
ням меж населеного пункту та План зонування селища Сонячне Запорізь-
кого району Запорізької області (у складі Генерального плану)» (далі - міс-
тобудівна документація).

2. Визначити замовником містобудівної документації виконавчий комі-
тет Широківської сільської ради.

3. Внести зміни до бюджету 2017 року, передбачити кошти на фінансу-
вання розроблення містобудівної документації, також при формуванні про-
екту бюджету на 2018 рік передбачити кошти на фінансування розроблення
містобудівної та землевпорядної документації.

4. Визначити організацію-розробника містобудівної документації, яка має право на виконання даного виду робіт, строки розроблення та джерела його фінансування.

5. Повідомити через місцеві засоби масової інформації про початок розроблення містобудівної документації.

6. Укласти договір з організацією-розробником містобудівної документації.

7. Звернутись до Запорізької обласної державної адміністрації щодо визначення державних інтересів для їх врахування під час розроблення містобудівної документації.

8. Забезпечити збір вихідних даних для розроблення містобудівної документації. При розробці технічного завдання та надання розробнику вихідних даних врахувати необхідність будівництва та розміщення адміністративної будівлі Широківської сільської ради по вулиці Весняній у селищі Сонячне Запорізького району Запорізької області.

9. Забезпечити, разом з організацією-розробником, попередній розгляд матеріалів містобудівної документації архітектурно-містобудівною радою при управлінні містобудування та архітектури Запорізької обласної державної адміністрації.

10. Забезпечити проведення громадських слухань, погодження містобудівної документації згідно чинного законодавства, із зарученням організації-розробника.

11. Погодити містобудівну документацію з органами місцевого самоврядування, що представляють інтереси суміжних територіальних громад (у разі необхідності).

12. Виготовлену та погоджену містобудівну документацію затвердити на сесії сільської ради.

13. Контроль за виконанням даного рішення покласти на постійну комісію з питань містобудування, будівництва, земельних відносин, екології, житлово-комунального господарства та комунальної власності.

Сільський голова



Д.О. Коротенко

Затверджено:

Голова Широківської сільської ради

Коротенко Д.О.

_____ 2017р.

М.П.

Погоджено:

Погоджено:

ФО-П Прудка І. А.

_____ Прудка І. А.

«_____» _____ 2017р.

М.П.

Начальник відділу містобудування,
архітектури та житлово-
комунального господарства
Запорізької РДА

Неумивака А.О.

«_____» _____ 2017р.

М.П.

ЗАВДАННЯ

на розроблення містобудівної документації «Генеральний план селища Сонячне Запорізького району Запорізької області. Оновлення з розширенням меж населеного пункту та план зонування селища Сонячне Запорізького району Запорізької області (у складі генерального плану)».

Згідно з ДБН Б.1.1-15:2012 « Склад та зміст генерального плану населеного пункту» та ДСТУ-Н Б Б.1.1-12:2011 « Настанова про склад та зміст плану зонування території (зонінг)».

1. Підстави для проектування	Рішення Широківської сільської ради Запорізького району Запорізької області: «Про Розроблення генерального плану селища Сонячне Запорізького району Запорізької області. Оновлення з розширенням меж населеного пункту та план зонування селища Сонячне Запорізького району Запорізької області (у складі генерального плану)» від 31.08.2017 №15
2. Замовник розроблення генерального плану	Широківська сільська рада Запорізького району Запорізької області.
3. Розробник генерального плану	ФО-П Прудка І. А. Головний архітектор проекту Прудка І. А. Кваліфікаційний сертифікат Серія АА № 003280 (розроблення містобудівної документації).
4. Строк розроблення	Визначається договором на виконання робіт

генерального плану	
5. Мета розроблення генерального плану	Генеральний план необхідно розробити з врахуванням: 1. Розширенням меж населеного пункту та його прилеглої зони, уточнення параметрів забудови; 2. Зміни показників розрахункової чисельності населення та нормативну забезпеченість села об'єктами обслуговування; 3. Необхідністю розроблення нових розділів генплану відповідно до діючого законодавства. 4. З метою визначення умов та обмежень використання території для містобудівних потреб.
6.Строк розрахункового етапу генерального плану та першої черги реалізації	Розрахунковий етап - 2038р.(20років), Перша черга реалізації – 2023р. (5років).
7. Основні показники населеного пункту.	Розробити генерального плану для розміщення населення -на розрахунковий період – 1,200 тис. осіб,
8. Вихідні дані для розроблення генерального плану	1. Електронна векторна карта в межах територіального розвитку, приміської зони масштаб довільний. 2. Матеріали інженерних, інженерно-геологічних та геодезичних вишукувань. 3. Матеріали санітарно-гігієнічного стану території села, обмеження щодо використання різних територій, інших природно-географічних та геологічних факторів. 4. Місцеві програми соціально-економічного розвитку, демографічні дані за останні 10 років, наявність об'єктів соціального, побутового та комунального обслуговування. 5. Дані щодо існуючого використання території (на основі державного земельного кадастру). 6. Історико-культурні об'єкти, охоронні зони та інші умови відносно збереження історико-культурної спадщини. 7. Перелік раніше розробленої містобудівної, землевпорядної документації, проектно-дослідницьких та вишукувальних робіт, які необхідно врахувати при проектуванні.
9. Графічні матеріали з зазначенням масштабу	1. Схема розташування територій, щодо яких вносяться зміни, у функціонально-планувальній структурі населеного пункту - б/м. 2. План існуючого стану населеного пункту (опорний план) М 1 : 5000 3. Схема існуючих планувальних обмежень М 1:5000 4. Основне креслення генерального плану М - 1:5000

	5. Схема планувальних обмежень. М 1:5000 6. Схема магістралей вулично-дорожньої мережі - М 1 : 5000 7. Схема інженерної підготовки території М1:5000 8. Схема інженерного обладнання території М1:5000 9. Схема зонування населеного пункту М1:5000
10. Перелік додаткових розділів та графічних матеріалів, або додаткові вимоги до змісту окремих розділів чи графічних матеріалів.	1. Виготовити план зонування території у складі генерального плану населеного пункту 2. Окремим томом виконати розділ «Інженерно-технічних заходів цивільного захисту (цивільної оборони)» на особливий період виконати, згідно окремого завдання на проектування, з врахуванням рішень затверджених відповідних розділів проектів (схем) районного планування.
11. Особливі вимоги до забудови, інженерного обладнання, організації транспорту, пішоходів	1. Висотність забудови не повинна перевищувати 1 - 4 поверхи. 2. Переважним видом забудови прийняти садибну, з ділянками 0,15-0,1га, в тому числі. 3. Надати пропозиції щодо розвитку внутрішньої мережі вулиць. 4. Надати пропозиції щодо охоронних та захисних зон з врахуванням містобудівних чинників. 5. Надати пропозиції щодо централізованого водопостачання для всієї забудови населеного пункту. Розмістити вузол водопідготовки. 6. Надати пропозиції щодо централізованої каналізації для всієї забудови населеного пункту. 7. Передбачити резервування території під розміщення об'єктів культурно-побутового обслуговування населення, розміщення об'єктів торговельної інфраструктури. 8. Приділити особливу увагу межі зон охорони пам'яток культурної спадщини в обов'язковому порядку нанести на основний кресленик генерального плану села, земельні ділянки що містять пам'ятку місцевого та національного значення. 9. Передбачити зелені і паркові зони; 10. Передбачити спортивно-ігрові майданчики;
12. Вимоги щодо врахування державних інтересів	Зазначити згідно умов від центрального органу виконавчої влади, що забезпечує формування державної політики у сфері містобудування та архітектури.
13. Вимоги щодо розрахунків на першу чергу реалізації	На першу чергу реалізації генерального плану передбачити включення до території селища Сонячне прилеглих зон житлової та промислової забудови, що встановлені органами державного земельного кадастру та надати пропозиції щодо

	комплексного благоустрою цих територій.
14. Додаткові вимоги.	На підставі затвердженого Генерального плану населеного пункту та плану Зонування території подальшими етапами розробки містобудівної документації на місцевому рівні є «Детальні плани територій».
15. Кількість додаткових екземплярів графічних та текстових матеріалів.	Матеріали проектної документації виконати у 3-х примірниках, з яких – один примірник матеріалів проектної документації – для передачі відділу містобудування, архітектури та житлово-комунального господарства Запорізької райдержадміністрації, та на магнітних носіях. Для текстових матеріалів -.pdf, графічних -.tiff,
16. Основні вимоги до програмного забезпечення, в тому числі геоінформаційних систем та технологій	Для Замовника: для текстових матеріалів - <i>Adobe (Acrobat) Reader</i> . -для графічних - <i>Microsoft Windows Photo Viewer</i> , <i>Adobe Illustrator</i> , <i>other image viewer</i> . Для розробника: <i>OpenOffice</i> , <i>AutoCad</i> , <i>ArcGIS</i> , або <i>Digital</i> s

Головний архітектор проекту



Прудка І.А.



УКРАЇНА

ЗАПОРІЗЬКА ОБЛАСНА ДЕРЖАВНА АДМІНІСТРАЦІЯ

пр. Соборний, 164, м. Запоріжжя, 69107, тел/факс: (061) 224-63-81
E-mail: adm@zoda.gov.ua; www.zoda.gov.ua Код ЄДРПОУ 00022504

17.01.2018

№ 11165/08-24

На № 01-48/1562 від 11.12.2017

Широківському сільському голові

Коротенку Д.О.

вул. Центральна, 1, с. Широке,
Запорізький район, 70413

Про визначення та врахування
державних та регіональних
інтересів під час розроблення
генерального плану
селища Сонячне

Шановний Денисе Олександровичу!


Обласна державна адміністрація розглянула лист Широківської сільської ради Запорізького району Запорізької області від 11.12.2017 № 01-48/1562 щодо визначення державних та регіональних інтересів при розробленні містобудівної документації «Генеральний план селища Сонячне Запорізького району Запорізької області. Оновлення з розширенням меж населеного пункту та План зонування селища Сонячне Запорізького району Запорізької області (у складі Генерального плану)» та повідомляє про таке.

Відповідно до планувальних рішень Схеми планування території Запорізької області, яка затверджена рішенням Запорізької обласної ради від 29.12.2011 № 4, територія селища Сонячне за функціональним зонуванням відноситься до території з пріоритетним розвитком високотехнологічних галузей промисловості та окремих метрополітарних (фінанси, наука, виставкова діяльність тощо) видів діяльності та до Північної (Запорізької) підзони урбанізації - з критичним рівнем виробничо-містобудівного освоєння території.

На території рекомендується жорстке регулювання містобудівного розвитку з першочерговою реструктуризацією економічної бази та екологічною реабілітацією території.

Відповідно до аналізу рівня соціально-економічного розвитку окремих таксонів Запорізької області Запорізький район відноситься до 3 типу таксонів із середнім показником потенціалу та середнім рівнем соціально-економічного та містобудівного розвитку. Перспективи розвитку району цього типу пов'язано із використанням його переваг транспортно-географічного положення.

В районі планується розвиток багатоступеневої системи громадського обслуговування населення з розміщенням підприємств повсякденного та періодичного обслуговування.

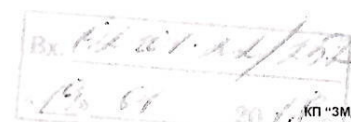

Планувальними рішеннями Схеми планування території Запорізької області на території селища Сонячне передбачено:

- зона впливу автомобільного транспортного коридору Європа-Азія;
- будівництво альтернативної національної дороги;
- будівництво транспортної розв'язки в різних рівнях;
- будівництво автостоянки для відстою вантажного транспорт.

Необхідно виконати роботи з розробки розділу «Інженерно-технічні заходи цивільного захисту» (далі – ІТЗ ЦЗ), який є складовою частиною містобудівної документації (схеми планування території або генерального плану). Головним завданням розділу ІТЗ ЦЗ при плануванні території є створення містобудівних умов, забезпечення захисту населення і територій від надзвичайних ситуацій техногенного та природного характеру, їх наслідків з урахуванням особливостей соціально-економічного розвитку та природно-кліматичних умов. Розділ розробити згідно ДБН Б.1.1-5:2007 Склад, зміст, порядок розроблення, погодження та затвердження розділу інженерно-технічних заходів цивільного захисту (цивільної оборони) у містобудівній документації (перша та друга частини), де визначити конкретні рішення щодо забезпечення захисту населення і територій від надзвичайних ситуацій техногенного і природного характеру та їх наслідків.

При розробленні містобудівної документації необхідно врахувати розташування ландшафтного заказника місцевого значення – «Балка Хуторська» та ботанічного заказника місцевого значення – «Цілинна Ділянка» та ст. 59 Закону України «Про охорону навколишнього природного середовища», п. «г» ст. 32 Закону України «Про відходи», ст. 87, 88, 89 Водного кодексу України, ст. 60, 61 Земельного кодексу України.

В околицях селища Сонячне Запорізького району знаходяться пам'ятки археології місцевого значення:

1. Курганний могильник «Могила Розкопана» з 8 курганів, охоронний № 2335, розташований за 0,5 км на південний схід від південної околиці с. Дніпрельстан, Широківської сільради та за 1,7 км на північний схід від північної околиці с-ща Сонячне, за 0,1 км на північний схід від північної околиці дачного кооперативу «Сонячний-2».

2. Курганний могильник з 7 курганів, охоронний № 2215, розташований за 6,5 км на схід від східної околиці с. Ручаївка Широківської сільради та за 1,1 км на південний захід від південно-західної околиці с-ща Сонячне.

3. Курган, охоронний № 2214, розташований за 4,5 км на схід від північно-східної околиці с. Ручаївка Широківської сільради та за 2,8 км на захід від західної околиці с-ща Сонячне.

4. Курганний могильник з 3 курганів, охоронний № 2213, розташований за 4,3 км на схід від південно-східної околиці с. Ручаївка Широківської сільради та за 3,0 км на південний захід від західної околиці с-ща Сонячне.

5. Курганний могильник з 9 курганів, охоронний № 2351, розташований за 1,5 км на південь від південної околиці с. Малишівка Широківської сільради та за 2,1 км на північ від північної околиці с-ща Сонячне.

6. Курганний могильник з 2 курганів, охоронний № 2349, розташований за 3,0-3,8 км на південь від західної околиці с. Малишівка Широківської сільради та за 0,5-0,6 км на захід - північний захід від північно-західної околиці с-ща Сонячне. Запорізької обласної ради народних депутатів №434 від 26.11.1985.

7. Курган, охоронний № 2350, розташований за 1,7 км на південь від західної околиці села с. Малинівка Широківської сільради та за 2,4 км на північний захід від північної околиці с-ща Сонячне.

Зазначені пам'ятки археології внесені до Списку пам'яток історії та культури Запорізької області рішенням виконкому Запорізької обласної ради народних депутатів № 434 від 26.11.1985.

Під час виконання робіт з розробки містобудівної документації «Генеральний план селища Сонячне Запорізького району Запорізької області. Оновлення з розширенням меж населеного пункту та План зонування селища Сонячне Запорізького району Запорізької області (у складі Генерального плану)» необхідним є врахування та дотримання вимог Законів України «Про охорону культурної спадщини» і «Про охорону археологічної спадщини».

Примірники креслень графічних матеріалів містобудівної документації на оптичних дисках повинні бути виконані у форматі геоінформаційних систем, що підтримують об'єктне представлення геопросторових даних.

Профільні геопросторові дані не пізніше 30 робочих днів після затвердження містобудівної документації повинні бути внесені до містобудівного кадастру Запорізького району. У разі не створення містобудівного кадастру Запорізького району, на час затвердження містобудівної документації місцевого рівня, зазначені матеріали повинні бути передані до Управління містобудування та архітектури облдержадміністрації та до відділу містобудування, архітектури та житлово-комунального господарства Запорізької райдержадміністрації.

Обласна державна адміністрація просить Вас врахувати державні та регіональні інтереси під час виконання робіт з розробки містобудівної документації «Генеральний план селища Сонячне Запорізького району Запорізької області. Оновлення з розширенням меж населеного пункту та План зонування селища Сонячне Запорізького району Запорізької області (у складі Генерального плану)».

З повагою

заступник голови – керівник апарату
обласної державної адміністрації



З.М. Бойко



УКРАЇНА

**ШИРОКІВСЬКА СІЛЬСЬКА РАДА
ЗАПОРІЗЬКОГО РАЙОНУ ЗАПОРІЗЬКОЇ ОБЛАСТІ**

юридична адреса: 70413, Запорізька область, Запорізький район, село Широке,
вулиця Центральна, 1

адреса фактичного місця розташування: 69089 місто Запоріжжя,
вулиця Героїв 37 батальйону, 137

для листування: 69089, місто Запоріжжя, а/с 5586

телефон +38 (061) 279-31-37, телефон (факс) +38 (061) 223-62-10

e.mail: shyroke.otg@gmail.com

ЄДРПОУ 26013402

Вих. № 01-49/134 від 25.04.2018 року
На. вих. № _____ від _____

ФОП Прудка І.А.
пров. Вантажний, 13
м. Запоріжжя

«Про надання вихідних даних»

Для виконання генерального плану по об'єкту: «Генеральний план селища Сонячне Запорізького району Запорізької області. Оновлення з розширенням меж населеного пункту та План зонування селища Сонячне Запорізького району Запорізької області (у складі Генерального плану)», надаємо Вам таблицю вихідних даних по селищу Сонячне Запорізького району.

Додаток: на 5-ти аркушах.

Секретар Широківської сільської ради

О.А. Правдюк

Виконавець:
Ковтун І.А.
286-21-31

Для розробки генеральних планів з зонінгом необхідні наступні вихідні дані по трьом додаткам:

Додаток 1

Найважливіші дані населеного пункту.

1. - Загальна площа населеного пункту, 223,20 га
 - Загальна площа житлового фонду, га
 - Кількість садиб та багатоквартирних будинків з приведенням їх загальної площі та м.кв.
Всього – 352 одиниці загальною площею – 50298 м², житлова площа – 23712 м²
Однокімнатні – 56 одиниць загальна площа – 2423 м²
Двокімнатні – 85 одиниць загальна площа – 5251 м²
Трикімнатні – 80 одиниць загальна площа – 8498 м²
Чотирикімнатні – 51 одиниця загальна площа – 11496 м²
П'ятикімнатні – 39 одиниць загальна площа – 10123 м²
Шестикімнатні – 43 одиниці загальна площа – 12507 м²
Багатоповерхових будинків – 2 од. (загальна площа – м²)
П'ятиповерховий будинок вулиця Інститутська – 2126,9 м²
П'ятиповерховий будинок вулиця Весняна – 2704,8 м²
 - Загальна кількість населення на 01.01.2017 р. – 915 од. у т.ч. дорослих – 640 од., пенсіонерів – 107 од., дітей дошкільного віку – 59 од. та школярів – 109 од..
Інформація численності населення (10 років тому)
 - Найголовніші промислові підприємства та їх потужність - відсутні
 - Наявність резервних територій в межах населеного пункту під можливий розвиток промисловості та житлового будівництва, їх площа, га.
2. Копії проекту та пояснювальна записка на водовідведення та пониження ґрунтових вод села (вказати розробника проекту). Газопостачання, електропостачання
3. Перелік потенційно небезпечних та хімічно – небезпечних об'єктів (при наявності) маючи на увазі, що даний перелік щорічно обновлюється Головним Управлінням ДСНС України у Запорізькій області, затверджений рішенням обласної комісії з питань ТЄБ та НС, по населеному пункту. **(ДОДАЄТЬЯ)**
Перелік потенційно – небезпечних об'єктів розташованих на території села щорічно обновлюваний Головним Управлінням ДСНС України у

Запорізькій області, затверджений рішенням обласної комісії з питань ТЄБ та НС, по населеному пункту.

4. Перелік збірних евакопунктів та наявність найпростіших укриттів (підвали, погрібники), які можуть забезпечити захист населення.
5. Пам'ятники археології, історії, архітектури, природи, ландшафтних особистостей, Великої вітчизняної війни з короткою характеристикою. Пропозиції до узаконення таких пам'ятників при їх наявності. (Кургани за межами населеного пункту)

Додаток 2

Будинки та споруди громадського призначення.

Надати перелік будинків та споруд громадського призначення на території населеного пункту по наявності, а саме:

1. Школи загальноосвітні (фактична кількість місць) (розрахункова кількість) – **відсутні**
2. Школи музичні та спеціалізовані (фактична кількість місць) - відсутні:
3. Школи початкові (фактична кількість місць) - **відсутні**
4. Дитячі садочки (кількість дітей) (кількість садочків, розрахункова чисельність, фактична чисельність) - **відсутні**
5. Училища (фактична та розрахункова кількість місць) - **відсутні**
6. Лікарні, амбулаторії (ФАП), швидка допомога (кількість пацієнтів на добу та ліжко/ місць): амбулаторія загальної практики сімейної медицини, прийом на добу – дорослих, дітей – **відсутні**
7. Готелі (кількість місць) – **відсутні**
8. Будинки культури (кількість місць)
- будинок народної творчості та дозвілля – місць – **відсутні**
9. Крамниці продтоварів

№	Назва магазину	Загальна площа	Торгівельна площа
1.	ФОП Хижняк Г.В.	196,3	51,2
2	ТОВ «ВОГ РІТЕЙЛ»	120,0	46,6

10. Крамниці промтоварів (торгівельна площа, м.кв.)

№	Назва магазину	Загальна площа	Торгівельна площа
1.	Відсутні	-//-/-	-//-/-

11. Кафе, ресторани (кількість місць)

12. Розважальні центри (кількість місць) - **відсутні**
13. Окремі бібліотеки – **відсутні**
14. Клуби дитячих розваг (кількість місць) - **відсутні**
15. Пожарні депо (кількість машин) - **відсутні**
16. Дитячі та спортивні майданчики (площа , м.кв) – **наявні**
17. Стадіони (кількість місць, площа, га) **відсутні**

Дитячий майданчик:

Сел. Сонячне, вулиця Весняна, 1

Площа – 550,70 м2

Загально технічний стан – задовільний

Спортивний майданчик:

Сел. Сонячне, вулиця Весняна, 1

Площа – 275,36 м2

Загально технічний стан – задовільний

По кожному окремому об'єкту вказати:

- Його місце розташування (адресу)
- Розрахункову потужність
- Фактичну наявність
- Коротко загальний технічний стан

Адмінбудівля Інституту Олійних культур в межах селища Сонячне

Орієнтована площа площею 3,8502 га

площею 7,6788 га

площею 3,0722 га

площею 1,6400 га

(Державний акт на право постійного користування землею ІІ-ЗП №002385, зареєстрований в Книзі записів державних актів на право постійного користування землею 27.05.2004 за №5)

Технічні характеристики існуючих інженерних мереж та споруд з Вашими пропозиціями по їх удосконаленню і розвитку у населеному пункті.


1. Електропостачання. Схема, місце підключення та джерело зовнішнього підключення. Кількість та потужність існуючих розподільчих підстанцій, кількість та потужність трансформаторних підстанцій, Діюче електричне навантаження. Наявність резерву потужності кВт/добу. Довжина електромереж (в межах села) 35 кВ, 10 кВ, 0,4 кВ. Кількість РП, трасування повітряних та кабельних мереж.
2. Водопостачання. Схема, місце підключення та джерело водопостачання. Потужність м³/добу. Водоспоживання окремо підприємствами та житловим фондом м³/добу. Магістральні мережі (довжина, матеріал, діаметр, тиск, технічний стан). Наявність, кількість, потужність насосних станцій, очисних споруд. Кількість та місце розташування пожарних гідрантів, пожежрезервуарів та їх об'єм. (Що до пропозиції удосконалення?) Рівень забезпечення споживачів – м³/добу.
3. Каналізування. Схема, система каналізації (господарсько – фекальної). Наявність та тип очисних споруд, їх потужність, місце розташування, злив очищених стоків. Фактична загрузка та ефективність роботи. Кількість та місце розташування насосних станцій (вказати якщо само стічна). Довжина каналізаційних мереж, матеріал, діаметр, технічний стан. Перелік локальних споруд (при наявності). Куди підключена каналізація? (Що до пропозиції удосконалення?) Рівень забезпечення споживачів – м³/добу.
4. Теплопостачання. Схема. Кількість котелень їх загальна потужність (ГКкал), паливо, кількість споживачів та їх забезпечення (ГКкал). Місце розташування котелень, трасування та довжина тепломереж, матеріал, діаметр, робочий тиск, технічний стан.
5. Газопостачання. Схема. Місце підключення. Джерело газопостачання, кількість та місце розташування ГРС, ГРП, ШРП. Потужність, загальне споживання газу по селу. Наявний резерв на розвиток споживачів. Споживання та резерв газу по промисловим підприємствам, окремо кожному.
6. Телефонізація та радіофікація. Схема. Розташування та потужність (кількість абонентів) сільської АТС. При наявності

довжина зовнішніх мереж зв'язку, розташування розподільчих шаф. Резерв потужності на підключення нових абонентів.

7. Громадська оборона. Схема. Кількість, місце розташування, потужність та обладнання життєво необхідними умовами протирадіаційних укриттів для населення. Загальна чисельність промислово – виробничого персоналу у мирний час та в особливий період. Кількість та потужність евакопунктів (їх адреси).

Засоби сигналізації та оповіщення населення на особливий стан узгоджений з МНС. Технічний устрій, розташування, наявність наказу на закріплення відповідальних осіб.


8. Ферми КРС, у тому числі за межами населеного пункту, кількість худоби, функціонують чи ні? – **відсутні**

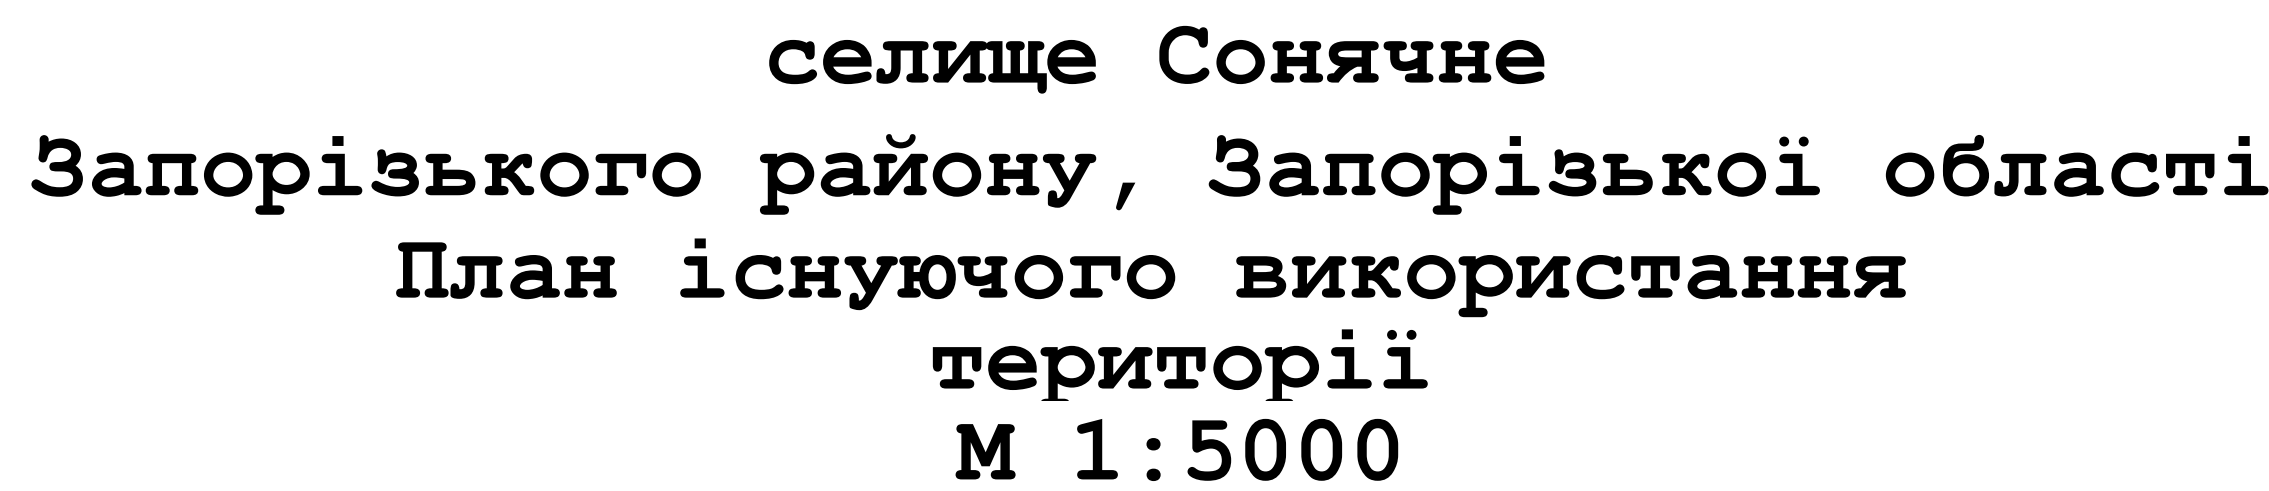

Умовні позначення		
Існуючі	Проект	Найменування
---		Межа населеного пункту
		Межі землевидоєднання
		Територія житлової садибної забудови
		Територія сільськогосподарського призначення
		Територія житлової багатоквартирної забудови
		Територія громадської забудови
		Територія інженерної інфраструктури
		Територія комунальних об'єктів
		Територія рекреаційного призначення
		Територія зелених насаджень спеціального призначення
		Територія зелених насаджень загального користування
		Житловий будинок
		Виробнича будівля (спокладу)
		Громадська будівля
		A3C
		Авто-газоопалювальна компресорна станція
		Залізниця
		Комплектна трансформаторна підстанція (КТТ)
		Газорозподільний пункт (ГРП, ШРП)




						11/2017
						Г енеральний план селища Сонечне Запорізького району Запорізької області. Оновлення і розширення меж населеного пункту та плану хуторів селища Сонечне Запорізького району Запорізької області (у складі генерального плану)
Витн.	Клас.	Арх.	Дк. док.	Плп.	Дат	
						Завоювн. Широкоме́ська сільська рада
ГАП	Пруда					Станн. ГП
Перевірн.						Арху
Розроблн.	Пруда					2
						Арху
						0
						План інженерного використання території М-1:2000
						ФАП Пруда ІА

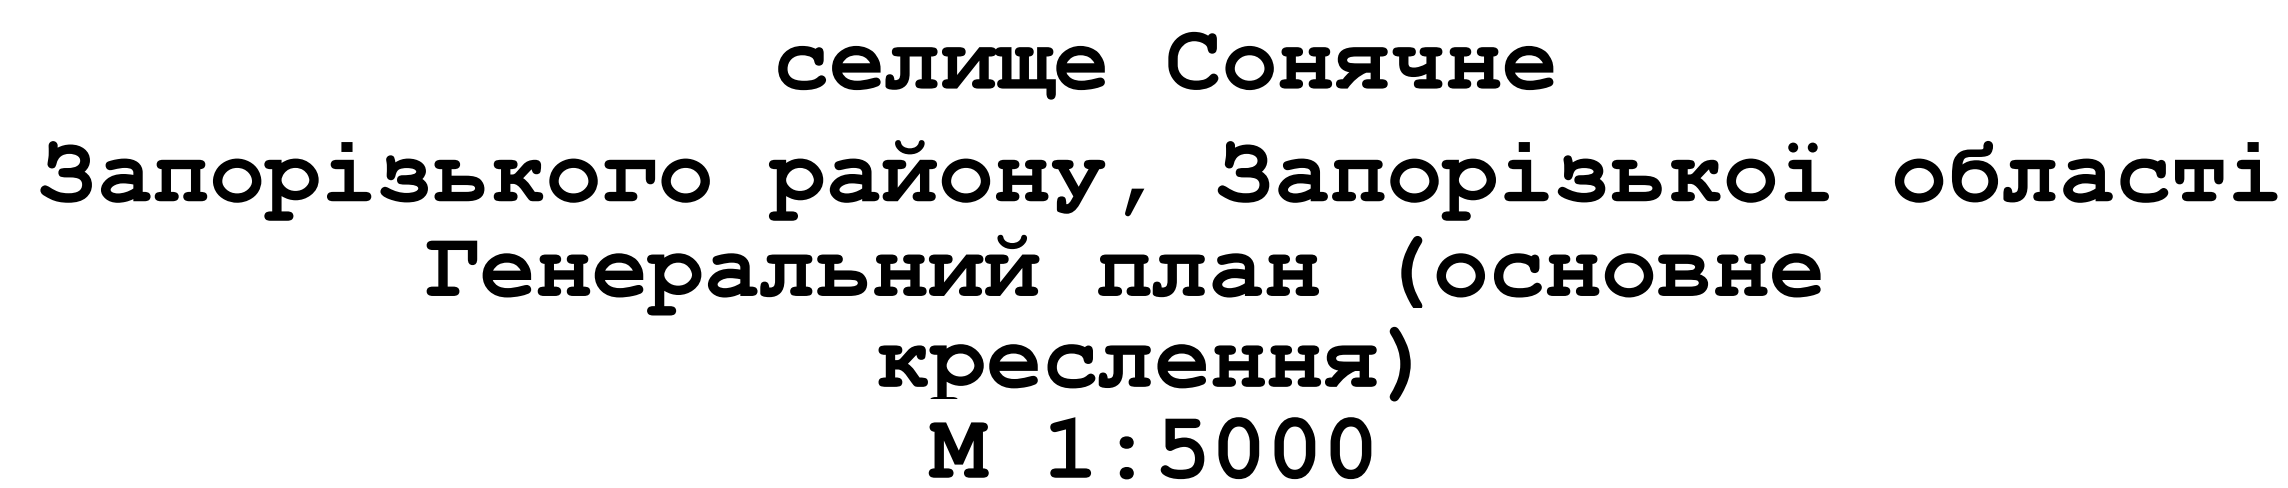

№ п/п	Найменування	Примітка
1	Інститут опійних культур НААН України	Існ.
2	Центр ПМД Широкоівської ОТГ	Проект
3	Адміністративна будівля	Проект
4	Спортивний майданчик (футбольне поле з штучним покриттям)	Проект
5	Спортивно-оздоровчий комплекс	Проект
6	Спортивно-оздоровчий центр	Проект
7	Карантинний розсадник рослин	Існ.
8	Відоме житло	Проект
9	Складські приміщення СЗЗ 50 м.	Проект
10	Ботанічний заказник "Ділина балка"	Існ.
11	Електрична підстанція ОЗ 3 м.	Існ.
12	Базеофункціональний торгівельно-виставковий та логістичний комплекс	Проект
13	Школа	Проект
14	Дитячий садок	Проект
15	Церква	Існ.
16	Гаражні кооперативи	Існ.
17	Склади промтоварів СЗЗ 50 м.	Існ.
18	Парк	Проект
19	Насосна станція	Проект
20	Газові модулі СЗЗ 100 м.	Існ.
21	Торгов. виставкової та логістичні центри	Проект
22	Дачні кооперативи	Існ.
23	Адміністративний центр, магазин	Проект
24	Насосна станція теплових мереж СЗЗ 15 м.	Існ.
25	Автомойка СЗЗ 50 м.	Існ.
26	АЗС СЗЗ 50 м.	Існ.
27	Адміністративно - торговельний центр	Проект
28	Ландшафтний заказник "Балка Хуторська"	Існ.

Існуючі	Проект	Найменування
---	—	Межа населеного пункту
		Межі землеволодіння
		Територія житлової садибної забудови
		Територія сільськогосподарського призначення
		Територія житлової багатоквартирної забудови
		Територія громадської забудови
		Територія транспортної інфраструктури
		Територія інженерної інфраструктури
		Територія комунальних об'єктів
		Територія рекреаційного призначення
		Територія оздоровчого призначення
		Територія зелених насаджень загального користування
		Територія зелених насаджень спеціального призначення
		Межі території ПЗЗ місцевого значення
		Житловий будинок
		Виробнича будівля (споруда)
		Громадська будівля
		АЗС
		Пролод
		Червоні лінії
		Залізниця
		Комплектна трансформаторна підстанція (КТП)
		Газорозподільний пункт (ГРП, ШРП)
		Транспортні вузли з Генерального Плану м. Запоріжжя

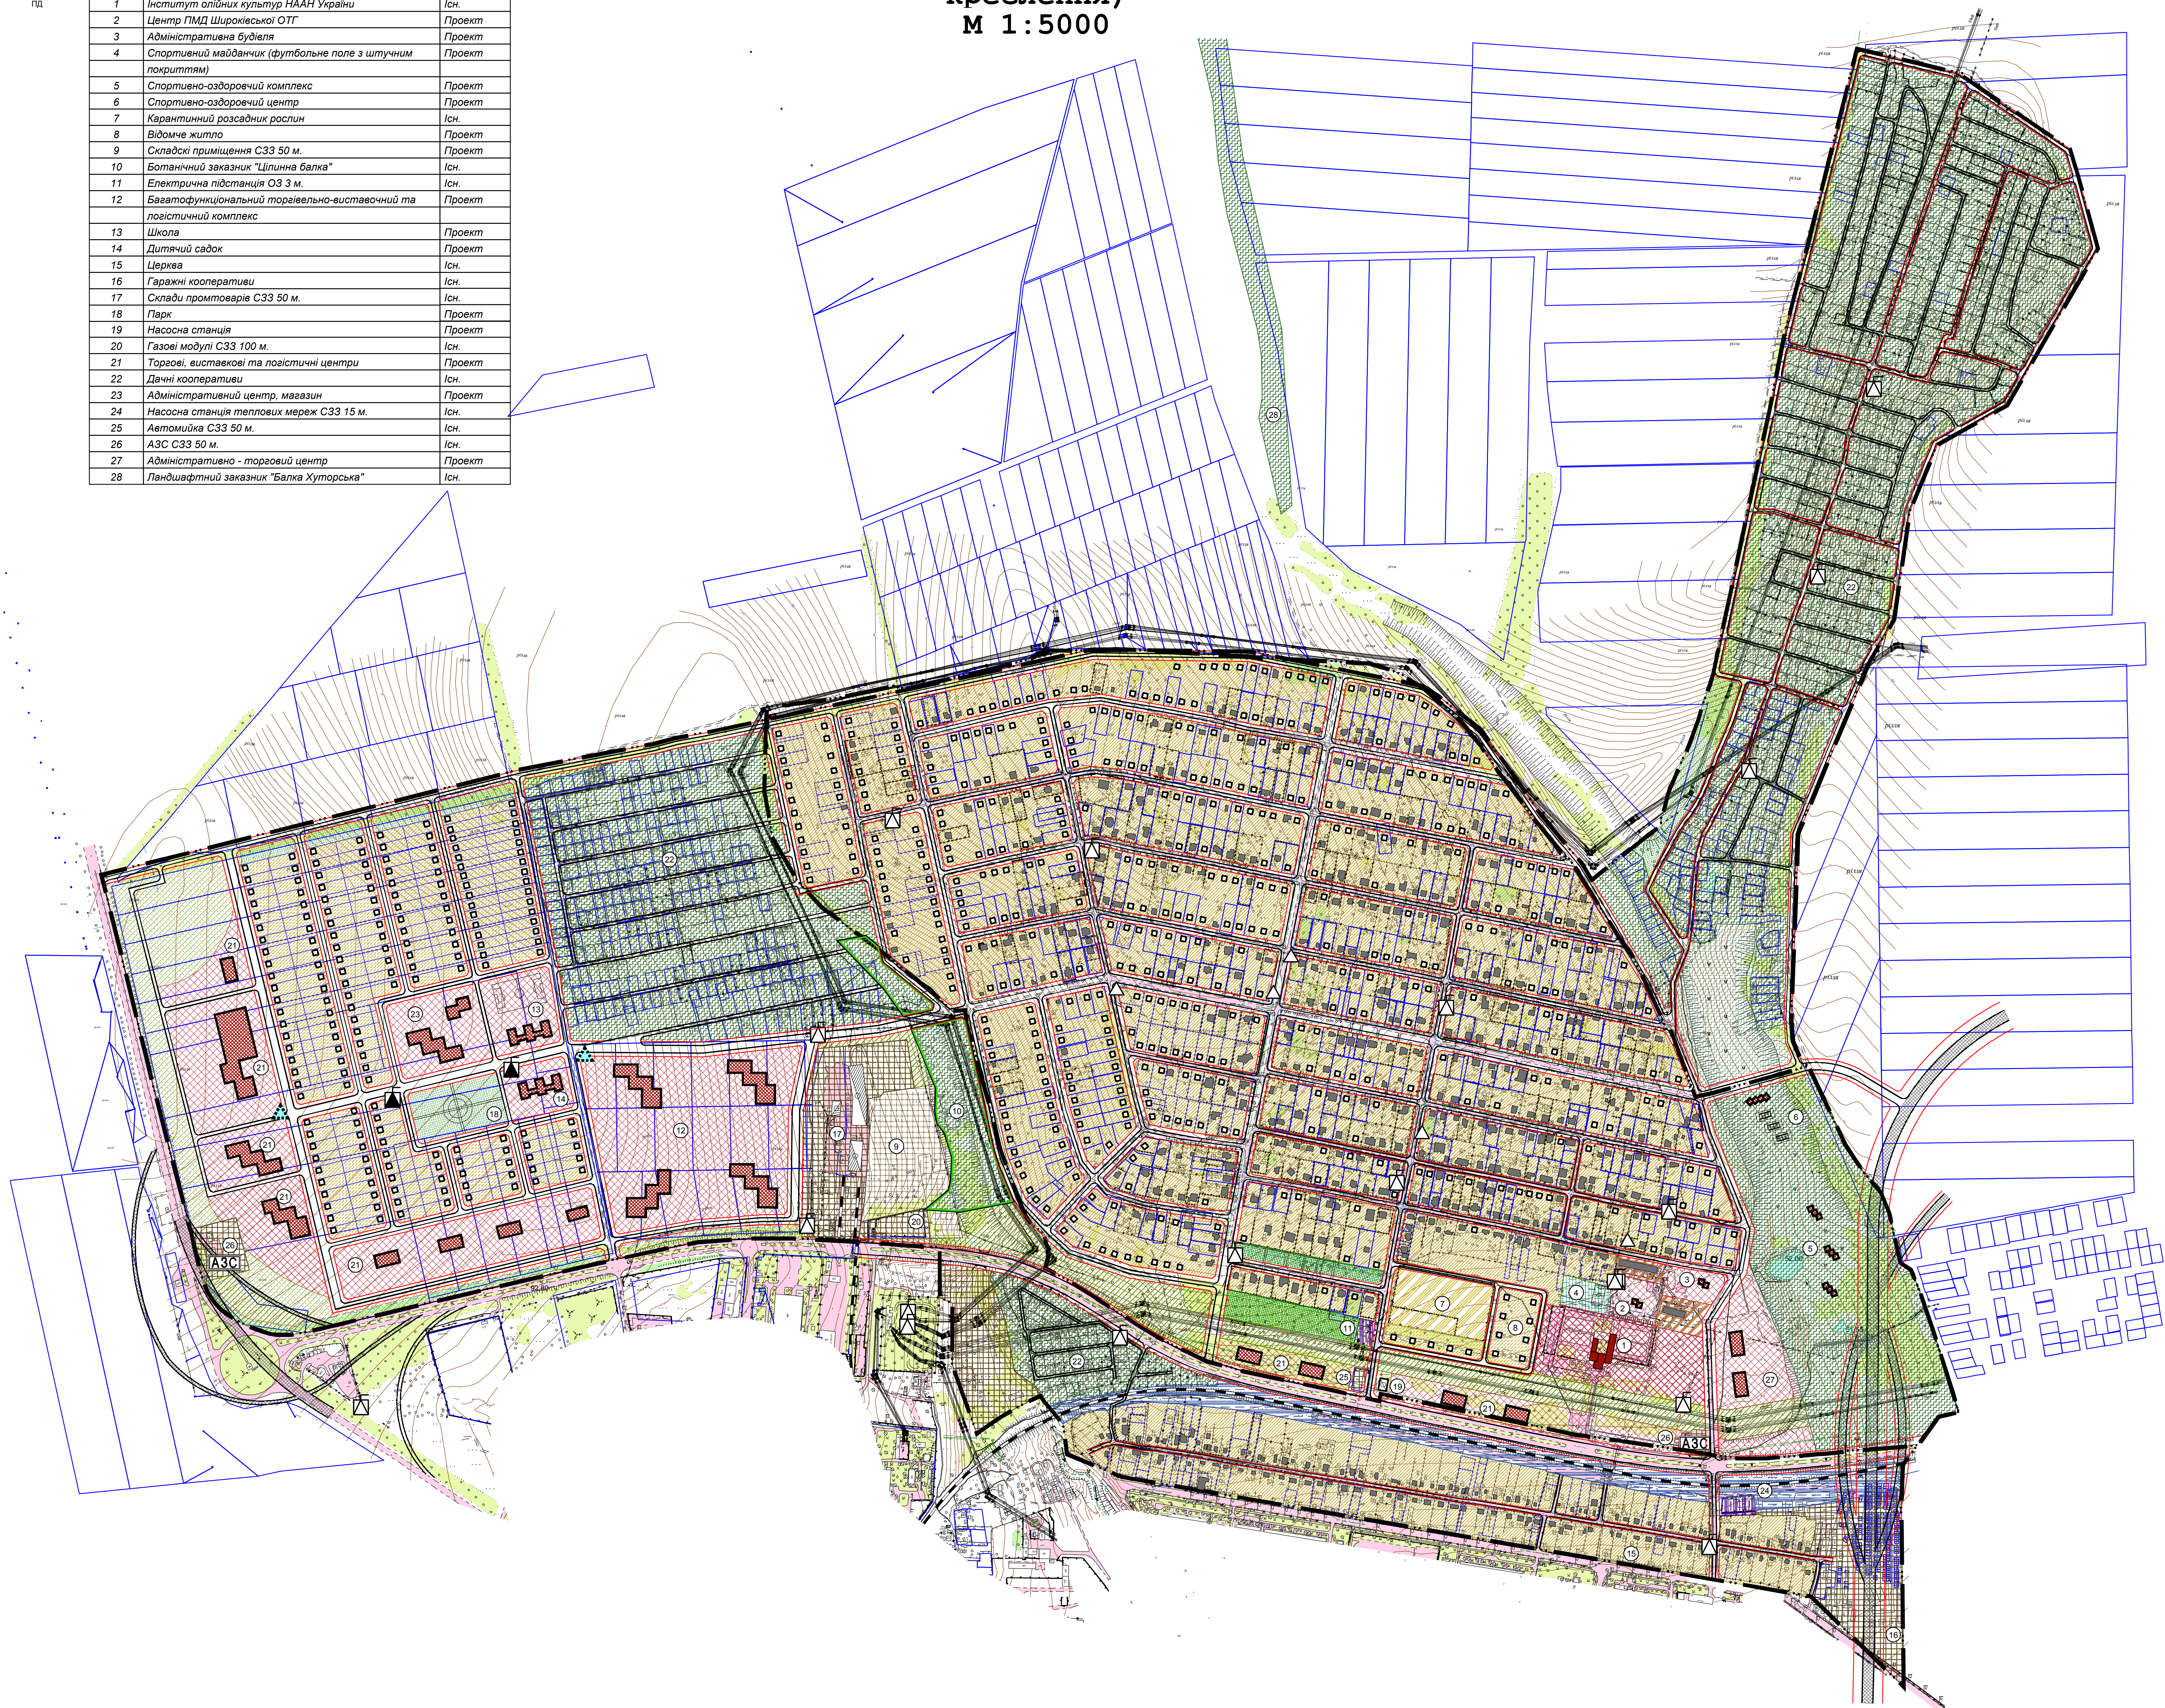

						11/7/2017
						Генеральный план селения Совхоза Запорожского району Запорожской области. Обновления и расширения мест населенного пункта та план хозяйств селения Совхоза Запорожского району Запорожской области (в соответствии с генеральным планом)
Зміст	Кінець	Арх.	№ док.	Після	Дата	
						Землюнок: Широкописьма сільська рада ГП 4 9
Г.А.П.	Пружана					
Перевірка						
Розробка	Пружана					
						М 1:5000
						©ОП Пружана І.А.



МІНІСТЕРСТВО РЕГІОНАЛЬНОГО РОЗВИТКУ, БУДІВНИЦТВА
ТА ЖИТЛОВО-КОМУНАЛЬНОГО ГОСПОДАРСТВА УКРАЇНИ
АТЕСТАЦІЙНА АРХІТЕКТУРНО-БУДІВЕЛЬНА КОМІСІЯ

Серія АА

№ 003280

КВАЛІФІКАЦІЙНИЙ СЕРТИФІКАТ
відповідального виконавця окремих видів робіт (послуг),
пов'язаних із створенням об'єкта архітектури

архітектор

(найменування професії)

Виданий про те, що

Прудка Ірина Анатоліївна

(прізвище, ім'я, по батькові)

пройшов(ла) професійну атестацію, що підтверджує його (її) відповідність кваліфікаційним вимогам у сфері діяльності, пов'язаної із створенням об'єктів архітектури, професійну спеціалізацію, необхідний рівень кваліфікації і знань.

Категорія: **архітектор**

Кваліфікаційний сертифікат видано згідно з рішенням Атестаційної архітектурно-будівельної комісії (далі - Комісія) від _____ № _____

(рішенням **відповідної** _____ секції Комісії
від **13.07.2016** № **8-16** _____, затвердженням президією
Комісії **14.07.2016** № **54-А** _____).

Зареєстрований у реєстрі атестованих осіб **14 липня** 20 **16** року
за № **3280** _____.

Роботи (послуги), пов'язані із створенням об'єктів архітектури, спроможність виконання яких визначено кваліфікаційним сертифікатом: _____

Розроблення містобудівної документації

Дата видачі **15 липня** 20 **16** року

Головою Атестаційної архітектурно-будівельної комісії



(підпис)

Білоус Сергій Ярославович

(прізвище, ім'я, по батькові)