
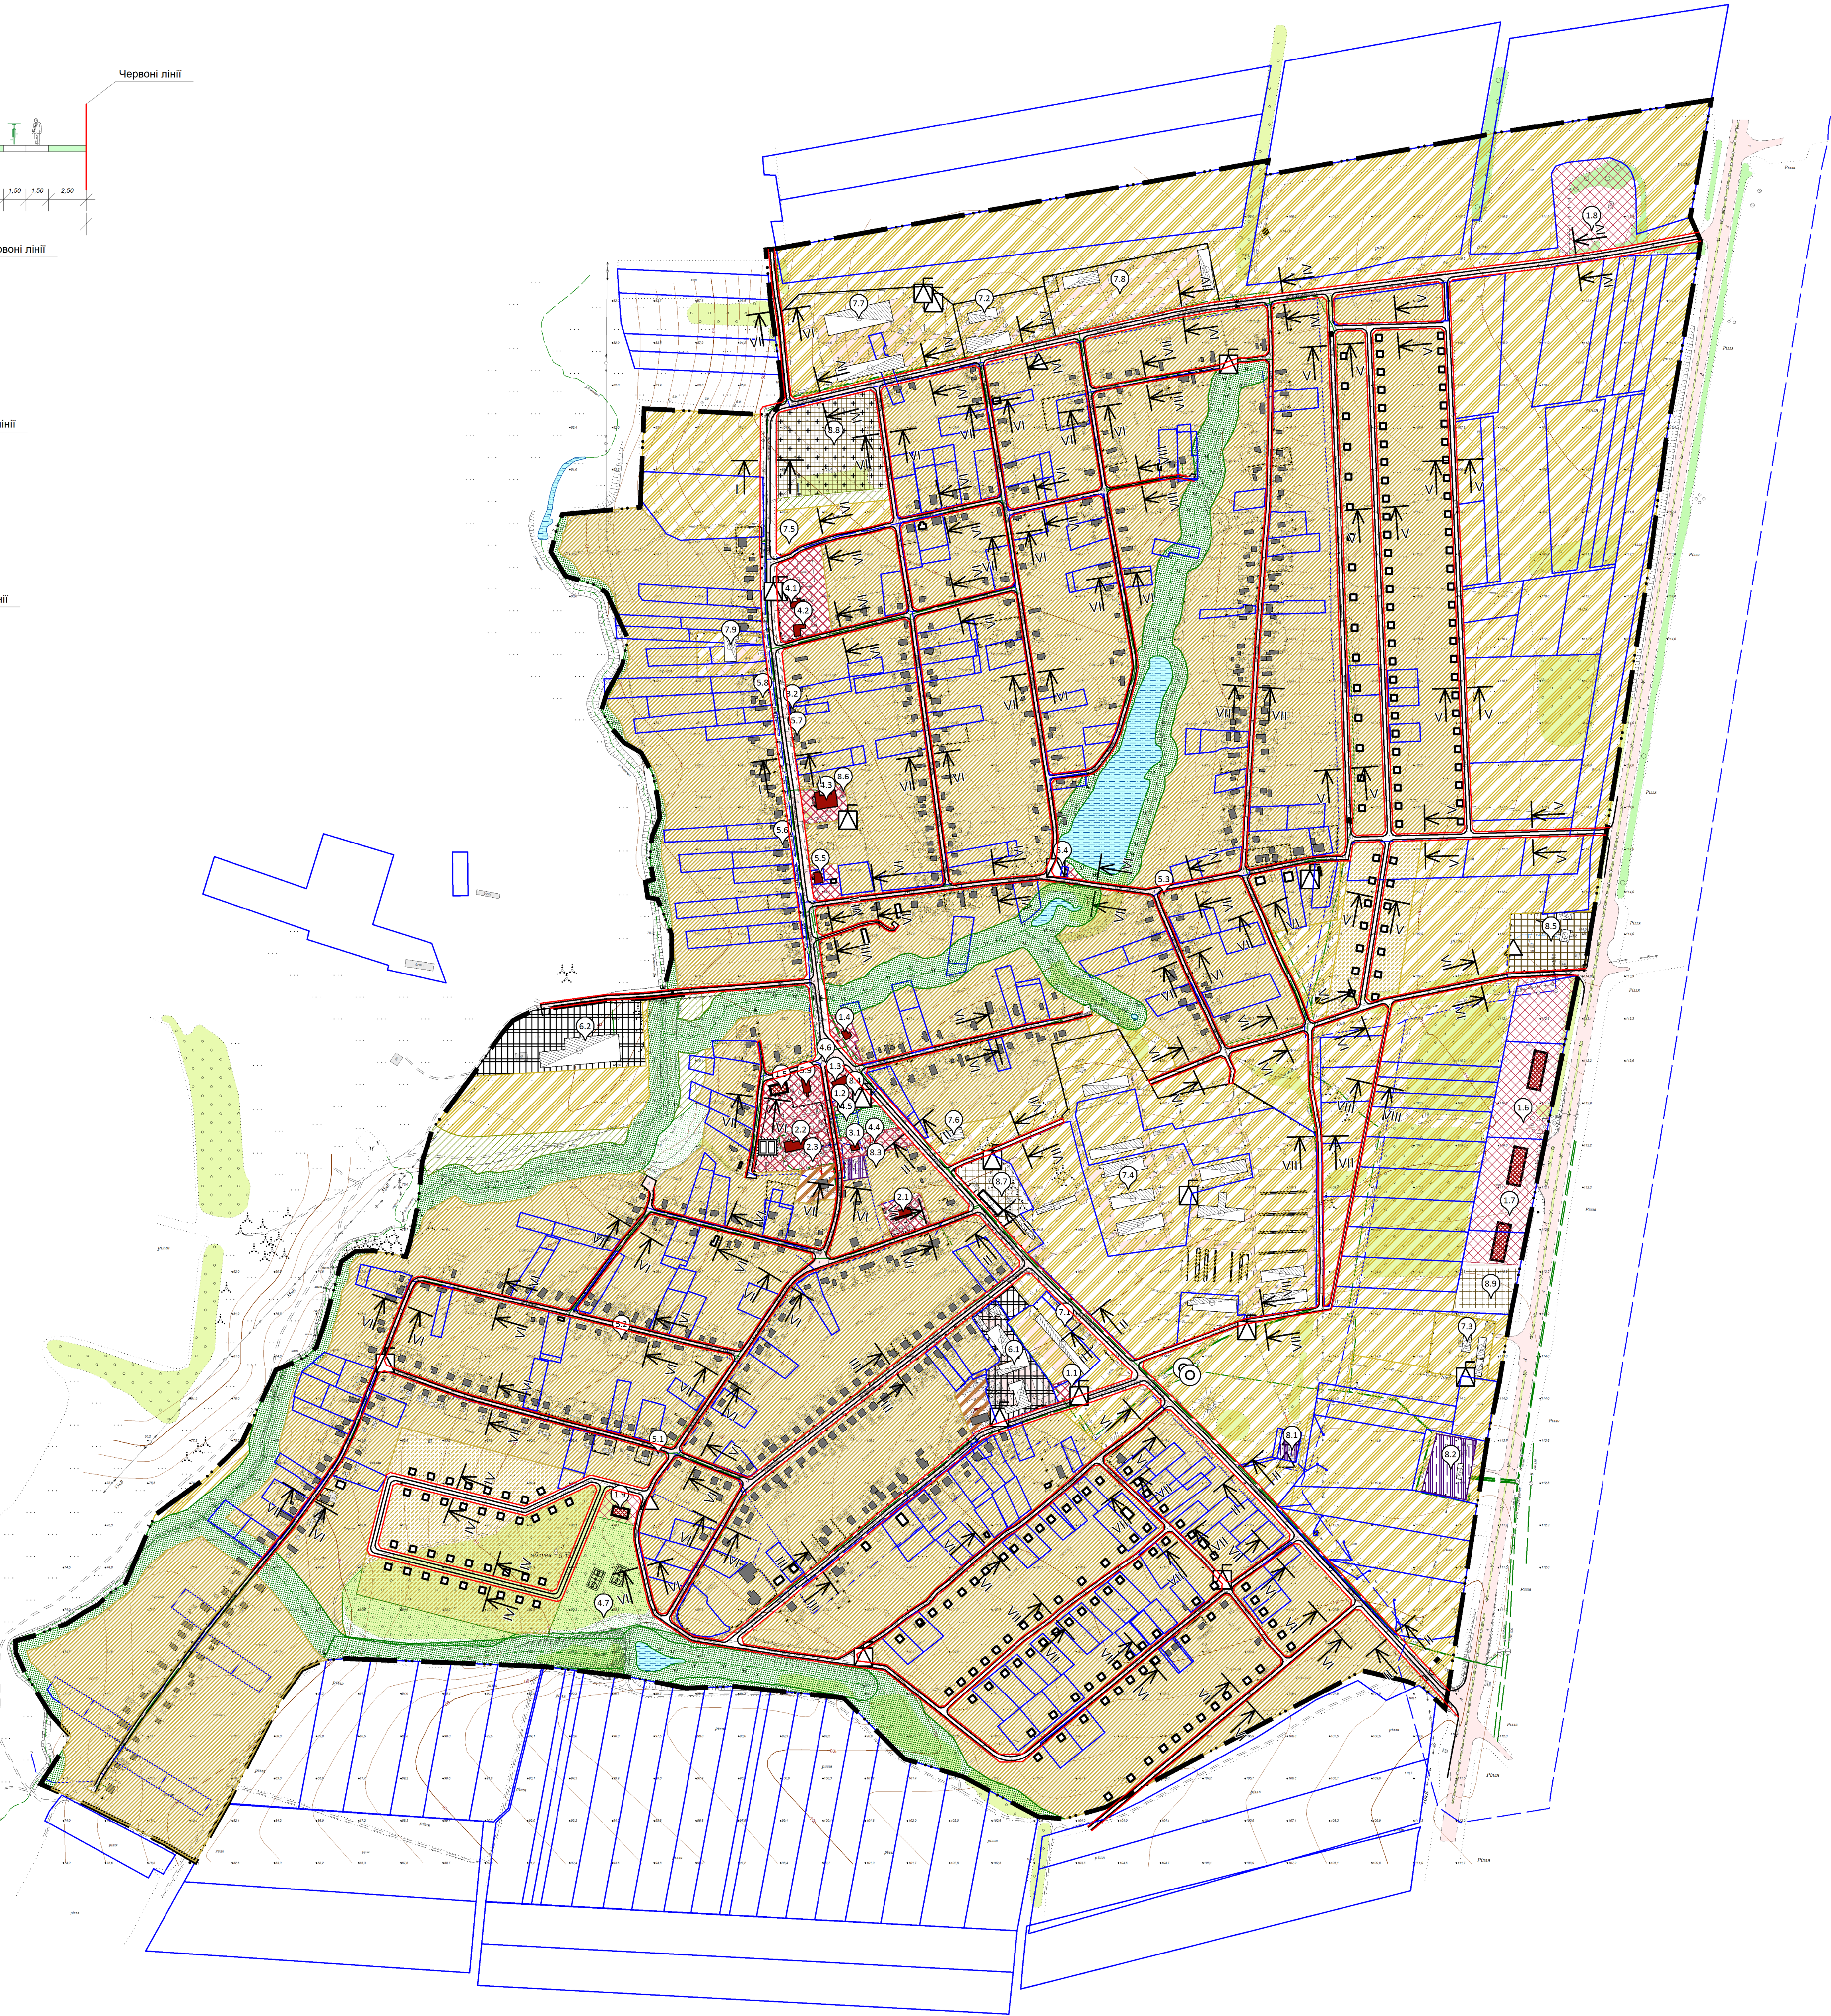
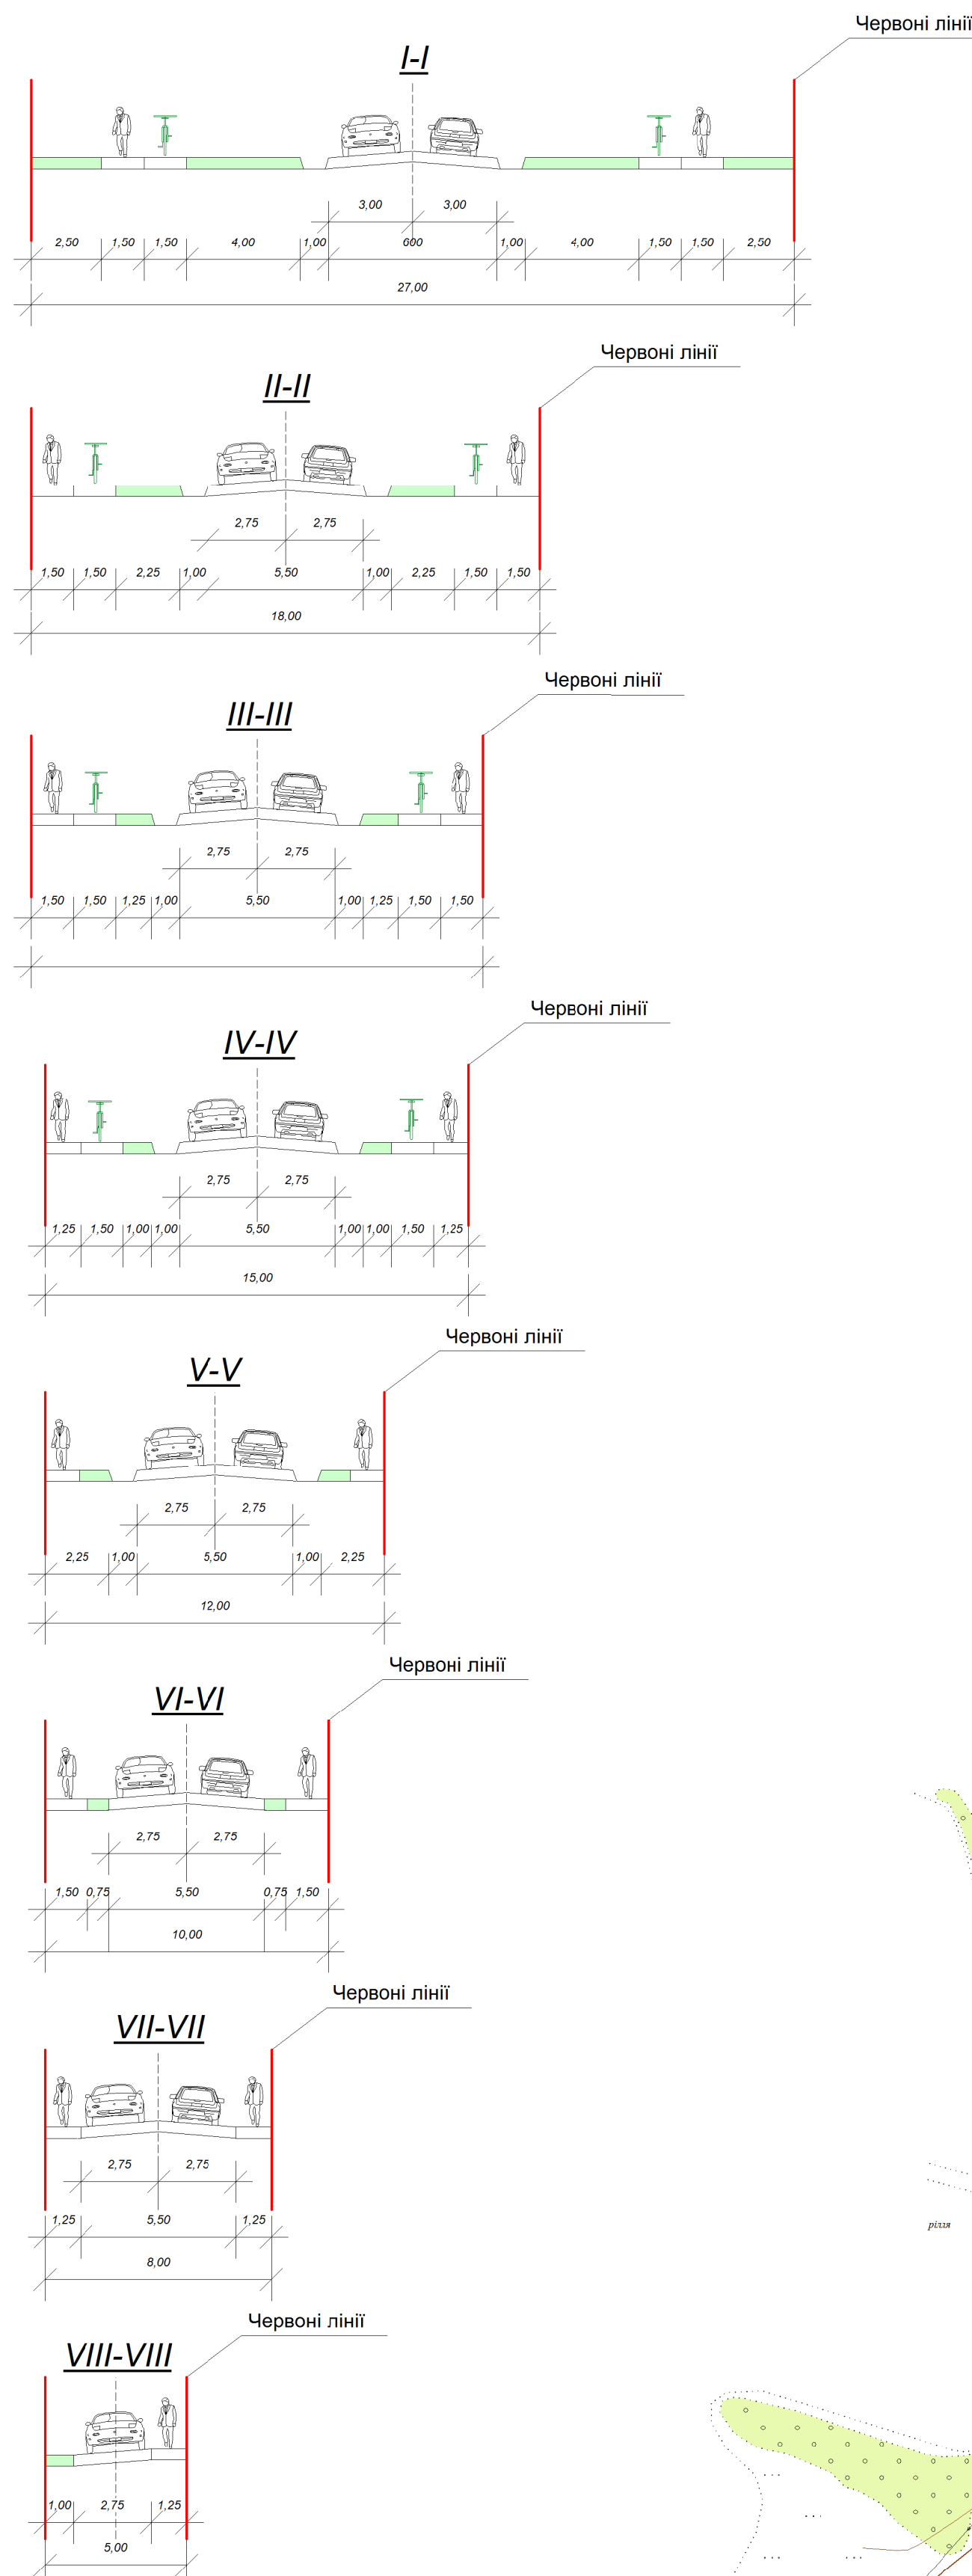


село Лукашеве
Запорізького району, Запорізької області

Схема вулично - дорожньої мережі,
міського (сільського) та
зовнішнього транспорту
1:5000

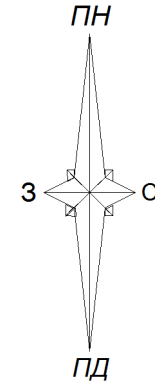

Умовні позначення		
Існуючі	Проект	Найменування
	—	Межа населеного пункту
		Об'єкти Державного земельного кадастру
		Територія житлової садибної забудови
		Територія житлової багатоквартирної забудови
		Територія сільськогосподарського призначення
		Територія громадської забудови
		Територія інженерної інфраструктури
		Територія комунальних об'єктів
		Територія виробнича
		Територія зелених насаджень загального користування
		Територія зелених насаджень спеціального призначення
		Територія кладовища
		Водний об'єкт
		Житловий будинок
		Виробнича будівля (споруда)
		Громадська будівля
		Прізд
		Червоні лінії
		Комплексна трансформаторна підстанція (КТП)
		Газорозподільний пункт (ГРП, ШРП)
		Водонапірна башта
		Пожарний резервуар

Експлікація будівель та споруд		
№ п/п	Найменування	Примітка
1.	Адміністративні та громадські установи	
1.1	Адміністративна будівля Запорізького управління водного господарства	
1.2	Адміністративна будівля	
1.3	Адміністративна будівля	
1.4	Будівля побутового обслуговування населення	Проектн.
1.5	Відділення банку, пошти	Проектн.
1.6	Торгові, виставкові будівлі, логістичний центр	Проектн.
1.7	Готель, кафе	Проектн.
1.8	Ринок сільськогосподарської продукції	Проектн.
1.9	Спортивний зал	Проектн.
2.	Учбові заклади та дитячі установи	
2.1	Дитячий садок Лукашівський НВК	
2.2	Школа Лукашівський НВК	
2.3	Спортивний майданчик	Проектн.
3.	Установи охорони здоров'я	
3.1	ФАП, приміщення для реабілітації	Реконстр.
3.2	Стоматологія	
4.	Установи культури та мистецтва, культові споруди	
4.1	Церква	
4.2	Будівля недільної школи храму	
4.3	Будинки культури з бібліотекою	
4.4	Братська могила радянських воїнів та пам'ятник воїнам - односельчанам	
4.5	Сільський парк	
4.6	Пам'ятник Шевченку Т.Г.	
4.7	Парк з спортивним та дитячим майданчиком	Проектн.
5.	Підприємства торгівлі, громадського харчування та побутового обслуговування	
5.1	Торгівельний павільйон	
5.2	Крамниця змішаної торгівлі	
5.3	Крамниця	
5.4	Торгівельний павільйон з літнім майданчиком	
5.5	Крамниця змішаної торгівлі	
5.6	Крамниця змішаної торгівлі з кафе	
5.7	Крамниця промислових товарів, кафе	
5.8	Крамниця ветеринарних та зоотоварів	
5.9	Об'єкт громадського харчування, туристичних послуг	
6.	Промислові підприємства	
6.1	Виробництво електротехнічної продукції ПП «Елтіс» СЗЗ 50 м	
6.2	Цегельний завод СЗЗ 100 м	
7.	Сільськогосподарське підприємство	
7.1	Комплекс по зберіганню зерна СЗЗ 50 м	
7.2	Комплекс по зберіганню зерна, овочів СЗЗ 50 м	
7.3	Підприємство по переробці зерна СЗЗ 100 м	
7.4	Склади сільськогосподарської продукції СЗЗ 50 м	
7.5	Територія вирощування декоративних рослин	Проектн.
7.6	Склади зберігання зерна СЗЗ 50	
7.7	Підприємство по переробці зерна СЗЗ 100 м	
7.8	Підприємство по технічному обслуговуванню та ремонту сільськогосподарської техніки СЗЗ 100 м	
7.9	Сільськогосподарське підприємство з складом, ваговою та обслуговуванню сільськогосподарської техніки СЗЗ 100 м	
8.	Комунальні заклади, склади, бази, підприємства транспорту та зв'язку	
8.1	ГРП ОЗ 10 м	
8.2	Насосна ЗСО 15 м	
8.3	ЗТП ОЗ 3 м	
8.4	Газова котельня ОЗ 10 м	
8.5	Господарські будівлі служби автомобільних доріг СЗЗ 100 м	
8.6	Вишка мобільного зв'язку	
8.7	Будівельний двір з виготовлення металевих конструкцій СЗЗ 50 м	Проектн.
8.8	Кладовище СЗЗ 100 м.	
8.9	АЗС, АГЗП СЗЗ 100 м.	Проектн.