

ФО – П Прудка І. А.

69039 м. Запоріжжя, пров. Вантажний, буд. 13  
email: 2136006@ gmail.com

Замовник:

Широківська сільська рада Запорізького району  
Запорізької області

Генеральний план села Широке Запорізького району  
Запорізької області.

Оновлення з розширенням меж населеного пункту та План  
зонування села Широке Запорізького району Запорізької  
області (у складі Генерального плану)

Пояснювальна записка до плану зонування

Шифр: 108/2018-ПЗ

ТОМ 3

Фізична особа-підприємець \_\_\_\_\_ І. А. Прудка

Головний архітектор проекту \_\_\_\_\_ І. А. Прудка

2018 р.

|               |  |  |
|---------------|--|--|
| Погоджено     |  |  |
|               |  |  |
|               |  |  |
|               |  |  |
| Зам. Інв. №   |  |  |
|               |  |  |
| Підпис і дата |  |  |
|               |  |  |
| Інв. № об.    |  |  |

| Позначення        |       | Найменування   |   | Примітка |       |
|-------------------|-------|---|---|----------|-------|
| 108/2018-З        |       | Зміст   |   |          |       |
| 108/2018-СЧ       |       | Склад проекту   |   |          |       |
| 108/2018-ПД       |       | Підтвердження ГАП   |   |          |       |
| 108/2018-ВЧ       |       | Відомості про учасників проектування   |   |          |       |
| 108/2018-ПЗ       |       | Пояснювальна записка   |   |          |       |
|                   |       | 1. Передмова   |   |          |       |
|                   |       | 2. Загальні положення. Основні терміни, зміст та призначення зонінгу   |   |          |       |
|                   |       | 3. Принципи зонування території населеного пункту   |   |          |       |
|                   |       | 4. Перелік територіальних зон, що визначаються на схемі зонування, та обґрунтування їх меж                                                                                      |   |          |       |
|                   |       | 5. Містобудівні регламенти як сукупність обов'язкових вимог до використання земельних ділянок та об'єктів нерухомості, що встановлюються у межах відповідних територіальних зон |   |          |       |
|                   |       | -Громадські зони   |   |          |       |
|                   |       | -Житлові зони   |   |          |       |
|                   |       | -Ландшафтно – рекреаційні зони   |   |          |       |
|                   |       | -Транспортної інфраструктури   |   |          |       |
|                   |       | -Інженерної інфраструктури   |   |          |       |
|                   |       | -Комунально – складські   |   |          |       |
|                   |       | -Спеціальні зони   |   |          |       |
|                   |       | -Зони сільськогосподарського призначення   |   |          |       |
|                   |       | -Інші зони   |   |          |       |
|                   |       | 6. Перелік дозволених видів забудови та іншого використання земельних ділянок у межах різних територіальних зон                                                                 |   |          |       |
|                   |       | 7. Режимы використання території, пов'язані з дією обмежень, що розповсюджуються на територію населеного пункту                                                                 |   |          |       |
|                   |       | 8. Додатки   |   |          |       |
|                   |       |   |   |          |       |
| 108/2018-З        |       |   |   |          |       |
| Зм.               | Кільк | Арк.   | № | Підпис   | Дат   |
| Розробив          |       | Прічка   |   |          | 09.18 |
| Перевірив         |       |   |   |          |       |
| ГАП               |       | Прічка   |   |          | 09.18 |
|                   |       |   |   |          |       |
| Зміст             |       |   |   |          |       |
| Стадія            |       | Аркцш   |   | Аркцші   |       |
| РП                |       | 1   |   | 1        |       |
| ФО-П Прічка І. А. |       |   |   |          |       |

Зам. Інв. №

Підпис і дата

Інв. №

| №<br>тому | Позначення  | Найменування                                                                               | Примітки                |
|-----------|-------------|--------------------------------------------------------------------------------------------|-------------------------|
|           |             | Текстові матеріали                                                                         |                         |
| 1.        | 108/2018-ПЗ | Пояснювальна записка до генерального плану                                                 |                         |
| 2.        | 108/2018-ПЗ | Основні положення генерального плану                                                       |                         |
| 3.        | 108/2018-ПЗ | Пояснювальна записка до плану зонування території                                          |                         |
| 4.        | 108/2018-ГП | Графічні матеріали                                                                         |                         |
|           | Лист 1      | Схема розташування населеного пункту в системі розселення М 1:50000                        |                         |
|           | Лист 2      | План існуючого використання території. Схема існуючих планувальних обмежень М 1:5000       |                         |
|           | Лист 3      | Генеральний план (основне креслення) Схема проектних планувальних обмежень М 1:5000        |                         |
|           | Лист 4      | Схема вулично – дорожньої мережі, міського (сільського) та зовнішнього транспорту М 1:5000 |                         |
|           | Лист 5      | Схема інженерного обладнання території М 1:5000                                            |                         |
|           | Лист 6      | Схема інженерної підготовки та захисту території М 1:5000                                  |                         |
|           | Лист 7      | План зонування території М 1:5000                                                          |                         |
|           |             | Інженерно-технічні заходи цивільного захисту (цивільної оборони)                           | У вигляді окремих томів |

|  |  |  |
|--|--|--|
|  |  |  |
|  |  |  |
|  |  |  |
|  |  |  |

Зам. Інв. №

Підпис і дата

Інв. №

|           |      |        |   |        |       |               |                   |       |        |  |  |
|-----------|------|--------|---|--------|-------|---------------|-------------------|-------|--------|--|--|
|           |      |        |   |        |       | 108/2018-СП   |                   |       |        |  |  |
|           |      |        |   |        |       |               |                   |       |        |  |  |
| Зм.       | Кіл. | Арк.   | № | Підпис | Дат.  | Склад проекту | Стадія            | Аркцш | Аркцші |  |  |
| Розробив  |      | Придка |   |        | 09.18 |               | РП                | 1     | 1      |  |  |
| Перевірив |      |        |   |        |       |               |                   |       |        |  |  |
| ГАП       |      | Придка |   |        | 09.18 |               |                   |       |        |  |  |
|           |      |        |   |        |       |               |                   |       |        |  |  |
|           |      |        |   |        |       |               | ФО-П Придка І. А. |       |        |  |  |

## Головний архітектор проекту

І. А. Прудка

Кваліфікаційний сертифікат відповідального виконавця окремих видів робіт (послуг), пов'язаних із створенням об'єкта архітектури (розроблення містобудівної документації) Серія АА №003280

[illegible]

| Розділ проекту | Посада                      | Ініціали, прізвище | Підпис |
|----------------|-----------------------------|--------------------|--------|
| ПЗ             | Головний архітектор проекту | І. А. Прудка       |        |
| ГП             | Головний архітектор проекту | І. А. Прудка       |        |

|  |  |  |
|--|--|--|
|  |  |  |
|  |  |  |
|  |  |  |
|  |  |  |

Зам. инв. №

**Підпис і дата**

HB. №

|           |      |        |   |        |       |                                      |                   |       |        |
|-----------|------|--------|---|--------|-------|--------------------------------------|-------------------|-------|--------|
|           |      |        |   |        |       | 108/2018-ВУ                          |                   |       |        |
|           |      |        |   |        |       | Відомість про учасників проектування | Стадія            | Аркуш | Аркуші |
| Зм.       | Кіл. | Арк.   | № | Підпис | Дат.  |                                      | РП                | 1     | 1      |
| Розробив  |      | Прудка |   |        | 09.18 |                                      |                   |       |        |
| Перевірив |      |        |   |        |       |                                      |                   |       |        |
| ГАП       |      | Прудка |   |        | 09.18 |                                      |                   |       |        |
|           |      |        |   |        |       |                                      |                   |       |        |
|           |      |        |   |        |       |                                      | ФО-П Прудка І. А. |       |        |

## 1. Передмова.

Замовником плану зонування території є Широківська сільська рада Запорізького району Запорізької області.

Виконавцем плану зонування є:

Фізична особа підприємець Прудка І. А.

69039, м. Запоріжжя, пров. Вантажний, 13.

ІНН 2803210762.

Головний архітектор проекту — І. А. Прудка, кваліфікаційний сертифікат Серія АА № 003280 (розроблення містобудівної документації).

У складі авторського колективу — М. С. Прудкий.

Підставою для розробки плану зонування території села Широке є Рішення Широківської сільської ради Запорізького району Запорізької області №5 від 11 квітня 2018 року «Про розробку містобудівної документації «Генеральний план села Широке Запорізького району Запорізької області. Оновлення з розширенням меж населеного пункту та План зонування села Широке Запорізького району Запорізької області (у складі Генерального плану)», завдання на проектування генерального плану та плану зонування території села Широке Запорізького району Запорізької області.

Рішення прийняті в зонінгу населеного пункту з урахуванням чинного законодавства України у сфері містобудування та вимог державних будівельних норм, а саме:

Земельного кодексу України;

Водного кодексу України;

Закону України «Про регулювання містобудівної діяльності»

Закону України «Про основи містобудування»

Закону України «Про благоустрій населених пунктів»

ДБН Б.1.1-22:2017 «Склад та зміст плану зонування території»

Наказу «Про затвердження порядку надання містобудівних умов та обмежень забудови земельної ділянки, їх склад та зміст»

ДБН Б.2.2-12:2018 «Планування і забудова території»;

Профільних ДБН за типом об'єкту;

ДСП «Державні санітарні правила планування та забудова населених пунктів» від 19.06.96 р. № 173;

профільних СанПін за типом об'єкту.

|           |               |             |   |        |      |                      |  |  |
|-----------|---------------|-------------|---|--------|------|----------------------|--|--|
| Інв. №    | Підпис і дата | Зам. Інв. № |   |        |      |                      |  |  |
|           |               |             |   |        |      |                      |  |  |
|           |               |             |   |        |      |                      |  |  |
|           |               |             |   |        |      |                      |  |  |
|           |               |             |   |        |      | 108/2018-ПЗ          |  |  |
| Зм.       | Кіл.          | Арк.        | № | Підпис | Дат. | Пояснювальна записка |  |  |
| Розробив  |               | Прудка      |   | 09.18  |      |                      |  |  |
| Перевірив |               |             |   |        |      |                      |  |  |
| ГАП       |               | Прудка      |   | 09.18  |      |                      |  |  |
|           |               |             |   |        |      | ФО-П Прудка І. А.    |  |  |
|           |               |             |   |        |      |                      |  |  |

|     |      |       |   |        |      |
|-----|------|-------|---|--------|------|
| Зм. | Кіл. | Аркуш | № | Підпис | Дата |
|-----|------|-------|---|--------|------|

**Максимальний відсоток забудови у межах земельної ділянки** – відношення сумарної площі земельної ділянки, що може бути забудована, до всієї площі земельної ділянки.

**Максимально допустима щільність населення (для багатоквартирної житлової забудови), люд/га** – відношення кількості осіб, що можуть проживати на ділянці перспективної забудови, до площі ділянки за умови розташування на ділянці зелених насаджень, майданчиків, місць паркування автомобілів, інженерного обладнання, проходів та проїздів відповідно до державних будівельних норм.

**Мінімальна площа земельної ділянки для розміщення об'єкта** допускається не менша ніж сума площі, зайнятої існуючим чи запроєктованим об'єктом будівництва, площі необхідних озелених територій, площі для паркування автомобілів, проїздів та інших необхідних допоміжних об'єктів, призначених для обслуговування і експлуатації об'єкта згідно з зонінгом.

**Територіальна зона** – територія (у визначених межах) на схемі зонування, стосовно якої встановлені єдині зональні вимоги.

**Територіальна підзона** – частина зони, в межах якої умови та обмеження забудови земельних ділянок, відрізняються від аналогічних показників територіальної зони окремими показниками, що пов'язані з відповідними планувальними обмеженнями.

**Охоронна зона** – зона, в якій встановлюється спеціальний режим охорони об'єктів, які в ній розміщені.

**Санітарно – захисна зона** – територія навколо потенційно небезпечного підприємства, в межах якої заборонено проживання населення та ведення господарської діяльності, розміри якої встановлюються проектною документацією відповідно до державних нормативних документів.

**Червоні лінії** – визначені в містобудівній документації відносно пунктів геодезичної мережі лінії, які відмежовують елементи транспортної інфраструктури (вулиці, проїзди, площі) від елементів планувальної структури (кварталів, мікрорайонів та ін.).

- Зонінг населеного пункту створюється з метою:
- регулювання планування та забудови території з урахуванням державних, громадських та приватних інтересів;
- раціонального використання території населеного пункту;
- забезпечення умов для реалізації планів і програм сталого розвитку населених пунктів, збереження природного середовища та охорони культурної спадщини
- встановлення правових гарантій з використання і будівельної зміни нерухомості для власників і осіб, що мають намір придбати права володіння, користування і розпорядження земельними ділянками, іншими об'єктами нерухомості;

|             |               |        |     |      |       |   |        |             |       |
|-------------|---------------|--------|-----|------|-------|---|--------|-------------|-------|
|             |               |        |     |      |       |   |        |             |       |
|             |               |        |     |      |       |   |        |             |       |
|             |               |        |     |      |       |   |        |             |       |
|             |               |        |     |      |       |   |        |             |       |
| Зам. інв. № | Підпис і дата | Інв. № |     |      |       |   | 09.18  | 108/2018-ПЗ | Аркцш |
|             |               |        | Зм. | Кіл. | Аркцш | № | Підпис |             |       |

- ### 3. Принципи зонування території населеного пункту.

Зонінг розроблявся на основі генерального плану населеного пункту.

При розробленні населеного пункту схема зонування території виконувалась у межах структурно-планувальних елементів – планувальних зон та планувальних утворень (житлові, промислові, рекреаційні райони, мікрорайони, квартали тощо), обмежених магістральними вулицями або природними межами.

На схемі зонування територія населеного пункту у відповідності з функціональним призначенням поділяється на територіальні зони, для кожної з яких встановлюється містобудівний регламент.

Кодові позначення зон та підзон групуються за видами. Кодова позначка підзони включає код територіальної зони, в межах якої вона виділена, і цифровий додаток, що встановлюється в залежності від виду планувальних обмежень, які розповсюджуються на територію підзони.

Сукупність видів використання та граничних параметрів нового будівництва та реконструкції об'єктів нерухомості у складі містобудівного регламенту є єдиною для усіх об'єктів у межах відповідної зони (підзони), якщо інше не обумовлене у складі регламенту.

[illegible]



Назви і кодові позначення зон групуються за видами. Зонуванням в межах населеного пункту села Широке встановлюються такі типи територіальних зон.

### Громадські зони – Г

Г-2-1, П-Г-2-1 Зона розміщення об'єктів повсякденного обслуговування

Г-3-1 Зона шкіл та ДНЗ

### Житлові зони – Ж

Ж-1 Зона садибної забудови

Ж-1/1 Зона садибної забудови в санітарно-захисній зоні промислових підприємств I-V класу шкідливості, сільськогосподарських, комунальних, складських територій

### Ландшафтно – рекреаційна зона – Р

Р-1-1/11 Рекреаційна зона природних ландшафтів в прибережна захисній смузі

Р-3-1 Зона розміщення парків, скверів

П-Р-3-2 Зона розміщення лугопарків, гідропарків

### Зона транспортної інфраструктури – ТР

ТР-2 Зона транспортної інфраструктури

### Зона інженерної інфраструктури – ІН

ІН-1 Зона інженерної інфраструктури

ІН-2, П-ІН-2 Зона інженерної інфраструктури

### Комунально складські зони – КС

КС-3-1 Зона розміщення кладовища

КС-4-1 Зона розміщення кладовища

КС-5 Зона розміщення об'єктів 5-го класу санітарної класифікації

### Спеціальні зони – С

С-4 Зона озеленення спеціального призначення

### Зони сільськогосподарського призначення – СВ

СВ-1 Зона земель сільськогосподарського призначення

СВ-2 Зона сільськогосподарських підприємств установ та організації

СВ-1/1 Зона земель сільськогосподарського призначення в санітарно-захисній зоні промислових підприємств I-V класу шкідливості, сільськогосподарських, комунальних, складських територій

СВ-1/30 Зона земель сільськогосподарського призначення з обмеженнями на територіях всіх видів зон охорони пам'яток культурної спадщини (5 м від підстави кургану-умовно не вказано)

### Інші зони

ІК Зона земель історико – культурного призначення

ВП – водні поверхні

Зам. Інв. №

Підпис і дата

Інв. №

09.18

108/2018-ПЗ

Аркцш

Зм. Кіл. Аркцш № Підпис Дата

\* – Крім основних типів територіальних зон генеральним планом обумовлено появу зон з кодовими позначками: " П " – Проектні. Це зони, розташовані на територіях, де за генпланом на розрахунковий період визначена Проектна забудова того чи іншого призначення, зі зміною функціонального призначення існуючої забудови або без такої.

Переважні та супутні види забудови та використання земельних ділянок в межах зон з такими кодовими позначками ідентичні видам забудови та використання земельних ділянок без таких кодових позначок.

#### **5. Містобудівні регламенти як сукупність обов'язкових вимог до використання земельних ділянок та об'єктів нерухомості, що встановлюються у межах відповідних територіальних зон**

Сукупність видів використання та граничних параметрів нового будівництва та реконструкції об'єктів нерухомості у складі містобудівного регламенту є єдиною для усіх об'єктів у межах відповідної зони (підзони), якщо інше не обумовлене у складі регламенту.

Містобудівні регламенти підзон можуть відрізнятися від містобудівного регламенту територіальних зон тільки за окремими показниками дозволеного будівництва, обумовленими дією планувальних обмежень.

#### **6. Перелік дозволених видів забудови та іншого використання земельних ділянок у межах різних територіальних зон**

Для окремої земельної ділянки дозволеним є таке використання, яке відповідає містобудівному регламенту зони (підзони), на території якої ділянка знаходиться. Невідповідність наміру забудови встановленим видам дозволеного використання земельних ділянок і об'єктів, зазначеним у містобудівному регламенті, означає, що його застосування у відповідній територіальній зоні не допускається.

Суттєва зміна параметрів існуючих земельних ділянок і об'єктів нерухомості, види використання і граничні параметри яких не відповідають містобудівному регламенту, можлива лише шляхом приведення таких об'єктів у відповідність з містобудівним регламентом або шляхом зменшення їх невідповідності.

Розташування в межах земельних ділянок супутніх видів забудови – інженерно-технічних об'єктів, споруд, комунікацій, що забезпечують реалізацію дозволеного використання об'єктів нерухомості на цих ділянках, можливе за умов обов'язкового дотримання технічних умов (норм).

Зам. інв. №

Підпис і дата

Інв. №

09.18

108/2018-ПЗ

Аркцш

Зм. Кіл. Аркцш № Підпис Дата

Земельні ділянки та розташовані на них об'єкти, які існували до впровадження в дію зонінгу, граничні параметри яких не відповідають містобудівному регламенту, можуть використовуватись без визначення терміну їх приведення у відповідність з містобудівним регламентом, якщо вони

не створюють загрози для життя, здоров'я людей, для навколишнього середовища, об'єктів культурної спадщини та природно-заповідного фонду.

Зміна видів використання земельних ділянок і об'єктів нерухомості фізичними та юридичними особами здійснюється у відповідності з переліком переважних, супутніх видів забудови в межах відповідної територіальної зони за дотримання інших вимог містобудівних регламентів та в порядку, визначеному законодавством.

Види територіальних зон, перелік видів використання земельних ділянок, параметри забудови у складі містобудівних регламентів конкретизуються в залежності від містобудівних особливостей населеного пункту, місцевих умов, рішень містобудівної документації.

### Громадські зони Г

#### Г-2-1, П-Г-2-1 Зона розміщення об'єктів повсякденного обслуговування

Призначаються для розташування адміністративних будівель, магазинів, торговельних закладів, закладів обслуговування населення, установ та супутніх до них елементів транспортної інфраструктури. Зона призначена для обслуговування населення. До зони відносяться об'єкти повсякденного обслуговування.

#### Переважні види використання:

- Адміністративні будівлі (організації та установи управління, офіси, ЦНАП);
- Відділення зв'язку (пошта, телеграф, телефонні станції, об'єкти радіомовлення та телебачення);
- Банки та їх відділення (філії);
- Юридичні консультації та нотаріальні контори;
- Готелі;
- Церква;
- Установи культури та мистецтва (танцювальні зали, клубні установи, бібліотеки, музеї, виставкові зали і т. д.);
- Бульвари, парки, сквери;
- Малі архітектурні форми декоративно-технологічного призначення;
- Об'єкти побутового обслуговування населення;
- ФАП, поліклініки, амбулаторії, аптеки;
- Спортивні та фізкультурно-оздоровчі заклади;
- Автостоянки при громадських будівлях;

Зам. інв. №

Підпис і дата

Інв. №

09.18

108/2018-ПЗ

Аркцш

Зм. Кіл. Аркцш № Підпис Дата



|     |      |       |   |        |      |
|-----|------|-------|---|--------|------|
| Зм. | Кіл. | Аркуш | № | Підпис | Дата |
|-----|------|-------|---|--------|------|



- Об'єкти, що технологічно пов'язані з об'єктами переважних видів або сприяють їх безпеці, в тому числі, протипожежні, відповідно до чинної нормативно-технічної документації;

- Споруди, що призначені для охорони об'єктів переважного чи допустимого виду використання;
  - Об'єкти інженерної інфраструктури;
  - Об'єкти транспортної інфраструктури (автостоянки, велостоянки, гаражі, паркінги наземні та підземні)
  - Громадські збиральні.
- Мінімальний коефіцієнт озеленення – 75%

Мета організації зони полягає в збереженні цінних природних особливостей ландшафту, створенні умов для відпочинку населення з максимальним виявленням особливостей ландшафту і мінімальним впливом на природне середовище.

- Лугопарки, гідропарки;
- Зелені насадження загального користування;
- Ландшафти, що охороняються;
- Місця відпочинку, кемпінг;
- Об'єкти рекреаційного призначення;
- Бігові та велосипедні доріжки;
- Спортивні майданчики;
- Пункти прокату спортивного інвентарю;
- Квітники, газони;
- Скульптурні композиції, об'єкти декоративно-монументального мистецтва.

- Об'єкти, що технологічно пов'язані з об'єктами переважних видів або сприяють їх безпеці, в тому числі, протипожежні, відповідно до чинної нормативно-технічної документації;

- Споруди, що призначені для охорони об'єктів переважного чи допустимого виду використання;
- Об'єкти інженерної інфраструктури;
- Об'єкти транспортної інфраструктури (автостоянки, велостоянки, гаражі, паркінги наземні та підземні);
- Громадські вбиральні.

|             |               |        |   |        |      |  |
|-------------|---------------|--------|---|--------|------|--|
|             |               |        | <p><b>Переважні види використання:</b></p> <ul style="list-style-type: none"> <li>- Лугопарки, гідропарки;</li> <li>- Зелені насадження загального користування;</li> <li>- Ландшафти, що охороняються;</li> <li>- Місця відпочинку, кемпінг;</li> <li>- Об'єкти рекреаційного призначення;</li> <li>- Бігові та велосипедні доріжки;</li> <li>- Спортивні майданчики;</li> <li>- Пункти прокату спортивного інвентарю;</li> <li>- Квітники, газони;</li> <li>- Скульптурні композиції, об'єкти декоративно-монументального мистецтва.</li> </ul>                              |        |      |  |
|             |               |        | <p><b>Супутні види використання:</b></p> <ul style="list-style-type: none"> <li>- Об'єкти, що технологічно пов'язані з об'єктами переважних видів або сприяють їх безпеці, в тому числі, протипожежні, відповідно до чинної нормативно-технічної документації;</li> <li>- Споруди, що призначені для охорони об'єктів переважного чи допустимого виду використання;</li> <li>- Об'єкти інженерної інфраструктури;</li> <li>- Об'єкти транспортної інфраструктури (автостоянки, велостоянки, гаражі, паркінги наземні та підземні);</li> <li>- Громадські вбиральні.</li> </ul> |        |      |  |
|             |               |        |   |        |      |  |
|             |               |        |   |        |      |  |
|             |               |        |   |        |      |  |
| Зам. Інв. № | Підпис і дата | Інв. № | <p>09.18</p> <p>108/2018-ПЗ</p> <p>Аркциш</p>   |        |      |  |
| Зм.         | Кіл.          | Аркциш | №   | Підпис | Дата |  |

- Мінімальний коефіцієнт озеленення — 80%

### Зона транспортної інфраструктури ТР

#### ТР-2 Зона транспортної інфраструктури

Відносяться території вулиць, майданів (в межах червоних ліній), доріг. В залежності від ситуації, що склалася, можна виділити зону пішохідних.

#### Переважні види використання:

- Проїзні частини, пішохідні тротуари, велосипедні доріжки;
- Пішохідні переходи;
- Зупинки громадського транспорту, з кіосками продажу проїзних квитків;
- Захисні зелені насадження вздовж проїзної частини;
- Транспортні розв'язки;
- Пункти зупинки пасажирського транспорту та їх обладнання;
- Споруди лінійного та енергетичного господарства;
- Інженерні комунікації;
- Огорожа вулиць та відбійники;
- Архітектурні форми благоустрою (фонтани, клумби, декоративні насадження, майданчики відпочинку);
- Дорожня інформація (знаки та ін.).

#### Супутні види використання:

- Об'єкти, що технологічно пов'язані з об'єктами переважних видів або сприяють їх безпеці, в тому числі, протипожежні, відповідно до чинної нормативно-технічної документації;
- Споруди, що призначені для охорони об'єктів переважного чи допустимого виду використання;
- Об'єкти транспортної інфраструктури (автостоянки, велостоянки, гаражі, паркінги наземні та підземні).

### Зона інженерної інфраструктури ІН

#### ІН-1, П-ІН-1 Зона інженерної інфраструктури

Призначена для розміщення головних об'єктів електромережі.

#### Переважні види використання:

- Електричні підстанції;
- Сонячні панелі;
- Технологічні проїзди та проходи;
- Огорожі;
- Адміністративні будівлі та споруди, що пов'язані з функціонуванням об'єктів зони;

Зам. Інв. №

Підпис і дата

Інв. №

09.18

108/2018-ПЗ

Аркцш

Зм. Кіл. Аркцш № Підпис Дата

- Зелені насадження спеціального призначення;
- Споруди інженерної інфраструктури.

#### **Супутні види використання:**

- Об'єкти, що технологічно пов'язані з об'єктами переважних видів або сприяють їх безпеці, в тому числі, протипожежні, відповідно до чинної нормативно-технічної документації;
- Споруди, що призначені для охорони об'єктів переважного чи допустимого виду використання;
- Об'єкти транспортної інфраструктури (автостоянки, велостоянки, гаражі, паркінги наземні та підземні).

### **ІН-2 Зона інженерної інфраструктури**

Призначена для розміщення головних об'єктів тепломереж, водопостачання, каналізації, газопостачання, зливової каналізації.

#### **Переважні види використання:**

- ГРС, ГРП;
- Котельні;
- Споруди інженерної інфраструктури тепло- та газопостачання, водопостачання, каналізації;
- Технологічні проїзди та проходи;
- Огорожі;
- Адміністративні будівлі та споруди, що пов'язані з функціонуванням об'єктів зони;
- Зелені насадження спеціального призначення.

#### **Супутні види використання:**

- Об'єкти, що технологічно пов'язані з об'єктами переважних видів або сприяють їх безпеці, в тому числі, протипожежні, відповідно до чинної нормативно-технічної документації;
- Споруди, що призначені для охорони об'єктів переважного чи допустимого виду використання;
- Об'єкти транспортної інфраструктури (автостоянки, велостоянки, гаражі, паркінги наземні та підземні).

### **Комунально складські зони КС**

#### **КС-3-1 Зона розміщення кладовища**

Призначається для розміщення об'єктів, що потребують встановлення СЗЗ 300 м.

#### **Переважні види використання:**

- Кладовища;
- Технологічні проїзди та проходи;
- Огорожі;

Зам. Інв. №

Підпис і дата

Інв. №

09.18

108/2018-ПЗ

Аркцш

Зм.

Кіл.

Аркцш

№

Підпис

Дата

- Адміністративні будівлі та споруди, що пов'язані з функціонуванням зони;
- Зелені насадження.

#### **Супутні види використання:**

- Об'єкти, що технологічно пов'язані з об'єктами переважних видів або сприяють їх безпеці, в тому числі, протипожежні, відповідно до чинної нормативно-технічної документації;
- Споруди, що призначені для охорони об'єктів переважного чи допустимого виду використання;
- Об'єкти інженерної інфраструктури;
- Об'єкти транспортної інфраструктури (автостоянки, велостоянки, гаражі).

### **КС-4-1 Зона розміщення кладовища**

Призначається для розміщення об'єктів, що потребують встановлення СЗЗ 100 м.

#### **Переважні види використання:**

- Кладовища;
- Технологічні проїзди та проходи;
- Огорожі;
- Адміністративні будівлі та споруди, що пов'язані з функціонуванням зони;
- Зелені насадження.

#### **Супутні види використання:**

- Об'єкти, що технологічно пов'язані з об'єктами переважних видів або сприяють їх безпеці, в тому числі, протипожежні, відповідно до чинної нормативно-технічної документації;
- Споруди, що призначені для охорони об'єктів переважного чи допустимого виду використання;
- Об'єкти інженерної інфраструктури;
- Об'єкти транспортної інфраструктури (автостоянки, велостоянки, гаражі).

### **КС-5 Зона розміщення об'єктів 5-го класу санітарної класифікації**

Призначається для розміщення об'єктів, що потребують встановлення СЗЗ 50 м.

#### **Переважні види використання:**

- Склади, бази 5-го класу шкідливості;
- Оптові ринки;
- Підприємства по обслуговуванню автомобілів;
- Пожежні депо;
- Підприємства комунального господарства;

Зам. інв. №

Підпис і дата

Інв. №

09.18

108/2018-ПЗ

Аркцш

Зм. Кіл. Аркцш № Підпис Дата

- ### Супутні види використання:

- ## Спеціальні зони

Призначені для розташування спецтериторій, пенітенціарних установ тощо. У спеціальних зонах передбачається розміщення об'єктів, які за своєю функцією несумісні з іншими об'єктами в інших територіальних зонах, а створення і використання цих зон неможливе без встановлення спеціальних вимог.

**С-4, П-С-4 Зона озеленення спеціального призначення**

Зона формується в межах територій, на яких за містобудівною документацією передбачається організація санітарно-захисних зон.

### Переважні види використання:

- Пішохідні доріжки, проїзди, проходи, дороги;
- Багаторічні зелені насадження.
- Об'єкти комунального господарства зі спеціальними інженерними спорудами;
- Підприємства які не викидають в атмосферу шкідливих речовин;
- Адміністративні об'єкти, що пов'язані з функціонуванням спеціальних об'єктів;
- Об'єкти інженерної інфраструктури.
- Зелені насадження спеціального призначення.

### Супутні види використання:

- Об'єкти, що технологічно пов'язані з об'єктами переважних видів або сприяють їх безпеці, в тому числі, протипожежні, відповідно до чинної нормативно-технічної документації;
- Споруди, що призначені для охорони об'єктів переважного чи допустимого виду використання;



## СВ-2 Зона сільськогосподарських підприємств установ та організації.

### Переважні види використання:

- Сільськогосподарські підприємства, господарства із санітарно-захисною зоною 50-200 м;
- Науково-дослідні сільськогосподарські установи;
- Підприємства по складуванню та переробці сільськогосподарської продукції; склади зберігання сільськогосподарської продукції, продовольчі та торгово – розподільчі склади;
- Холодильники, овочесховища;
- Підприємства по обслуговуванню транспортних засобів;
- Адміністративні об'єкти, що пов'язані з функціонуванням об'єктів;
- Споруди інженерної інфраструктури;
- Зелені насадження спеціального призначення.

### Супутні види використання:

- Об'єкти, що технологічно пов'язані з об'єктами переважних видів або сприяють їх безпеці, в тому числі, протипожежні, відповідно до чинної нормативно-технічної документації;
- Споруди, що призначені для охорони об'єктів переважного чи допустимого виду використання;
- Об'єкти інженерної інфраструктури;
- Об'єкти транспортної інфраструктури (автостоянки, велостоянки, гаражі, паркінги наземні та підземні).

Мінімальна щільність забудови сільськогосподарських підприємств згідно додатку Г.2 ДБН Б.2.2-12:2018 «Планування і забудова територій»

## Інші зони

### ІК Зона земель історико – культурного призначення

Землі історико-культурного фонду – це земельні ділянки на території яких присутні об'єкти культурної спадщини. До таких об'єктів відносяться пам'ятки історії, пам'ятки археології місцевого, регіонального чи державного значення. Наявність досліджених об'єктів археології скіфського часу та епохи бронзи в окрузі обумовлюють вірогідність виявлення нових об'єктів археології.

На цих землях необхідним є врахування та дотримання вимог Законів України «Про охорону культурної спадщини» та «Про охорону археологічної спадщини».

### Переважні види використання:

- Збереження пам'яток історії, археології, культури, архітектури, монументального мистецтва, їх музеєфікація;
- Розміщення допоміжних будинків та споруд для обслуговування існуючих пам'яток, туристичних груп
- Влаштування виставкової, концертної та іншої супутньої діяльності.

Зам. Інв. №

Підпис і дата

Інв. №

09.18

108/2018-ПЗ

Аркцш

Зм. Кіл. Аркцш № Підпис Дата



**Планувальні обмеження  
які діють на території населеного пункту**

| <b>Обмеження, пов'язані з дотриманням санітарно – гігієнічних та природоохоронних норм:</b> |   |
|---------------------------------------------------------------------------------------------|---|
| <b>Планувальні обмеження</b>                                                                | <b>Режим використання і забудови території, на яких діють планувальні обмеження</b>   |
| Санітарна – захисна зона сільськогосподарських підприємств та комунальних територій         | У санітарно-захисних зонах не можна допускати розміщення:<br>- житлових будинків з прибудинковими територіями, гуртожитків, готелів; дитячих дошкільних закладів, загальноосвітніх шкіл, лікувально-профілактичних та оздоровчих установ; спортивних споруд, зелених насаджень загального користування;<br>-заборона розглядати зону як резервну територію для розширення підприємств, розвитку сільськогосподарських територій.   |
| Прибережна захисна смуга                                                                    | Рекомендовано розчищення русла річки.<br>На території водоохоронних зон забороняється:<br>-використання стійких та сильнодіючих пестицидів;<br>-влаштування кладовищ, скотомогильників, звалищ, полів фільтрації;<br>-скидання неочищених стічних вод, використовуючи рельєф місцевості (балки, пониззя, кар'єри тощо), а також потічки розорювання земель (крім підготовки ґрунту для залуження і залісення), а також садівництво та городництво;<br>-зберігання та застосування пестицидів і добрив; влаштування літніх таборів для худоби;<br>-будівництво будь-яких споруд (крім гідротехнічних,<br>-гідрометричних та лінійних), у тому числі баз відпочинку, дач, гаражів та стоянок автомобілів; миття та обслуговування транспортних засобів і техніки;<br>-влаштування звалищ сміття, зноєсховищ, накопичувачів рідких і твердих відходів виробництва, кладовищ, скотомогильників, полів фільтрації тощо. |
| Санітарно – захисна зона кладовища                                                          | заборона на розміщення:<br>- житлових будинків з прибудинковими територіями, гуртожитків, готелів, будинків для пріїжджих;<br>- дитячих дошкільних закладів, загальноосвітніх шкіл, лікувально-профілактичних та оздоровчих   |

Зам. Інв. №

Підпис і дата

Інв. №

09.18

108/2018-ПЗ

Аркцш

Зм. Кіл. Аркцш № Підпис Дата

|  |   |
|--|---|
|  | <p>установ загального та спеціального призначення зі стаціонарами, наркологічних диспансерів;</p> <p>- спортивних споруд, садів, садівницьких товариств;</p> <p>- джерел централізованого водопостачання, водозабірних споруд, споруд водопровідної розподільної мережі.</p> <p>- заборона розглядати зону як резервну територію для розвитку сільбищних територій, якщо містобудівною документацією не передбачається закриття об'єктів та, відповідно скорочення СЗЗ.</p> <p>Вимоги до водозабезпечення будівель - обов'язкове підключення до мережі централізованого водопроводу</p> |
|--|---|

**Обмеження, що пов'язані з охоронною магістральних мереж інженерної інфраструктури та об'єктів на них**

|                                                                     |   |
|---------------------------------------------------------------------|---|
| Магістральні електромережі та об'єкти на них                        | <p>В межах санітарно-захисних зон забороняється:</p> <p>розміщувати житлові і громадські будівлі, дачні ділянки та інші місця перебування людей, майданчики для стоянки та зупинки всіх видів транспорту, підприємства по обслуговуванню автомобілів, а також сховища нафти і нафтопродуктів.</p> <p>Сільськогосподарські угіддя, що знаходяться на території санітарно-захисних зон ПЛЕ, можуть бути використані для вирощування сільськогосподарських культур, що не потребують ручної обробки, тобто повинні бути виключені умови для тривалого перебування людини в зоні дії електричного поля.</p> <p>Охоронні зони:</p> <ul style="list-style-type: none"> <li>- кабелі силові всіх напруг та кабелі зв'язку - 0,6 м;</li> <li>- ПЛ до 20 кВ охоронна зона - 10 м;</li> <li>- ПЛ 35 кВ охоронна зона - 15 м;</li> <li>- Трансформаторна підстанція - 3 м від огорожі</li> </ul> |
| Водоводи, водовідведення, колектори каналізації, колектори зливової | <p>В зонах санітарної охорони свердловин 15 м забороняється:</p> <ul style="list-style-type: none"> <li>- здійснення діяльності щодо утримання та експлуатації інженерних мереж;</li> <li>- будівництво будівель та споруд в охоронній зоні трубопроводів;</li> <li>- будівництво, ліквідацію будівель та споруд, вирубаня дерев, встановлення загородження, проведення земляних робіт на глибині понад 0,3 м,</li> </ul>   |

Зам. Інв. №

Підпис і дата

Інв. №

09.18

108/2018-ПЗ

Аркцш

Зм. Кіл. Аркцш № Підпис Дата



тралення жорсткими і напівжорсткими тралами при перетинанні газопроводами водних перешкод (в охоронних зонах підвідних газопроводів);

8) розпалювати вогнище і розміщувати дудь-які відкриті або закриті джерела вогню;

9) проводити дудь-які заходи, пов'язані з великим скупченням людей, не зайнятих виконанням дозволених в установленому порядку робіт.

Охоронні зони та відстань від фундаментів будівель та споруд до:

Газопроводу горючих газів:

- низького тиску до 0.05 кгс/кв.см<sup>2</sup> - 2 м;
- газопроводи горючих газів середнього тиску від 0.05 до 3 кгс/кв.см<sup>2</sup> - 4 м;
- газопроводи горючих газів високого тиску від 3 до 6 кгс/кв.см<sup>2</sup> - 7 м;
- газопроводи горючих газів високого тиску до понад 6 до 12 кгс/кв.см<sup>2</sup> - 10 м;
- навколо будівель ГРП, ШРП, ВОГ - у вигляді ділянки землі, обмеженої умовною лінією, віддаленої від зовнішніх стін будинку (шаф) ГРП, ВОГ, ШРП при тиску газу на вводі в ГРП, ШРП, ВОГ до 0,6 МПа на 10 метрів у всі сторони, а при тиску газу на вводі в ГРП, ШРП, ВОГ понад 0,6 до 1,2 МПа - на 15 м у всі сторони.

#### Вимоги до ділянок, що знаходяться в охоронних зонах пам'яток культурної спадщини

Зона охорони археологічного культурного шару

Заборона

- на містобудівні, архітектурні чи ландшафтні перетворення, будівельні, меліоративні, шляхові роботи без дозволу відповідного органу охорони культурної спадщини;
- здійснення обстеження та археологічного нагляду за проведенням робіт під час проведення земляних робіт чи нового будівництва на вже забудованих ділянках міста;

обов'язкове попереднє археологічне обстеження у випадку проведенням будівельних робіт на нових територіях

Зам. Інв. №

Підпис і дата

Інв. №

09.18

108/2018-ПЗ

Аркцш

Зм. Кіл. Аркцш № Підпис Дата


## 8. Додатки

1. Зменшена копія плану зонування території
2. Рішення Широківської сільської ради Запорізького району Запорізької області №5 від 11 квітня 2018 року «Про розробку містобудівної документації «Генеральний план села Широке Запорізького району Запорізької області. Оновлення з розширенням меж населеного пункту та План зонування села Широке Запорізького району Запорізької області (у складі Генерального плану)»Завдання на проектування генерального плану з планом зонування території села Широке Запорізького району Запорізької області.
3. Завдання на проектування генерального плану з планом зонування території села Широке Запорізького району Запорізької області.
4. Лист Запорізької обласної державної адміністрації №03805/08-27 від 15.05.2018 «Про визначення та врахування державних та регіональних інтересів під час розроблення генерального плану села Широке».
5. Копія кваліфікаційного сертифіката серія АА № 003280 зареєстрованого 14 липня 2016 року. Розроблення містобудівної документації.

[illegible]

село Широке  
Запорізького району, Запорізької області

План зонування території  
1:5000

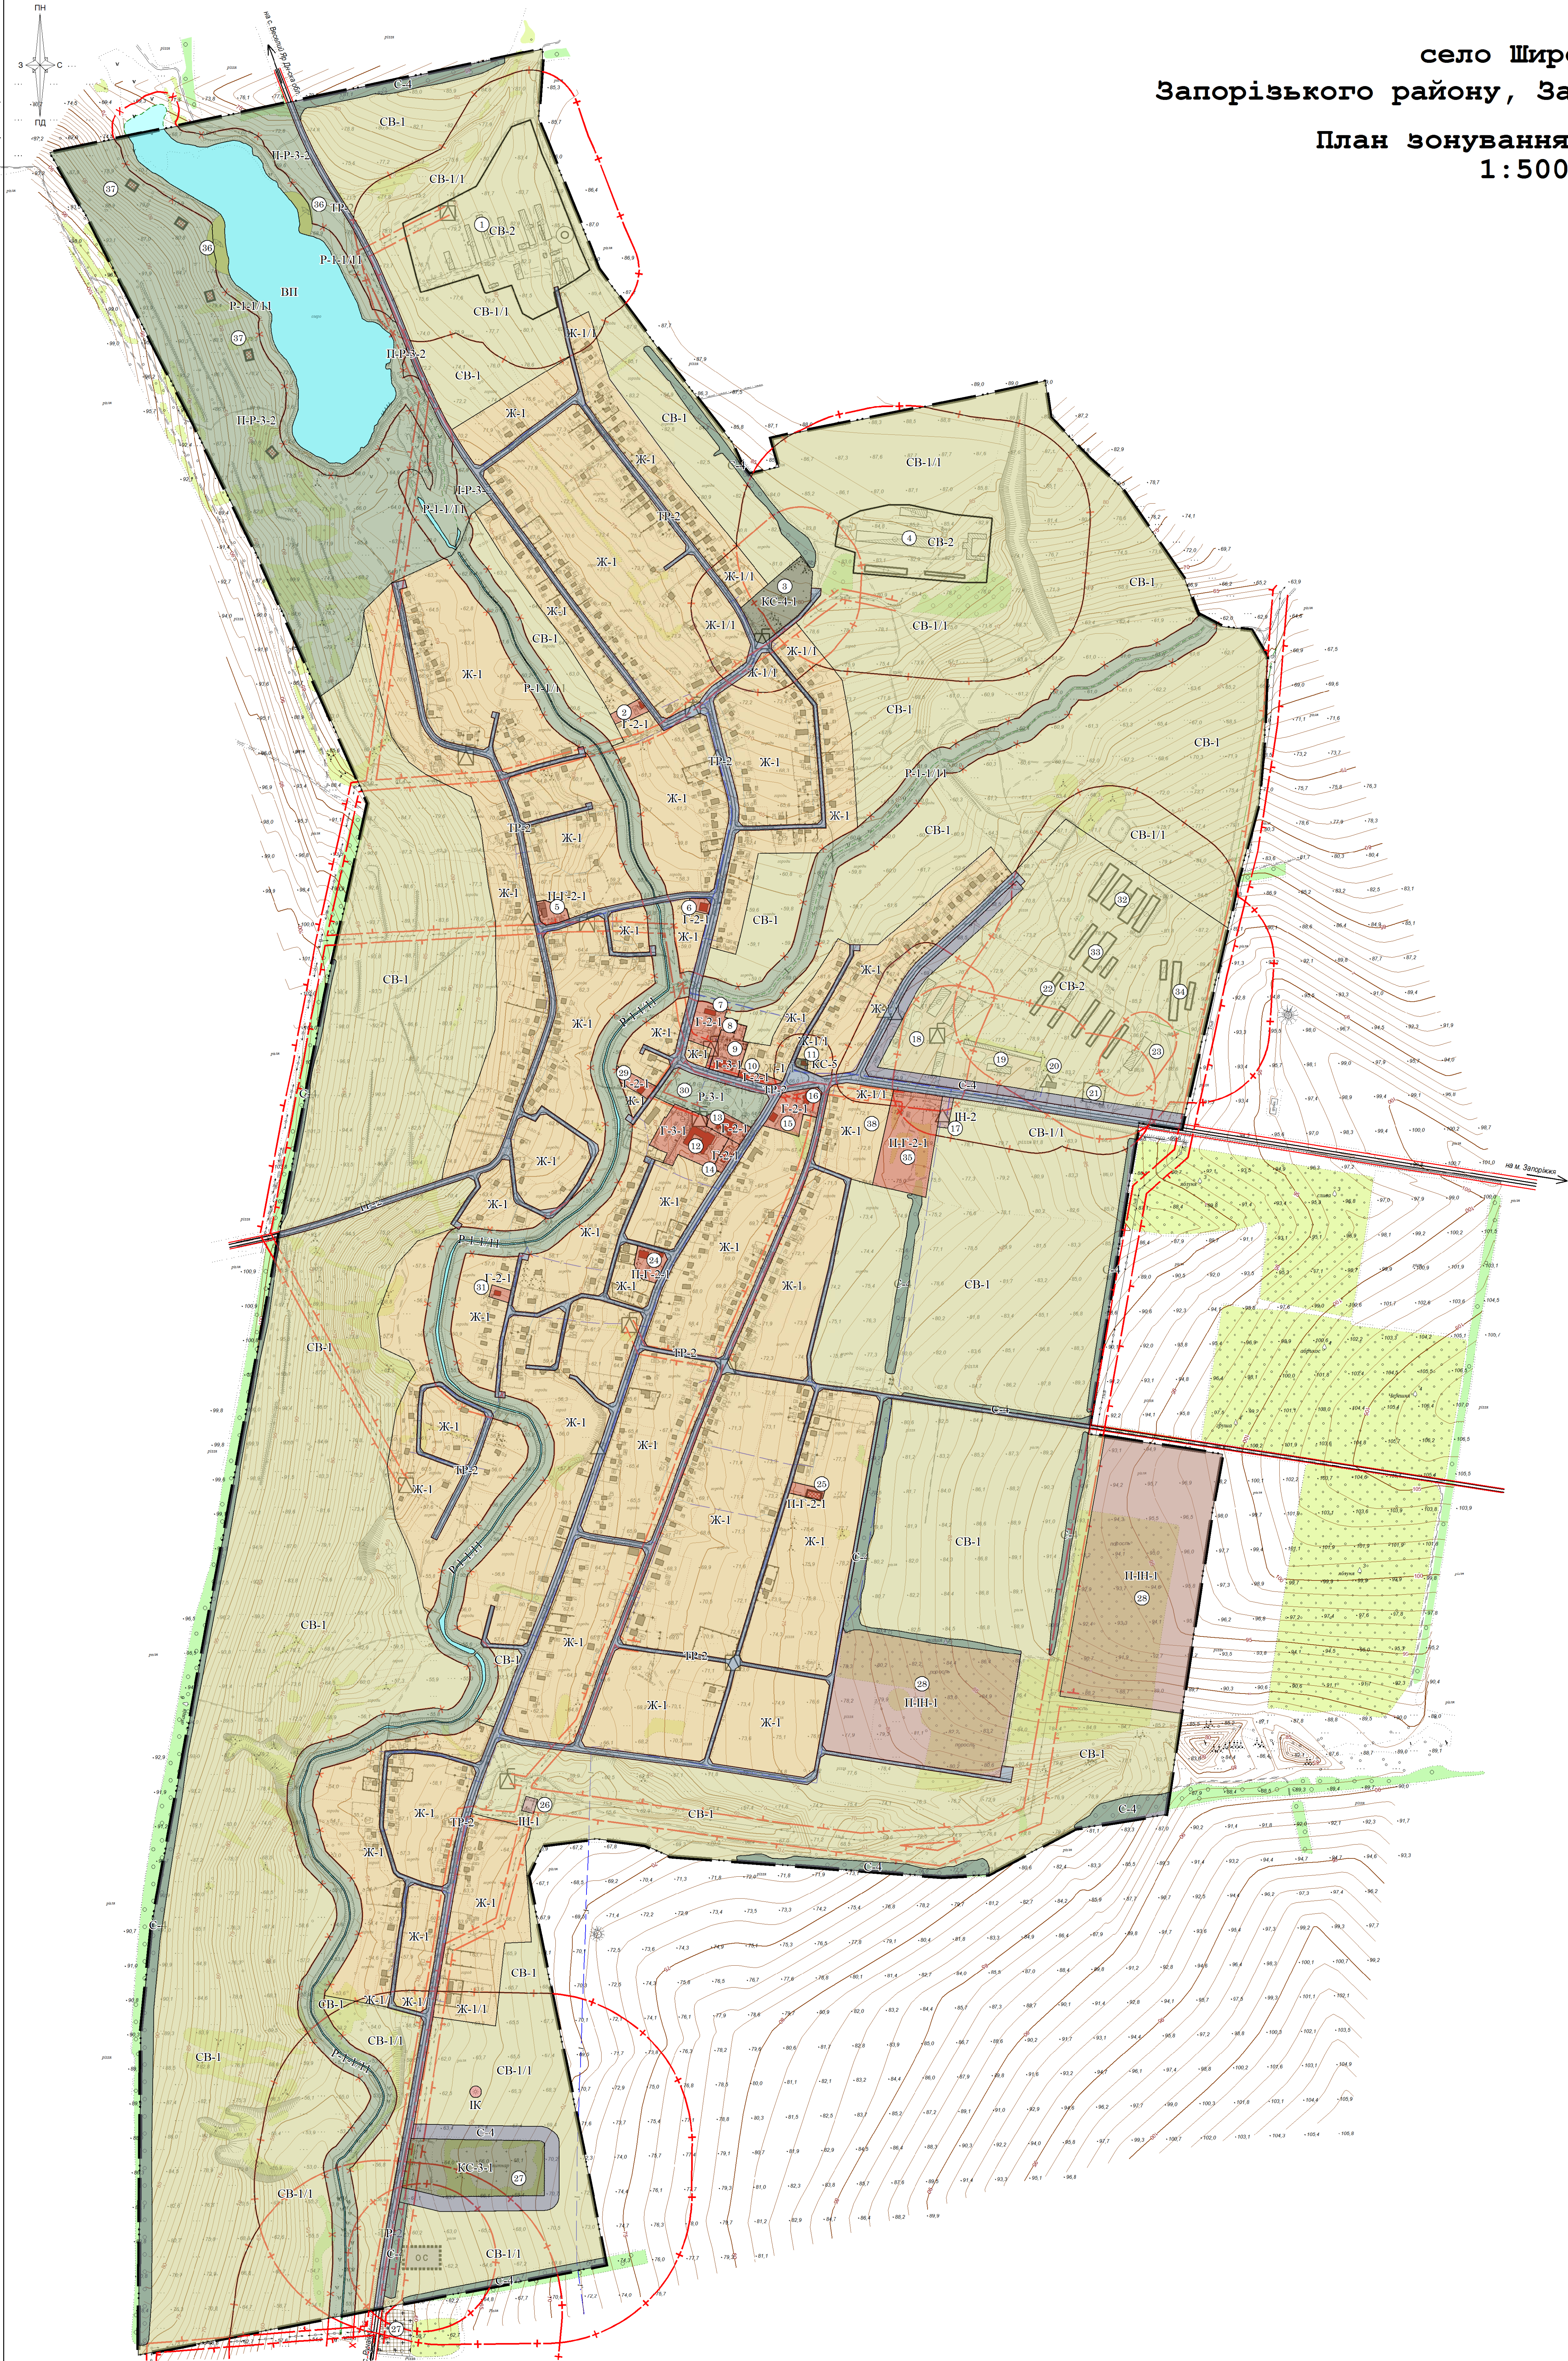

Умовні позначення

— Межа населеного пункту проєктна

- Громадські зони - Г

- Г-2-1 Зона розміщення об'єктів повсякденного обслуговування
- Г-1-2-1 Зона розміщення об'єктів повсякденного обслуговування проєктна
- Г-3-1 Зона шкіл та ДНЗ

- Житлові зони - Ж

- Ж-1 Зона садибної забудови
- Ж-1/1 Зона садибної забудови в санітарно-захисній зоні промислових підприємств І-V класу шкідливості, сільськогосподарських, комунальних, складських територій

- Ландшафтно-рекреаційні зони - Р

- Р-1-1/1 Рекреаційна зона природних ландшафтів в прибережній захисній смузі
- Р-3-1 Зона розміщення парків, скверів
- Р-1-3-2 Зона розміщення парковок, гідропарків проєктна

- Зони транспортної інфраструктури - ТР

- ТР-2 Зона транспортної інфраструктури території вулиць

- Зони інженерної інфраструктури - ІН

- ІН-1 Зона інженерної інфраструктури
- ІН-Н-1 Зона інженерної інфраструктури проєктна
- ІН-2 Зона інженерної інфраструктури

- Комунально-складські зони - КС

- КС-3-1 Зона розміщення об'єктів 3-го класу санітарної класифікації
- КС-4-1 Зона розміщення об'єктів 4-го класу санітарної класифікації
- КС-5 Зона розміщення об'єктів 5-го класу санітарної класифікації

- Спеціальні зони - С

- С-4 Зона озеленення спецпризначення
- ІН-С-4 Зона озеленення спецпризначення проєктна

- Зони сільськогосподарського призначення - СВ

- СВ-1 Зона земель сільськогосподарського призначення
- СВ-1/1 Зона земель сільськогосподарського призначення в санітарно-захисній зоні промислових підприємств І-V класу шкідливості, сільськогосподарських, комунальних, складських територій
- СВ-2 Зона земель сільськогосподарських підприємств, установ та організацій
- СВ-1/30 Зона земель сільськогосподарського призначення з обмеженнями на територіях всіх видів зон охорони пам'яток культурної спадщини (5 м від підшови кураву-умовно не показано)

- Інші зони

- ІК Зона земель історико-культурного призначення
- ВП Водна поверхня

Експлікація будівель та споруд

| № п/п | Найменування   | Примітка  |
|-------|---|-----------|
| 1.    | Сільськогосподарське підприємство: зернохвище, сенокосище, телятник на 100 гол., свинарник на 75 гол., будівлі технічного обслуговування та зберігання сільськогосподарських машин СЗЗ 100 м |           |
| 2.    | Коск з літнім майданчиком. Магазин   |           |
| 3.    | Кладовище СЗЗ 100 м   |           |
| 4.    | Сільськогосподарське підприємство: зернохвище, телятник до 400 гол. СЗЗ 200 м   |           |
| 5.    | Адміністративно - торговельний комплекс по реалізації сільськогосподарської продукції   | Реконстр. |
| 6.    | Крамниця продовольчих товарів   |           |
| 7.    | Церква   |           |
| 8.    | Котельня   |           |
| 9.    | Дитячий садок   |           |
| 10.   | Крамниця змішаної торгівлі   |           |
| 11.   | Пожежна частина СЗЗ 50 м   |           |
| 12.   | Широківська загальноосвітня школа І-ІІІ ступенів   |           |
| 13.   | Широківський будинок культури. ЦНАП   |           |
| 14.   | Крамниця змішаної торгівлі   |           |
| 15.   | Адміністративна будівля. ФАП   |           |
| 16.   | Церква   |           |
| 17.   | ГРС   |           |
| 18.   | Зернохвище СЗЗ 50 м   |           |
| 19.   | Підприємство технічного обслуговування та зберігання сільськогосподарських машин СЗЗ 100 м                                                                                                   |           |
| 20.   | Адміністративна будівля сільськогосподарського підприємства   |           |
| 21.   | Склад ГСМ СЗЗ 100 м   |           |
| 22.   | Телятник на 150 гол. СЗЗ 150 м   |           |
| 23.   | Зернохвище СЗЗ 50 м   |           |
| 24.   | Будівля побутового обслуговування   | Реконстр. |
| 25.   | Крамниця сільськогосподарської продукції   | Реконстр. |
| 26.   | Електрична підстанція ОЗ 3 м   |           |
| 27.   | Кладовище СЗЗ 300 м   |           |
| 28.   | Сонячні панелі   | Проектн.  |
| 29.   | Спортивний клуб   |           |
| 30.   | Парк   |           |
| 31.   | Будівля дільничної ветеринарної медицини   |           |
| 32.   | Телятник на 150 гол. СЗЗ 150 м   |           |
| 33.   | Свинарник на 100 гол. СЗЗ 150 м   |           |
| 34.   | Віцеферма на 200 гол. СЗЗ 150 м   |           |
| 35.   | Ринок. Кафе. Крамниця   | Проектн.  |
| 36.   | Територія пляжу   | Проектн.  |
| 37.   | Будинки відпочинку   | Проектн.  |
| 38.   | Малий груповий будинок та дитячий будинок сімейного типу   | Проектн.  |

|           |        |      |        |       |      |                                                                                                 |  |                |            |            |  |
|-----------|--------|------|--------|-------|------|-------------------------------------------------------------------------------------------------|--|----------------|------------|------------|--|
|           |        |      |        |       |      | 108/2018                                                                                        |  |                |            |            |  |
|           |        |      |        |       |      | Генеральний план, План зонування території села Широке Запорізького району Запорізької області. |  |                |            |            |  |
| Зміст     | Кільк. | Арх. | № док. | Підп. | Дата | Засновник:<br>Широківська сільська рада                                                         |  | Стала<br>ГП    | Архив<br>7 | Архив<br>7 |  |
| Г.АП      | Пруда  |      |        |       |      | План зонування території<br>1:5000                                                              |  | ФОРМ Пруда ІА. |            |            |  |
| Перевірив | Пруда  |      |        |       |      |                                                                                                 |  |                |            |            |  |



УКРАЇНА  
ШИРОКІВСЬКА СІЛЬСЬКА РАДА  
ЗАПОРІЗЬКОГО РАЙОНУ ЗАПОРІЗЬКОЇ ОБЛАСТІ  
П'ЯТНАДЦЯТА ПОЗАЧЕРГОВА СЕСІЯ СЬОМОГО СКЛИКАННЯ

РІШЕННЯ

11 квітня 2018 року

№ 5

с. Широке

Про розроблення містобудівної документації «Генеральний план села Широке Запорізького району Запорізької області. Оновлення з розширенням меж населеного пункту та План зонування села Широке Запорізького району Запорізької області (у складі Генерального плану)»

Враховуючи необхідність раціонального використання земель, створення належних умов для життєзабезпечення села Широке та керуючись п. 42 частини 1, ст.26 Закону України “Про місцеве самоврядування в Україні”, ст.17 Закону України “Про регулювання містобудівної діяльності”, Широківська сільська рада Запорізького району Запорізької області

ВИРІШИЛА:

1. Розробити містобудівну документацію «Генеральний план села Широке Запорізького району Запорізької області. Оновлення з розширенням меж населеного пункту та План зонування села Широке Запорізького району Запорізької області (у складі Генерального плану)» (далі - містобудівна документація).

2. Визначити замовником містобудівної документації Виконавчий комітет Широківської сільської ради Запорізького району Запорізької області.

3. Виконавчому комітету Широківської сільської ради Запорізького району Запорізької області:

3.1. Визначити організацію-розробника містобудівної документації, яка має право на виконання даного виду робіт, строки розроблення та джерела його фінансування.

3.2. Повідомити через місцеві засоби масової інформації про початок розроблення містобудівної документації.

3.3. Укласти договір з організацією-розробником містобудівної документації.

Планувальними рішеннями Схеми планування території Запорізької області на території села Широке є передбачено:

зона впливу автомобільного транспортного коридору Європа-Азія;  
розчистка р. Томаківка;  
відвід поверхневих вод з території села.

Необхідно виконати роботи з розробки розділу «Інженерно-технічні заходи цивільного захисту» (далі – ІТЗ ЦЗ), який є складовою частиною містобудівної документації (схеми планування території або генерального плану). Головним завданням розділу ІТЗ ЦЗ при плануванні території є створення містобудівних умов, забезпечення захисту населення і територій від надзвичайних ситуацій техногенного та природного характеру, їх наслідків з урахуванням особливостей соціально-економічного розвитку та природно-кліматичних умов. Розділ розробити згідно ДБН Б.1.1-5:2007 Склад, зміст, порядок розроблення, погодження та затвердження розділу інженерно-технічних заходів цивільного захисту (цивільної оборони) у містобудівній документації (перша та друга частини), де визначити конкретні рішення щодо забезпечення захисту населення і територій від надзвичайних ситуацій техногенного і природного характеру та їх наслідків.

При розробленні містобудівної документації необхідно врахувати обмеження господарської діяльності в межах берегової захисної смуги та водоохоронної зони затоки р. Томаківка.

На території та за сучасними межами с. Широке Запорізького району розташовані пам'ятки культурної спадщини місцевого значення, взяті на облік відповідно до Закону УРСР «Про охорону та використання пам'яток історії та культури».

Пам'ятки археології місцевого значення:

курган, охоронний № 4109, розташований за 0,3 км на схід від південно-східної околиці с. Широке, взятий на облік розпорядженням голови Запорізької облдержадміністрації від 11.03.1996 № 161;

курганний могильник з 18 курганів, охоронний № 1926, розташований за 0,5 км на захід від західної околиці с. Широке, взятий на облік рішенням виконкому Запорізької обласної ради народних депутатів від 23.10.1984 № 354;

курганний могильник з 4 курганів, охоронний № 1929, розташований за 0,5 км на схід від східної околиці с. Широке, взятий на облік рішенням виконкому Запорізької обласної ради народних депутатів від 23.10.1984 № 354;

курган, охоронний № 4111, розташований за 0,6 км на північний схід від північної околиці с. Широке, Взятий на облік розпорядженням голови Запорізької облдержадміністрації від 11.03.1996 № 161;

курганний могильник «Могила Гологанка» з 20 курганів, розташований за 1,0 км на захід від північно-західної околиці с. Широке, взятий на облік рішенням виконкому Запорізької обласної ради народних депутатів від 23.10.1984 № 354;

курганний могильник з 4 курганів, охоронний № 1928, розташований за 1,6 км на південний захід від південної околиці с. Широке, взятий на облік

Додаток № 1 до договору № 108/1018 від 18.06.2018р.  
(згідно ДБН Б. 1.1-15:2012 "Склад та зміст Генерального плану населеного пункту")

Затверджено:

Голова Широківської сільської ради

\_\_\_\_\_ Коротенко Д.О.

« \_\_\_\_\_ » \_\_\_\_\_ 2018р.  
М.П.

Погоджено:

Начальник відділу містобудування,  
архітектури та житлово-  
комунального господарства  
Запорізької РДА

\_\_\_\_\_ Неумивака А.О.

« \_\_\_\_\_ » \_\_\_\_\_ 2018р.  
М.П.

Погоджено:

ФО-П Прудка І. А.

\_\_\_\_\_ Прудка І.

« \_\_\_\_\_ » \_\_\_\_\_ 2018р.  
М.П.

## ЗАВДАННЯ

на розроблення містобудівної документації «Генеральний план села Широке Запорізького району Запорізької області. Оновлення з розширенням меж населеного пункту та план зонування села Широке Запорізького району Запорізької області ( у складі генерального плану)».

Згідно з ДБН Б.1.1-15:2012 «Склад та зміст генерального плану населеного пункту» та ДСТУ-Н Б Б.1.1-12:2011 «Настанова про склад та зміст плану зонування території (зонінг)».

|                                            |   |
|--------------------------------------------|---|
| 1. Підстави для проектування               | Рішення Широківської сільської ради Запорізького району Запорізької області: «Про Розроблення генерального плану села Широке Запорізького району Запорізької області. Оновлення з розширенням меж населеного пункту та план зонування села Широке Запорізького району Запорізької області (у складі генерального плану)» від 11.04.2018 №5 |
| 2. Замовник розроблення генерального плану | Широківська сільська рада Запорізького району Запорізької області.   |
| 3. Розробник генерального плану            | ФО-П Прудка І. А.<br>Головний архітектор проекту Прудка І.А.   |

|                                                                            |   |
|----------------------------------------------------------------------------|---|
|                                                                            | Кваліфікаційний сертифікат Серія АА № 003280 (розроблення містобудівної документації).   |
| 4. Строк розроблення генерального плану                                    | Визначається договором на виконання робіт   |
| 5. Мета розроблення генерального плану                                     | Генеральний план необхідно розробити з врахуванням:<br>1. Розширенням меж населеного пункту та його прилеглої зони, уточнення параметрів забудови;<br>2. Зміни показників розрахункової чисельності населення та нормативну забезпеченість села об'єктами обслуговування;<br>3. Необхідністю розроблення нових розділів генплану відповідно до діючого законодавства.<br>4. З метою визначення умов та обмежень використання території для містобудівних потреб.   |
| 6.Строк розрахункового етапу генерального плану та першої черги реалізації | Розрахунковий етап - 2038р.(20років),<br>Перша черга реалізації – 2023р. (5років).   |
| 7. Основні показники населеного пункту.                                    | Розробити генерального плану для розміщення населення<br>- проектна площа 631 га,<br>- на розрахунковий період – 2,250 тис. осіб,<br>Показник уточняється при розробці генерального плану   |
| 8. Вихідні дані для розроблення генерального плану (надаються Замовником)  | 1. Тахеометрична зйомка виконана у державній геодезичній системі координат УСК-2000.<br>2. Матеріали інженерних, інженерно-геологічних та геодезичних вишукувань.<br>3. Матеріали санітарно-гігієнічного стану території села, обмеження щодо використання різних територій, інших природно-географічних та геологічних факторів.<br>4. Місцеві програми соціально-економічного розвитку, демографічні дані за останні 10 років, наявність об'єктів соціального, побутового та комунального обслуговування.<br>5. Дані щодо існуючого використання території (на основі державного земельного кадастру).<br>6. Історико-культурні об'єкти, охоронні зони та інші умови відносно збереження історико-культурної спадщини.<br>7. Перелік раніше розробленої містобудівної, землевпорядної документації, проектно-дослідницьких та вишукувальних робіт, які необхідно врахувати при проектуванні. |
| 9. Графічні матеріали з зазначенням масштабу                               | 1. Схема розташування територій, щодо яких вносяться зміни, у функціонально-планувальній   |

|   |   |
|---|---|
|   | <p>структурі населеного пункту - б/м.</p> <p>2. План існуючого використання території. Схема існуючих планувальних обмежень М 1:5000</p> <p>3. Генеральний план (основне креслення). Схема проектних планувальних обмежень М 1:5000</p> <p>4. Схема вулично – дорожньої мережі, міського (сільського) та зовнішнього транспорту М 1:5000</p> <p>5. Схема інженерного обладнання території М 1:5000</p> <p>6. Схема інженерної підготовки та захисту території М 1:5000</p> <p>7. План зонування території М1:5000</p>   |
| 10. Перелік додаткових розділів та графічних матеріалів, або додаткові вимоги до змісту окремих розділів чи графічних матеріалів. | <p>1. Виготовити план зонування території у складі генерального плану населеного пункту</p> <p>2. Окремим томом виконати розділ «Інженерно-технічних заходів цивільного захисту (цивільної оборони)» на особливий період виконати, згідно окремого завдання на проектування, з врахуванням рішень затверджених відповідних розділів проектів (схем) районного планування.</p>   |
| 11. Особливі вимоги до забудови, інженерного обладнання, організації транспорту, пішоходів                                        | <p>1. Висотність забудови не повинна перевищувати 1 - 4 поверхи.</p> <p>2. Переважним видом забудови прийняти садибну, з ділянками 0,25 га, в тому числі.</p> <p>3. Надати пропозиції щодо розвитку внутрішньої мережі вулиць.</p> <p>4. Надати пропозиції щодо охоронних та захисних зон з врахуванням містобудівних чинників.</p> <p>5. Надати пропозиції щодо централізованого водопостачання для всієї забудови населеного пункту. Розмістити вузол водопідготовки.</p> <p>6. Надати пропозиції щодо централізованої каналізації для всієї забудови населеного пункту.</p> <p>7. Передбачити резервування території під розміщення об'єктів культурно-побутового обслуговування населення, розміщення об'єктів торговельної інфраструктури.</p> <p>8. Приділити особливу увагу межі зон охорони пам'яток культурної спадщини в обов'язковому порядку нанести на основний кресленик генерального плану села, земельні ділянки що містять пам'ятку місцевого та національного значення.</p> <p>9. Передбачити зелені і паркові зони;</p> <p>10. Передбачити спортивно-ігрові майданчики;</p> |
| 12. Вимоги щодо врахування державних інтересів                                                                                    | Зазначити згідно умов від центрального органу виконавчої влади, що забезпечує формування   |

|   |   |
|---|---|
|   | державної політики у сфері містобудування та архітектури.   |
| 13. Вимоги щодо розрахунків на першу чергу реалізації                                              | На першу чергу реалізації генерального плану передбачити включення до території с. Широке території фермерських господарств, територію сонячної електростанції за межами населеного пункту, що встановлені органами державного земельного кадастру та надати пропозиції щодо комплексного благоустрою цих територій.             |
| 14. Додаткові вимоги.                                                                              | На підставі затвердженого Генерального плану населеного пункту та плану Зонування території подальшими етапами розробки містобудівної документації на місцевому рівні є «Детальні плани територій».   |
| 15. Кількість додаткових екземплярів графічних та текстових матеріалів.                            | Матеріали проектної документації виконати у 3-х примірниках, з яких – один примірник матеріалів проектної документації – для передачі відділу містобудування, архітектури та житлово-комунального господарства Запорізької райдержадміністрації, та на магнітних носіях.<br>Для текстових матеріалів -.pdf,<br>графічних -.tiff, |
| 16. Основні вимоги до програмного забезпечення, в тому числі геоінформаційних систем та технологій | Для Замовника:<br>для текстових матеріалів - <i>Adobe (Acrobat) Reader</i> .<br>-для графічних - <i>Microsoft Windows Photo Viewer</i> ,<br><i>Adobe Illustrator</i> , other image viewer.<br>Для розробника: <i>OpenOffice</i> , <i>AutoCad</i> , <i>ArcGIS</i> , або <i>Digital</i> s                                          |

Головний архітектор проекту



Прудка І.А.

*Шановний*



УКРАЇНА

ЗАПОРІЗЬКА ОБЛАСНА ДЕРЖАВНА АДМІНІСТРАЦІЯ

пр. Соборний, 164, м. Запоріжжя, 69107, тел/факс: (061) 224-63-81  
E-mail: adm@zoda.gov.ua; www.zoda.gov.ua Код ЄДРПОУ 00022504

15.05.2018 № 03806/08-27

На № 01-48/1006 від 12.04.2018

Широківському сільському голові  
Коротенку Д.О.

вул. Центральна, 1, с. Широке,  
Запорізький район, 70413

Про визначення та врахування  
державних та регіональних  
інтересів під час розроблення  
генерального плану села Широке

Шановний Денисе Олександровичу!

Обласна державна адміністрація розглянула лист Широківської сільської ради Запорізького району Запорізької області від 12.04.2018 № 01-48/1006 щодо визначення державних та регіональних інтересів при розробленні містобудівної документації «Генеральний план села Широке Запорізького району Запорізької області. Оновлення з розширенням меж населеного пункту та План зонування села Широке Запорізького району Запорізької області (у складі Генерального плану)» та повідомляє про таке.

Відповідно до планувальних рішень Схеми планування території Запорізької області, яка затверджена рішенням Запорізької обласної ради від 29.12.2011 № 4, територія села Широке за функціональним зонуванням відноситься до території з пріоритетним розвитком логістичних центрів складування, доробки та сортування вантажів та до Північної (Запорізької) підзони урбанізації - з критичним рівнем виробничо-містобудівного освоєння території.

На території рекомендується жорстке регулювання містобудівного розвитку з першочерговою реструктуризацією економічної бази та екологічною реабілітацією території.

Відповідно до аналізу рівня соціально-економічного розвитку окремих таксонів Запорізької області Запорізький район відноситься до 3 типу таксонів із середнім показником потенціалу та середнім рівнем соціально-економічного та містобудівного розвитку. Перспективи розвитку району цього типу пов'язано із використанням його переваг транспортно-географічного положення.

В районі планується розвиток багатоступеневої системи громадського обслуговування населення з розміщенням підприємств повсякденного та періодичного обслуговування.

Вх. 06-01-2018  
«15» 05 2018 р.  
М. 3000-2000-2000-776-1000

Планувальними рішеннями Схеми планування території Запорізької області на території села Широке є передбачено:

зона впливу автомобільного транспортного коридору Європа-Азія;  
розчистка р. Томаківка;  
відвід поверхневих вод з території села.

Необхідно виконати роботи з розробки розділу «Інженерно-технічні заходи цивільного захисту» (далі – ІТЗ ЦЗ), який є складовою частиною містобудівної документації (схеми планування території або генерального плану). Головним завданням розділу ІТЗ ЦЗ при плануванні території є створення містобудівних умов, забезпечення захисту населення і територій від надзвичайних ситуацій техногенного та природного характеру, їх наслідків з урахуванням особливостей соціально-економічного розвитку та природно-кліматичних умов. Розділ розробити згідно ДБН Б.1.1-5:2007 Склад, зміст, порядок розроблення, погодження та затвердження розділу інженерно-технічних заходів цивільного захисту (цивільної оборони) у містобудівній документації (перша та друга частини), де визначити конкретні рішення щодо забезпечення захисту населення і територій від надзвичайних ситуацій техногенного і природного характеру та їх наслідків.

При розробленні містобудівної документації необхідно врахувати обмеження господарської діяльності в межах берегової захисної смуги та водоохоронної зони затоки р. Томаківка.

На території та за сучасними межами с. Широке Запорізького району розташовані пам'ятки культурної спадщини місцевого значення, взяті на облік відповідно до Закону УРСР «Про охорону та використання пам'яток історії та культури».

Пам'ятки археології місцевого значення:

курган, охоронний № 4109, розташований за 0,3 км на схід від південно-східної околиці с. Широке, взятий на облік розпорядженням голови Запорізької облдержадміністрації від 11.03.1996 № 161;

курганний могильник з 18 курганів, охоронний № 1926, розташований за 0,5 км на захід від західної околиці с. Широке, взятий на облік рішенням виконкому Запорізької обласної ради народних депутатів від 23.10.1984 № 354;

курганний могильник з 4 курганів, охоронний № 1929, розташований за 0,5 км на схід від східної околиці с. Широке, взятий на облік рішенням виконкому Запорізької обласної ради народних депутатів від 23.10.1984 № 354;

курган, охоронний № 4111, розташований за 0,6 км на північний схід від північної околиці с. Широке, Взятий на облік розпорядженням голови Запорізької облдержадміністрації від 11.03.1996 № 161;

курганний могильник «Могила Гологанка» з 20 курганів, розташований за 1,0 км на захід від північно-західної околиці с. Широке, взятий на облік рішенням виконкому Запорізької обласної ради народних депутатів від 23.10.1984 № 354;

курганний могильник з 4 курганів, охоронний № 1928, розташований за 1,6 км на південний захід від південної околиці с. Широке, взятий на облік

рішенням виконкому Запорізької обласної ради народних депутатів від 23.10.1984 № 354;

курганний могильник з 5 курганів, охоронний № 1930, розташований за 2,2 км на північний захід від північної околиці с. Широке. Взятий на облік рішенням виконкому Запорізької обласної ради народних депутатів № 354 від 23.10.1984;

курган, охоронний № 4110, розташований за 2,6 км на схід від східної околиці с. Широке, взятий на облік розпорядженням голови Запорізької облдержадміністрації від 11.03.1996 № 161.

Рішенням виконкому Запорізької районної ради народних депутатів від 13.06.1985 № 225 встановлено охоронну зону для пам'яток археології Запорізького району в радіусі 5 м від підніжжя курганів.

Розпорядженням голови Запорізької облдержадміністрації від 11.03.1996 № 161 для пам'яток археології під охоронними №№ 4109, 4110, 4111 затверджено охоронну зону розміром 5 м від підніжжя курганів.

Пам'ятка археології місцевого значення, взята на облік відносно с. Ручаївка, розташована на відстані до 1,0 км від с. Широке - курган, охоронний № 2367, за 0,8 км на північний схід від північно-східної околиці с. Ручаївка та за 0,8 км на південь від південної околиці с. Широке. Взятий на облік рішенням виконкому Запорізької обласної ради народних депутатів від 26.11.1985 № 434.

Пам'ятка історії місцевого значення - Братська могила радянських воїнів, охоронний № 412, розташована у парку біля будинку культури с. Широке Широківської сільради. Взята на облік рішенням виконкому Запорізької обласної ради депутатів трудящих від 10.02.1971 № 55.

До Переліку об'єктів культурної спадщини у Запорізькій області наказом управління культури і туризму Запорізької облдержадміністрації від 28.11.2011 № 361-осн. включено щойно виявлений об'єкт археології - курган, розташований за 0,6 км на південь від південної околиці с. Широке Широківської сільради.

На південь від с. Широке знаходився відомий за картографічними матеріалами археологічний об'єкт - курган, що потребує обстеження для встановлення його фактичної наявності та вирішення питання про необхідність взяття на державний облік.

Існує вірогідність виявлення археологічних об'єктів - поселень, що не перебувають на державному обліку.

Рекомендованим є обстеження території населеного пункту фаховими спеціалістами на етапі виготовлення проекту містобудівної документації з метою забезпечення захисту об'єктів археології, що можуть бути виявлені у відповідності до ст. 37 Закону України «Про охорону культурної спадщини».

Під час виконання робіт з розробки містобудівної документації «Генеральний план села Широке Запорізького району Запорізької області. Оновлення з розширенням меж населеного пункту та План зонування села Широке Запорізького району Запорізької області (у складі Генерального

плану)» необхідним є врахування та дотримання вимог Законів України «Про охорону культурної спадщини» і «Про охорону археологічної спадщини».

Необхідно врахувати та відобразити інформацію про:

об'єкти державного земельного кадастру які входять до Генерального плану;

структуру і характеристику земель та віднесення їх до особливо цінних земель;

врахування вимог статті 23 Земельного кодексу України;

суб'єктів підприємницької діяльності у галузі топографо-геодезичної і картографічної діяльності, задіяних для оновлення (створення) картографічної основи;

систему географічних координат, в якій виконано оновлення картографічної основи, а також пункти Державної геодезичної мережі, використані при топографо-геодезичних і картографічних роботах;

передачу до Державного картографо-геодезичного фонду України копій геодезичних, топографічних, картографічних, гідрографічних, аерозйомочних матеріалів, що передбачено статтею 19 Закону України «Про топографо-геодезичну і картографічну діяльність».

Примірники креслень графічних матеріалів містобудівної документації на оптичних дисках повинні бути виконані у форматі геоінформаційних систем, що підтримують об'єктне представлення геопросторових даних.

Профільні геопросторові дані не пізніше 30 робочих днів після затвердження містобудівної документації повинні бути внесені до містобудівного кадастру Запорізького району. У разі не створення містобудівного кадастру Запорізького району, на час затвердження містобудівної документації місцевого рівня, зазначені матеріали повинні бути передані до Управління містобудування та архітектури облдержадміністрації та до відділу містобудування, архітектури та житлово-комунального господарства Запорізької райдержадміністрації.

Обласна державна адміністрація просить Вас врахувати державні та регіональні інтереси під час виконання робіт з розробки містобудівної документації «Генеральний план села Широке Запорізького району Запорізької області. Оновлення з розширенням меж населеного пункту та План зонування села Широке Запорізького району Запорізької області (у складі Генерального плану)».

З повагою

керівник апарату обласної  
державної адміністрації



З.М. Бойко



МІНІСТЕРСТВО РЕГІОНАЛЬНОГО РОЗВИТКУ, БУДІВНИЦТВА  
ТА ЖИТЛОВО-КОМУНАЛЬНОГО ГОСПОДАРСТВА УКРАЇНИ  
АТЕСТАЦІЙНА АРХІТЕКТУРНО-БУДІВЕЛЬНА КОМІСІЯ

Серія АА

№ 003280

**КВАЛІФІКАЦІЙНИЙ СЕРТИФІКАТ**  
відповідального виконавця окремих видів робіт (послуг),  
пов'язаних із створенням об'єкта архітектури

**архітектор**

(найменування професії)

Виданий про те, що

**Прудка Ірина Анатоліївна**

(прізвище, ім'я, по батькові)

пройшов(ла) професійну атестацію, що підтверджує його (її) відповідність кваліфікаційним вимогам у сфері діяльності, пов'язаної із створенням об'єктів архітектури, професійну спеціалізацію, необхідний рівень кваліфікації і знань.

Категорія: **архітектор**

Кваліфікаційний сертифікат видано згідно з рішенням Атестаційної архітектурно-будівельної комісії (далі - Комісія) від \_\_\_\_\_ № \_\_\_\_\_

(рішенням **відповідної** \_\_\_\_\_ секції Комісії  
від **13.07.2016** № **8-16** \_\_\_\_\_, затвердженням президією  
Комісії **14.07.2016** № **54-А** \_\_\_\_\_).

Зареєстрований у реєстрі атестованих осіб **14 липня** 20 **16** року  
за № **3280** \_\_\_\_\_.

Роботи (послуги), пов'язані із створенням об'єктів архітектури, спроможність виконання яких визначено кваліфікаційним сертифікатом: \_\_\_\_\_

**Розроблення містобудівної документації**

Дата видачі **15 липня** 20 **16** року

Голова Атестаційної архітектурно-будівельної комісії



(підпис)

**Білоус Сергій Ярославович**

(прізвище, ім'я, по батькові)