


с. Петропавлівка
Широківської сільської ради Запорізького району

План існуючого використання території,
схема існуючих планувальних обмежень
1:2000

Експлікація будівель та споруд		
№ п/п	Найменування	Примітка
1	Будівля магазину	Зруйнована
2	Електрична підстанція	
3	Сонячна підстанція	
4	Адміністративна будівля	
5	Кладовище	
6	Господарська будівля	

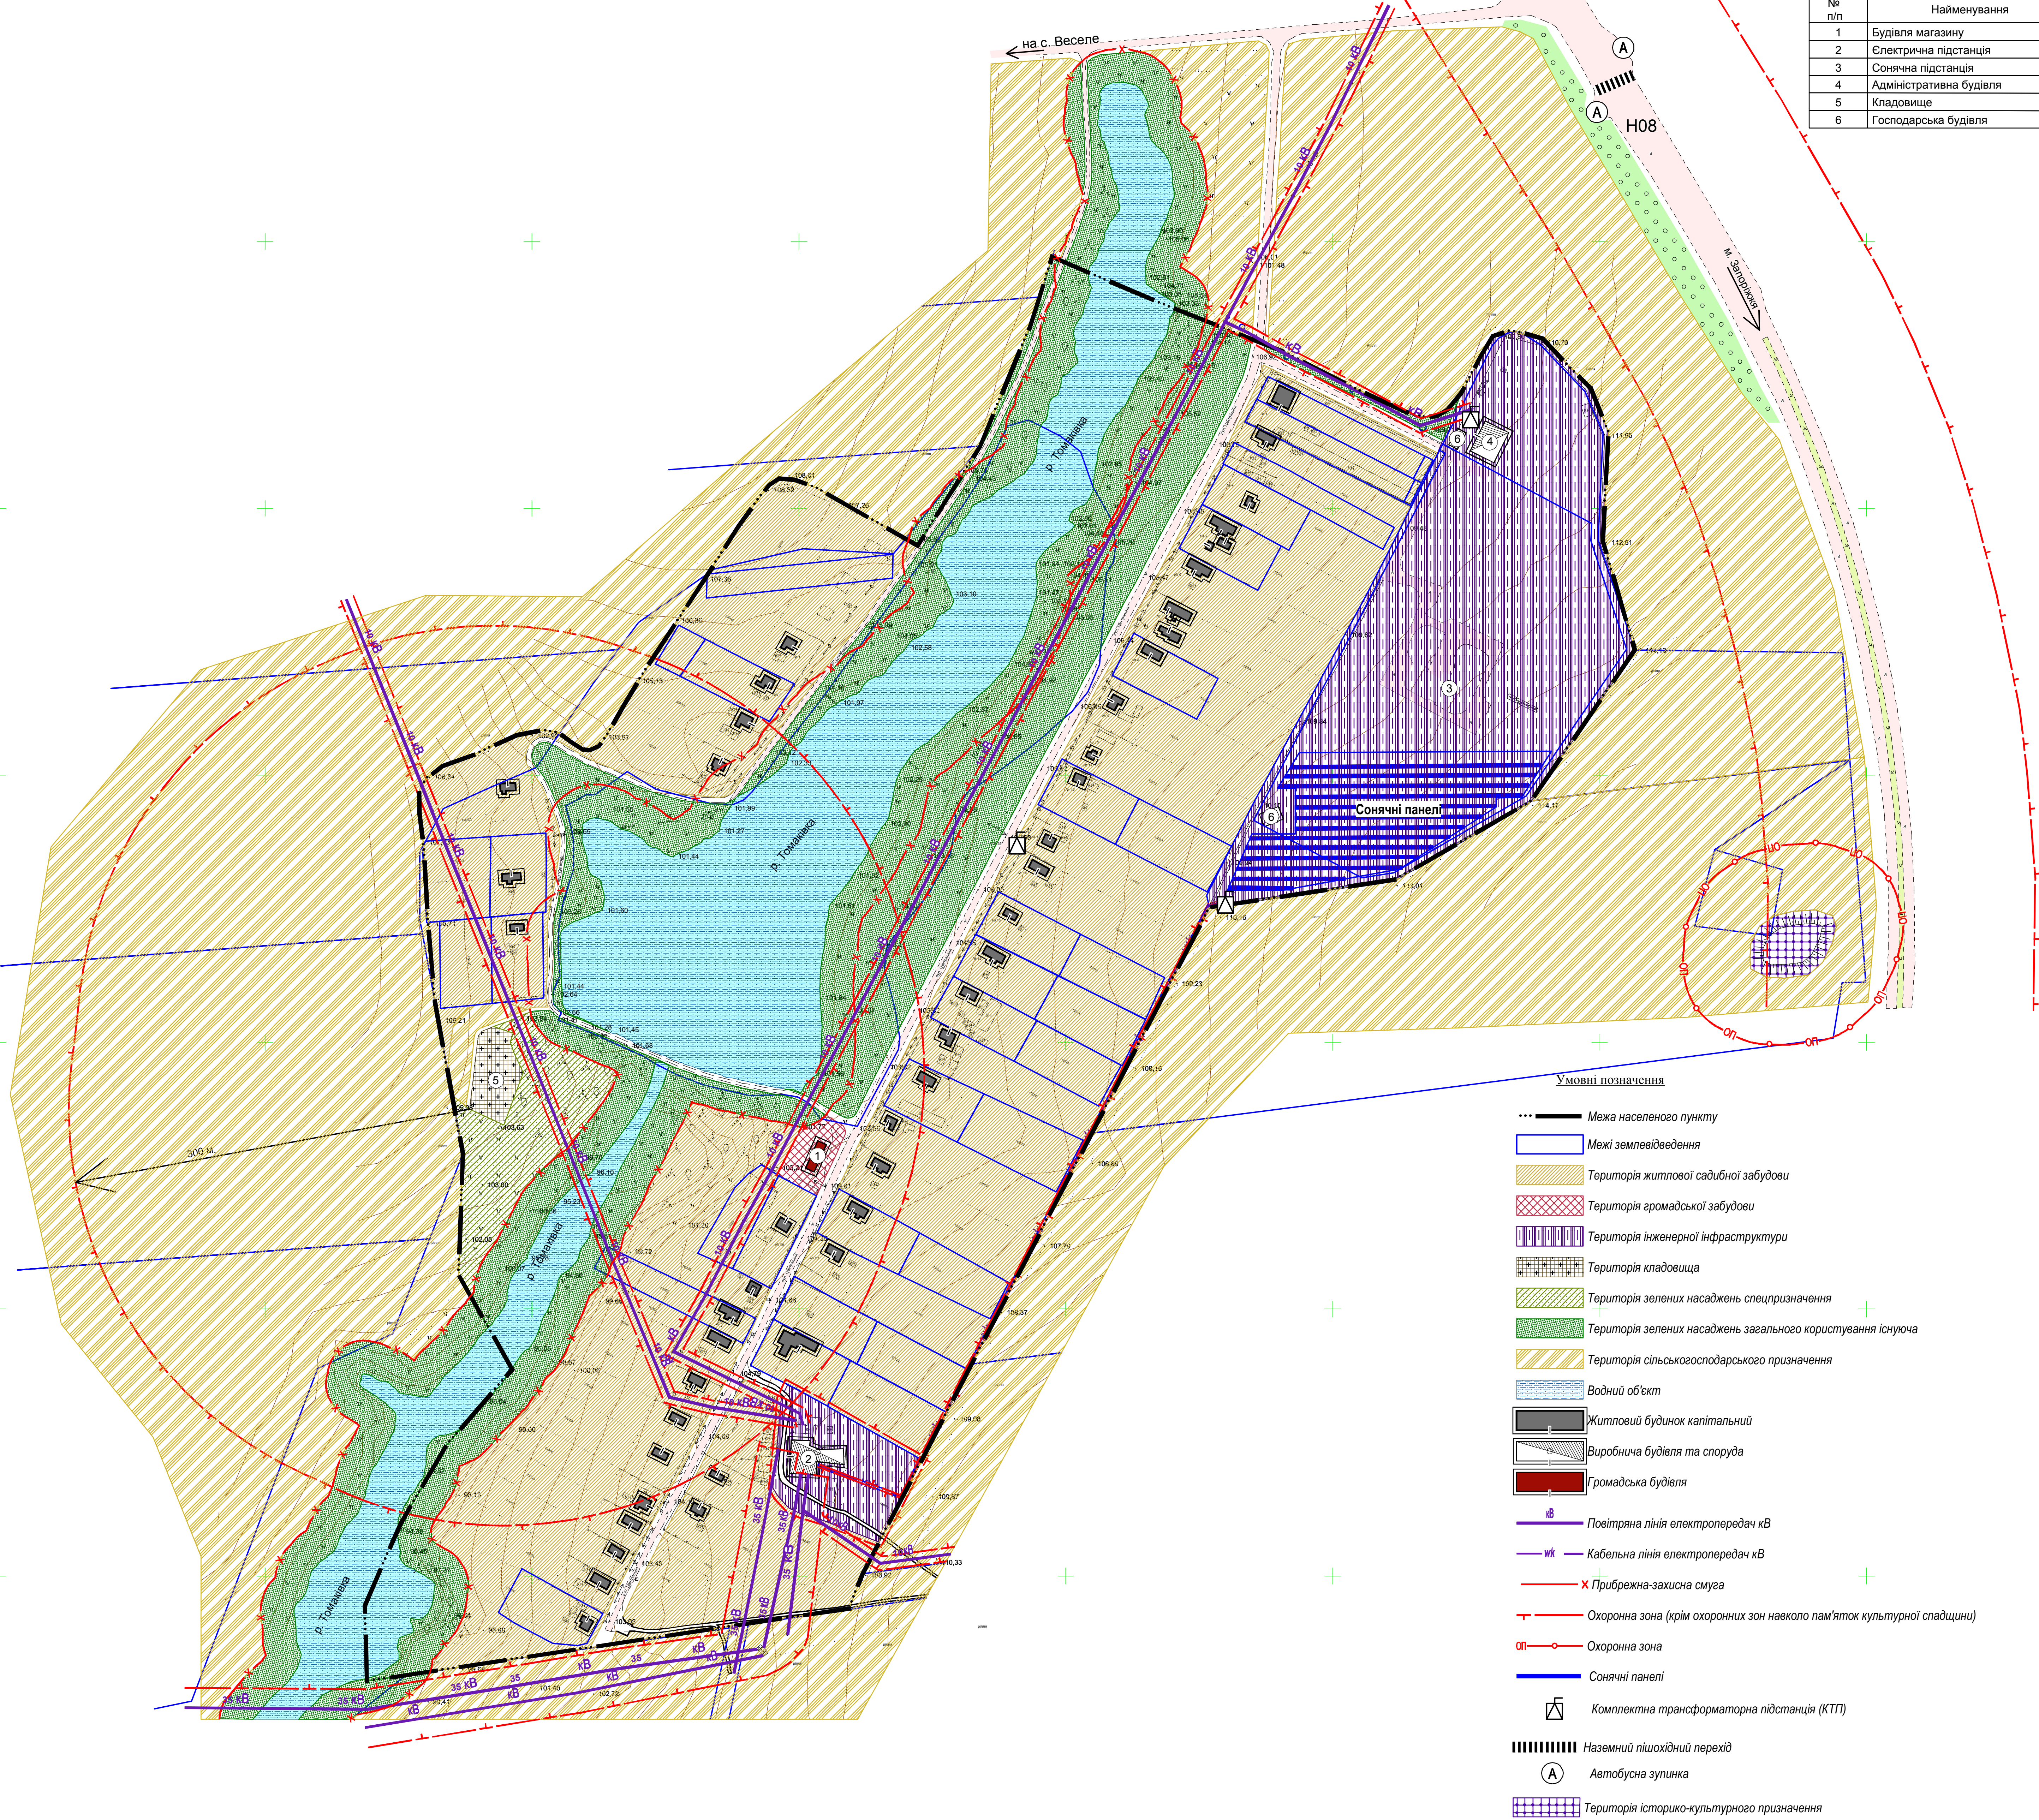

Примітка:
Топографічною основою креслення слугували
планшети М 1:2000 виконані ФГО-ПІ Божки В.В. 03.2017р.

						05.2017 ГП		
						Генеральний план, план зонування території села Петропавлівка Широківської сільської ради Запорізького району Запорізької області		
						Замовник: Широківська сільська рада Запорізького району Запорізької області		
						План існуючого використання території, схема існуючих планувальних обмежень 1:2000		
						Стадія	Архив	Архив
						ГП	2	7
						ПП "Стиль"		