


село Малишівка
Запорізького району, Запорізької області

План зонування території
М 1:2000

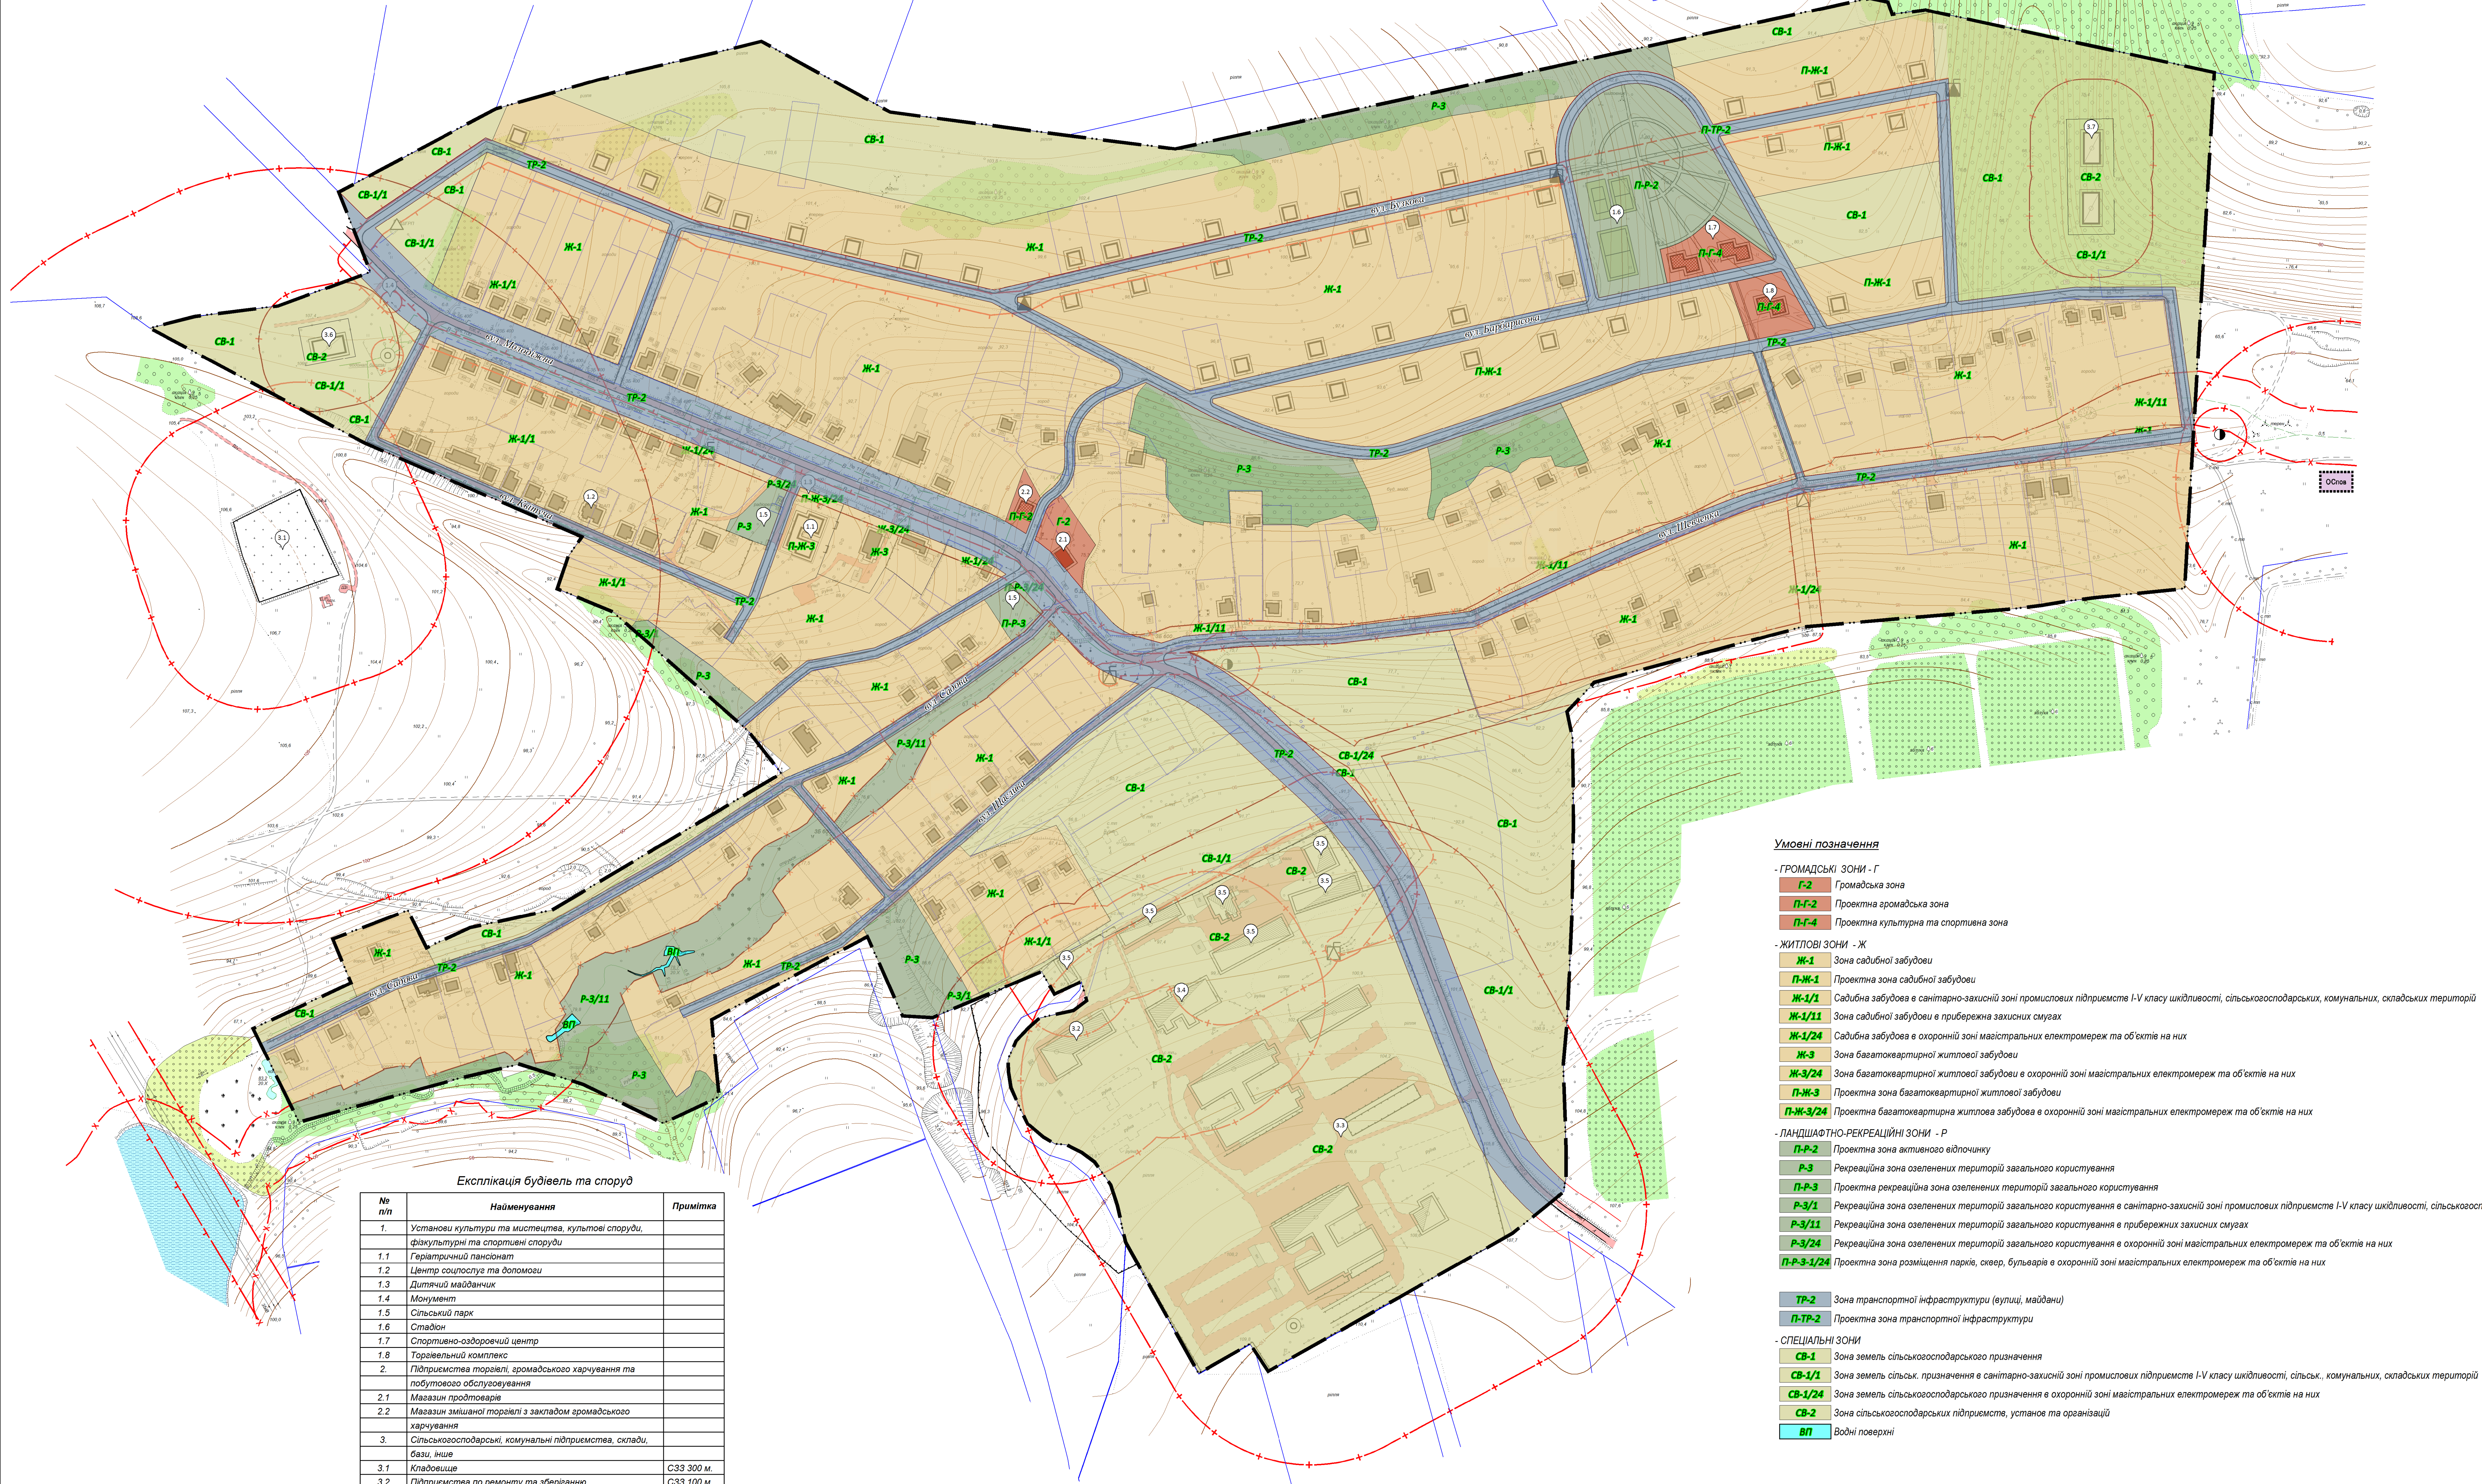

Експлікація будівель та споруд		
№ п/п	Найменування	Примітка
1.	Установи культури та мистецтва, культові споруди, фізкультурні та спортивні споруди	
1.1	Геріатричний пансіонат	
1.2	Центр соціальної та соціальної допомоги	
1.3	Дитячий майданчик	
1.4	Монумент	
1.5	Сільський парк	
1.6	Стадіон	
1.7	Спортивно-оздоровчий центр	
1.8	Торговельний комплекс	
2.	Підприємства торгівлі, громадського харчування та побутового обслуговування	
2.1	Магазин продовольства	
2.2	Магазин змішаної торгівлі з закладом громадського харчування	
3.	Сільськогосподарські, комунальні підприємства, склади, бази, інші	
3.1	Кладовище	СЗЗ 300 м.
3.2	Підприємства по ремонту та зберіганню сільськогосподарських машин	СЗЗ 100 м.
3.3	Фермерське господарство великої розсади худоби до 150 голів	СЗЗ 150 м.
3.4	Підприємство по переробці зерна	СЗЗ 100 м.
3.5	Склади зберігання зерна	СЗЗ 50 м.
3.6	Логістичний центр. Склади зберігання сільськогосподарської продукції	СЗЗ 50 м.
3.7	Склади зберігання фруктів	СЗЗ 50 м.

- Умовні позначення**
- ГРОМАДСЬКІ ЗОНИ - Г**
- Г-2** Громадська зона
 - П-Г-2** Проектна громадська зона
 - П-Г-4** Проектна культурна та спортивна зона
- ЖИТЛОВІ ЗОНИ - Ж**
- Ж-1** Зона садибної забудови
 - П-Ж-1** Проектна зона садибної забудови
 - Ж-1/1** Садибна забудова в санітарно-захисній зоні промислових підприємств I-V класу шкідливості, сільськогосподарських, комунальних, складських територій
 - Ж-1/11** Зона садибної забудови в прибережній захисній смузі
 - Ж-1/24** Садибна забудова в охоронній зоні магістральних електромереж та об'єктів на них
 - Ж-3** Зона багатоквартирної житлової забудови
 - Ж-3/24** Зона багатоквартирної житлової забудови в охоронній зоні магістральних електромереж та об'єктів на них
 - П-Ж-3** Проектна зона багатоквартирної житлової забудови
 - П-Ж-3/24** Проектна багатоквартирна житлова забудова в охоронній зоні магістральних електромереж та об'єктів на них
- ЛАНДШАФТНО-РЕКРЕАЦІЙНІ ЗОНИ - Р**
- П-Р-2** Проектна зона активного відпочинку
 - Р-3** Рекреаційна зона озеленених територій загального користування
 - П-Р-3** Проектна рекреаційна зона озеленених територій загального користування
 - Р-3/1** Рекреаційна зона озеленених територій загального користування в санітарно-захисній зоні промислових підприємств I-V класу шкідливості, сільськогосподарських, комунальних, складських територій
 - Р-3/11** Рекреаційна зона озеленених територій загального користування в охоронній зоні магістральних електромереж та об'єктів на них
 - Р-3/24** Рекреаційна зона озеленених територій загального користування в охоронній зоні магістральних електромереж та об'єктів на них
 - П-Р-3-1/24** Проектна зона розміщення парків, скверів, бульварів в охоронній зоні магістральних електромереж та об'єктів на них
- СПЕЦІАЛЬНІ ЗОНИ**
- СВ-1** Зона земель сільськогосподарського призначення
 - СВ-1/1** Зона земель сільського призначення в санітарно-захисній зоні промислових підприємств I-V класу шкідливості, сільських, комунальних, складських територій
 - СВ-1/24** Зона земель сільськогосподарського призначення в охоронній зоні магістральних електромереж та об'єктів на них
 - СВ-2** Зона сільськогосподарських підприємств, установ та організацій
 - ВП** Водні поверхні
- ТРАНСПОРТНІ ЗОНИ - Т**
- ТР-2** Зона транспортної інфраструктури (вулиці, майдани)
 - П-ТР-2** Проектна зона транспортної інфраструктури

						194/197П		
						Генеральний план села Малишівка Запорізького району Запорізької області		
						Оновлення з розширенням меж населеного пункту та план зонування села Малишівка Запорізького району Запорізької області (у складі генерального плану)		
Зміст	Кільк.	Арк.	№рек.	Підп.	Датум	Завдання	Склад	Архив
						Широкогірська сільська рада	П	7
ГЛП	Пруда					План зонування території		
Перекрес	Пруда					М 1:2000		
Розробив	Пруда					ФОРМ 1188 x 850		