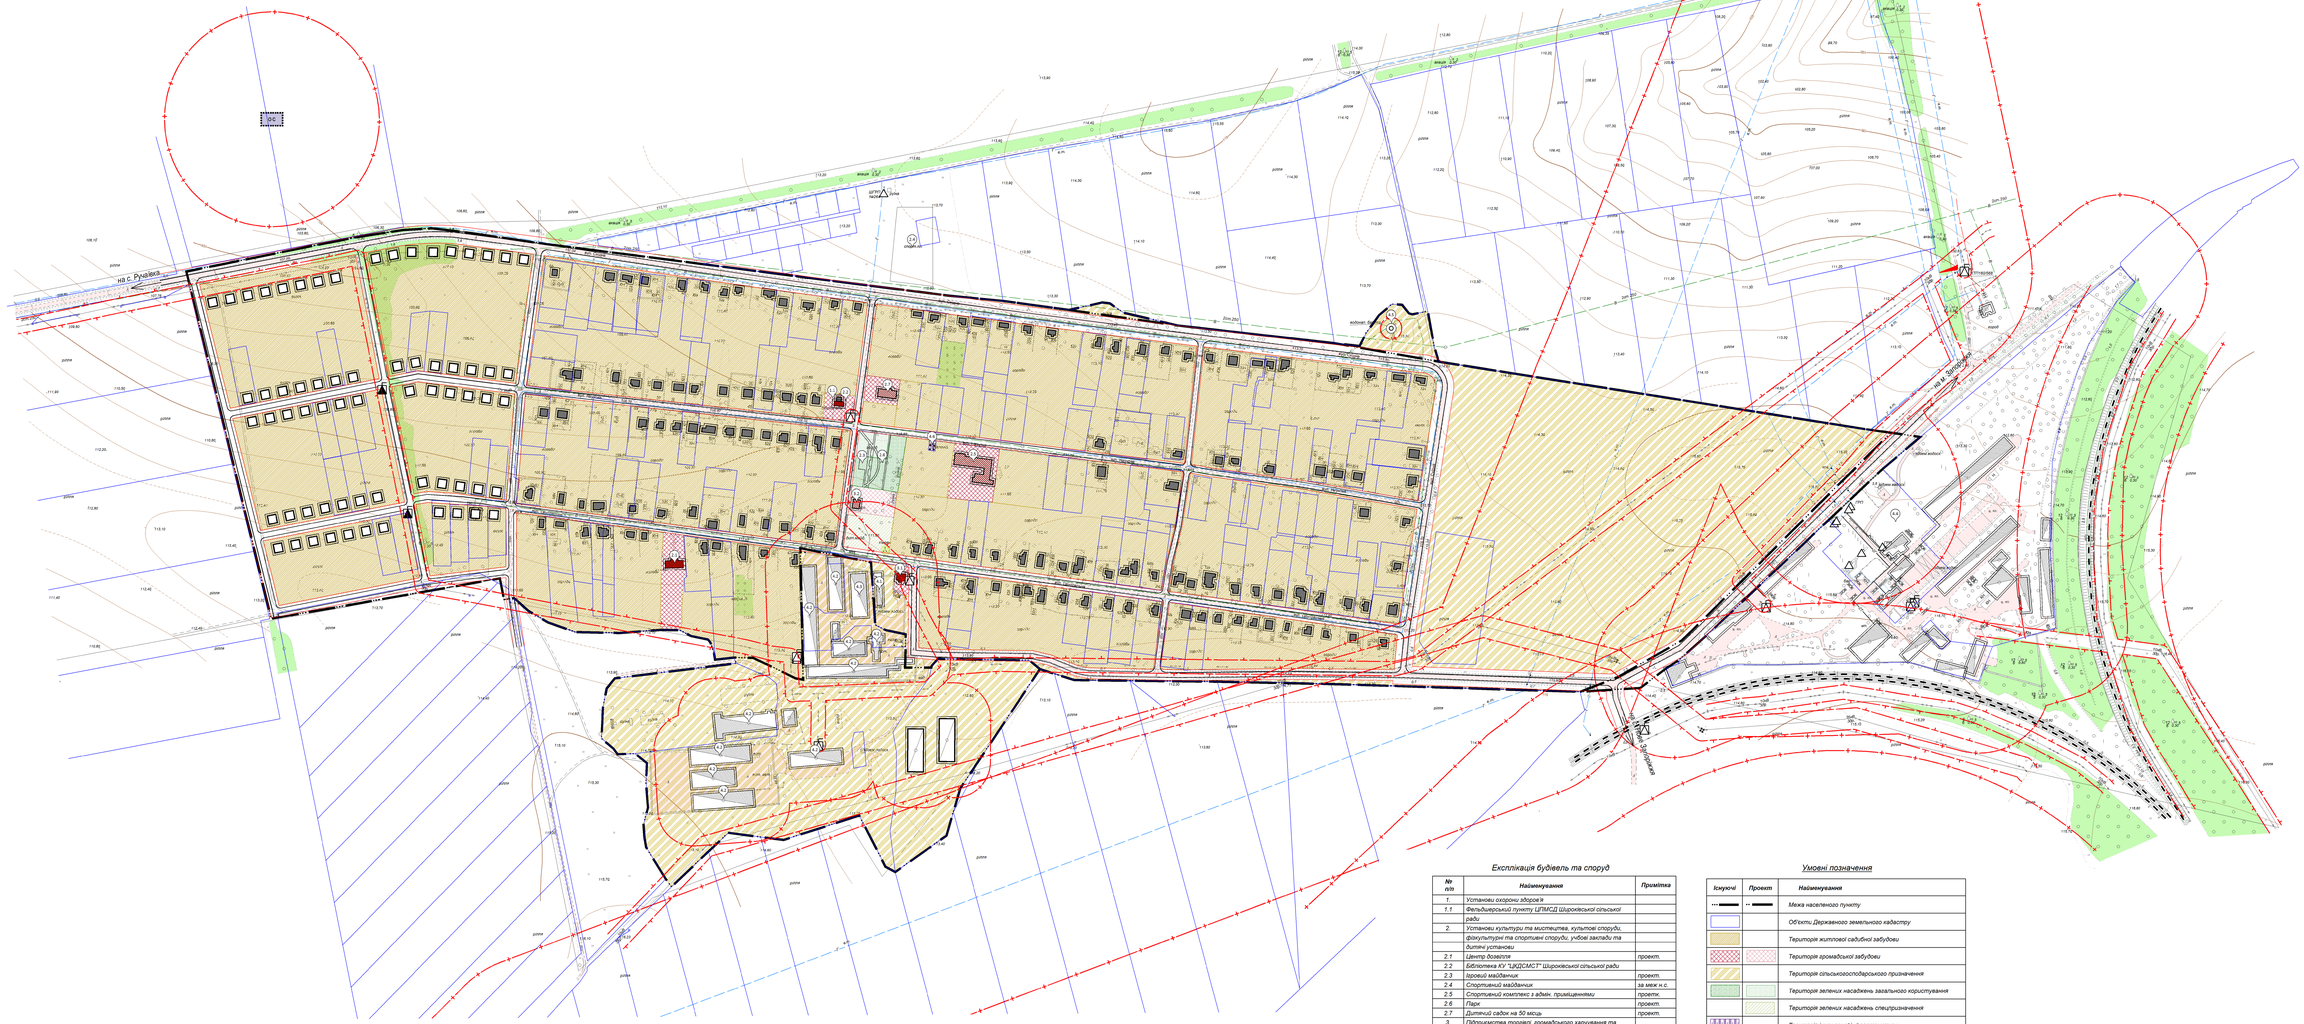

село Зеленопілля
Запорізького району, Запорізької області

Генеральний план (основне креслення).
Схема проектних планувальних обмежень
М 1:2000

Пн
З
С
ПД
ОС
на с. Ручаївка
вул. Східна
вул. Наукова
вул. Центральна
на м. Запоріжжя
на с. Нове Запоріжжя
ШГРП №26
руїна
спорт.пл.
водонап. башта
ТП160/568
ГРП
підзем.водосх.
дит.майд.
акація
рілля
город
2ст.250
10кВ
35кВ
1.1
2.1
2.2
2.3
2.4
2.5
2.6
2.7
3.1
3.2
4.1
4.2
4.3
4.4
4.5
4.6

Експлікація будівель та споруд

№ п/п	Найменування	Примітка
1.	Установи охорони здоров'я	
1.1	Фельдшерський пункту ЦПМСД Широківської сільської ради	
2.	Установи культури та мистецтва, культові споруди, фізкультурні та спортивні споруди, учбові заклади та дитячі установи	
2.1	Центр дозвілля	проект.
2.2	Бібліотека КУ "ЦКДСМСТ" Широківської сільської ради	
2.3	Ігровий майданчик	проект.
2.4	Спортивний майданчик	за меж н.с.
2.5	Спортивний комплекс з адмін. приміщеннями	проетк.
2.6	Парк	проект.
2.7	Дитячий садок на 50 місць	проект.
3.	Підприємства торгівлі, громадського харчування та побутового обслуговування	
3.1	Крамниця змішаної торгівлі	
3.2	Крамниця продовольчих та не продовольчих товарів	проект.
4.	Комунальні підприємства, склади, бази, інше	
4.1	Складська будівля	
4.2	Комплекс складських будівель СЗЗ 50 м.	
4.3	ТОК СЗЗ 100 м	
4.4	Виробнича база ВАТ АК Південтрансенерго СЗЗ 100 м	за меж. н.с.
4.5	Вежа Рожновського ЗСО 15 м.	
4.6	Вежа мобільного зв'язку	

Умовні позначення

Існуючі	Проект	Найменування
▬	▬	Межа населеного пункту
▭		Об'єкти Державного земельного кадастру
▨		Територія житлової садибної забудови
▨	▨	Територія громадської забудови
▨		Територія сільськогосподарського призначення
▨	▨	Територія зелених насаджень загального користування
	▨	Територія зелених насаджень спецпризначення
▥		Територія інженерної інфраструктури
■	□	Житловий будинок
■	▨	Громадська будівля
▨	□	Виробнича будівля та споруда
▬		Залізниця
	═	Червоні лінії
	═	Проїзд
△	▲	Комплектна трансформаторна підстанція (КТП)
△		Газорозподільний пункт (ГРП, ШРП)
◎		Водонапірна башта
┼		Охоронна зона
+		Санітарно-захисна зона
1+		1-й пояс зони санітарної охорони
	ОС	Очисні споруди

						28/03-2019-ГП		
Змін.	Кільк.	Арк.	№док.	Підп.	Дата	Генеральний план села Зеленопілля Запорізького району Запорізької області. Оновлення з розширенням меж населеного пункту та план зонування села Зеленопілля Запорізького району Запорізької області (у складі генерального плану)		
						Замовник: Широківська сільська рада	Стадія ГП	Аркуш 3
								Аркушів 7
ГАП		Прудка						
Перевірив						Генеральний план (основне креслення). Схема проектних планувальних обмежень М 1:2000	ФОП Прудка І.А.	
Розробив		Прудкий						

Формат 1800 x 1200