


с. Петропавлівка
Широківської сільської ради Запорізького району

Схема інженерного обладнання території
1:2000

Експлікація будівель та споруд		
№ п/п	Найменування	Примітка
1	Будівля магазину	Реконст.
2	Електрична підстанція	
3	Сонячна підстанція	
4	Адміністративна будівля	
5	Кладовище	
6	Територія зеленого туризму	
7	Спортивний майданчик	
8	Господарські будівлі	
9	Під'їзд пожежних машин до водозабору	

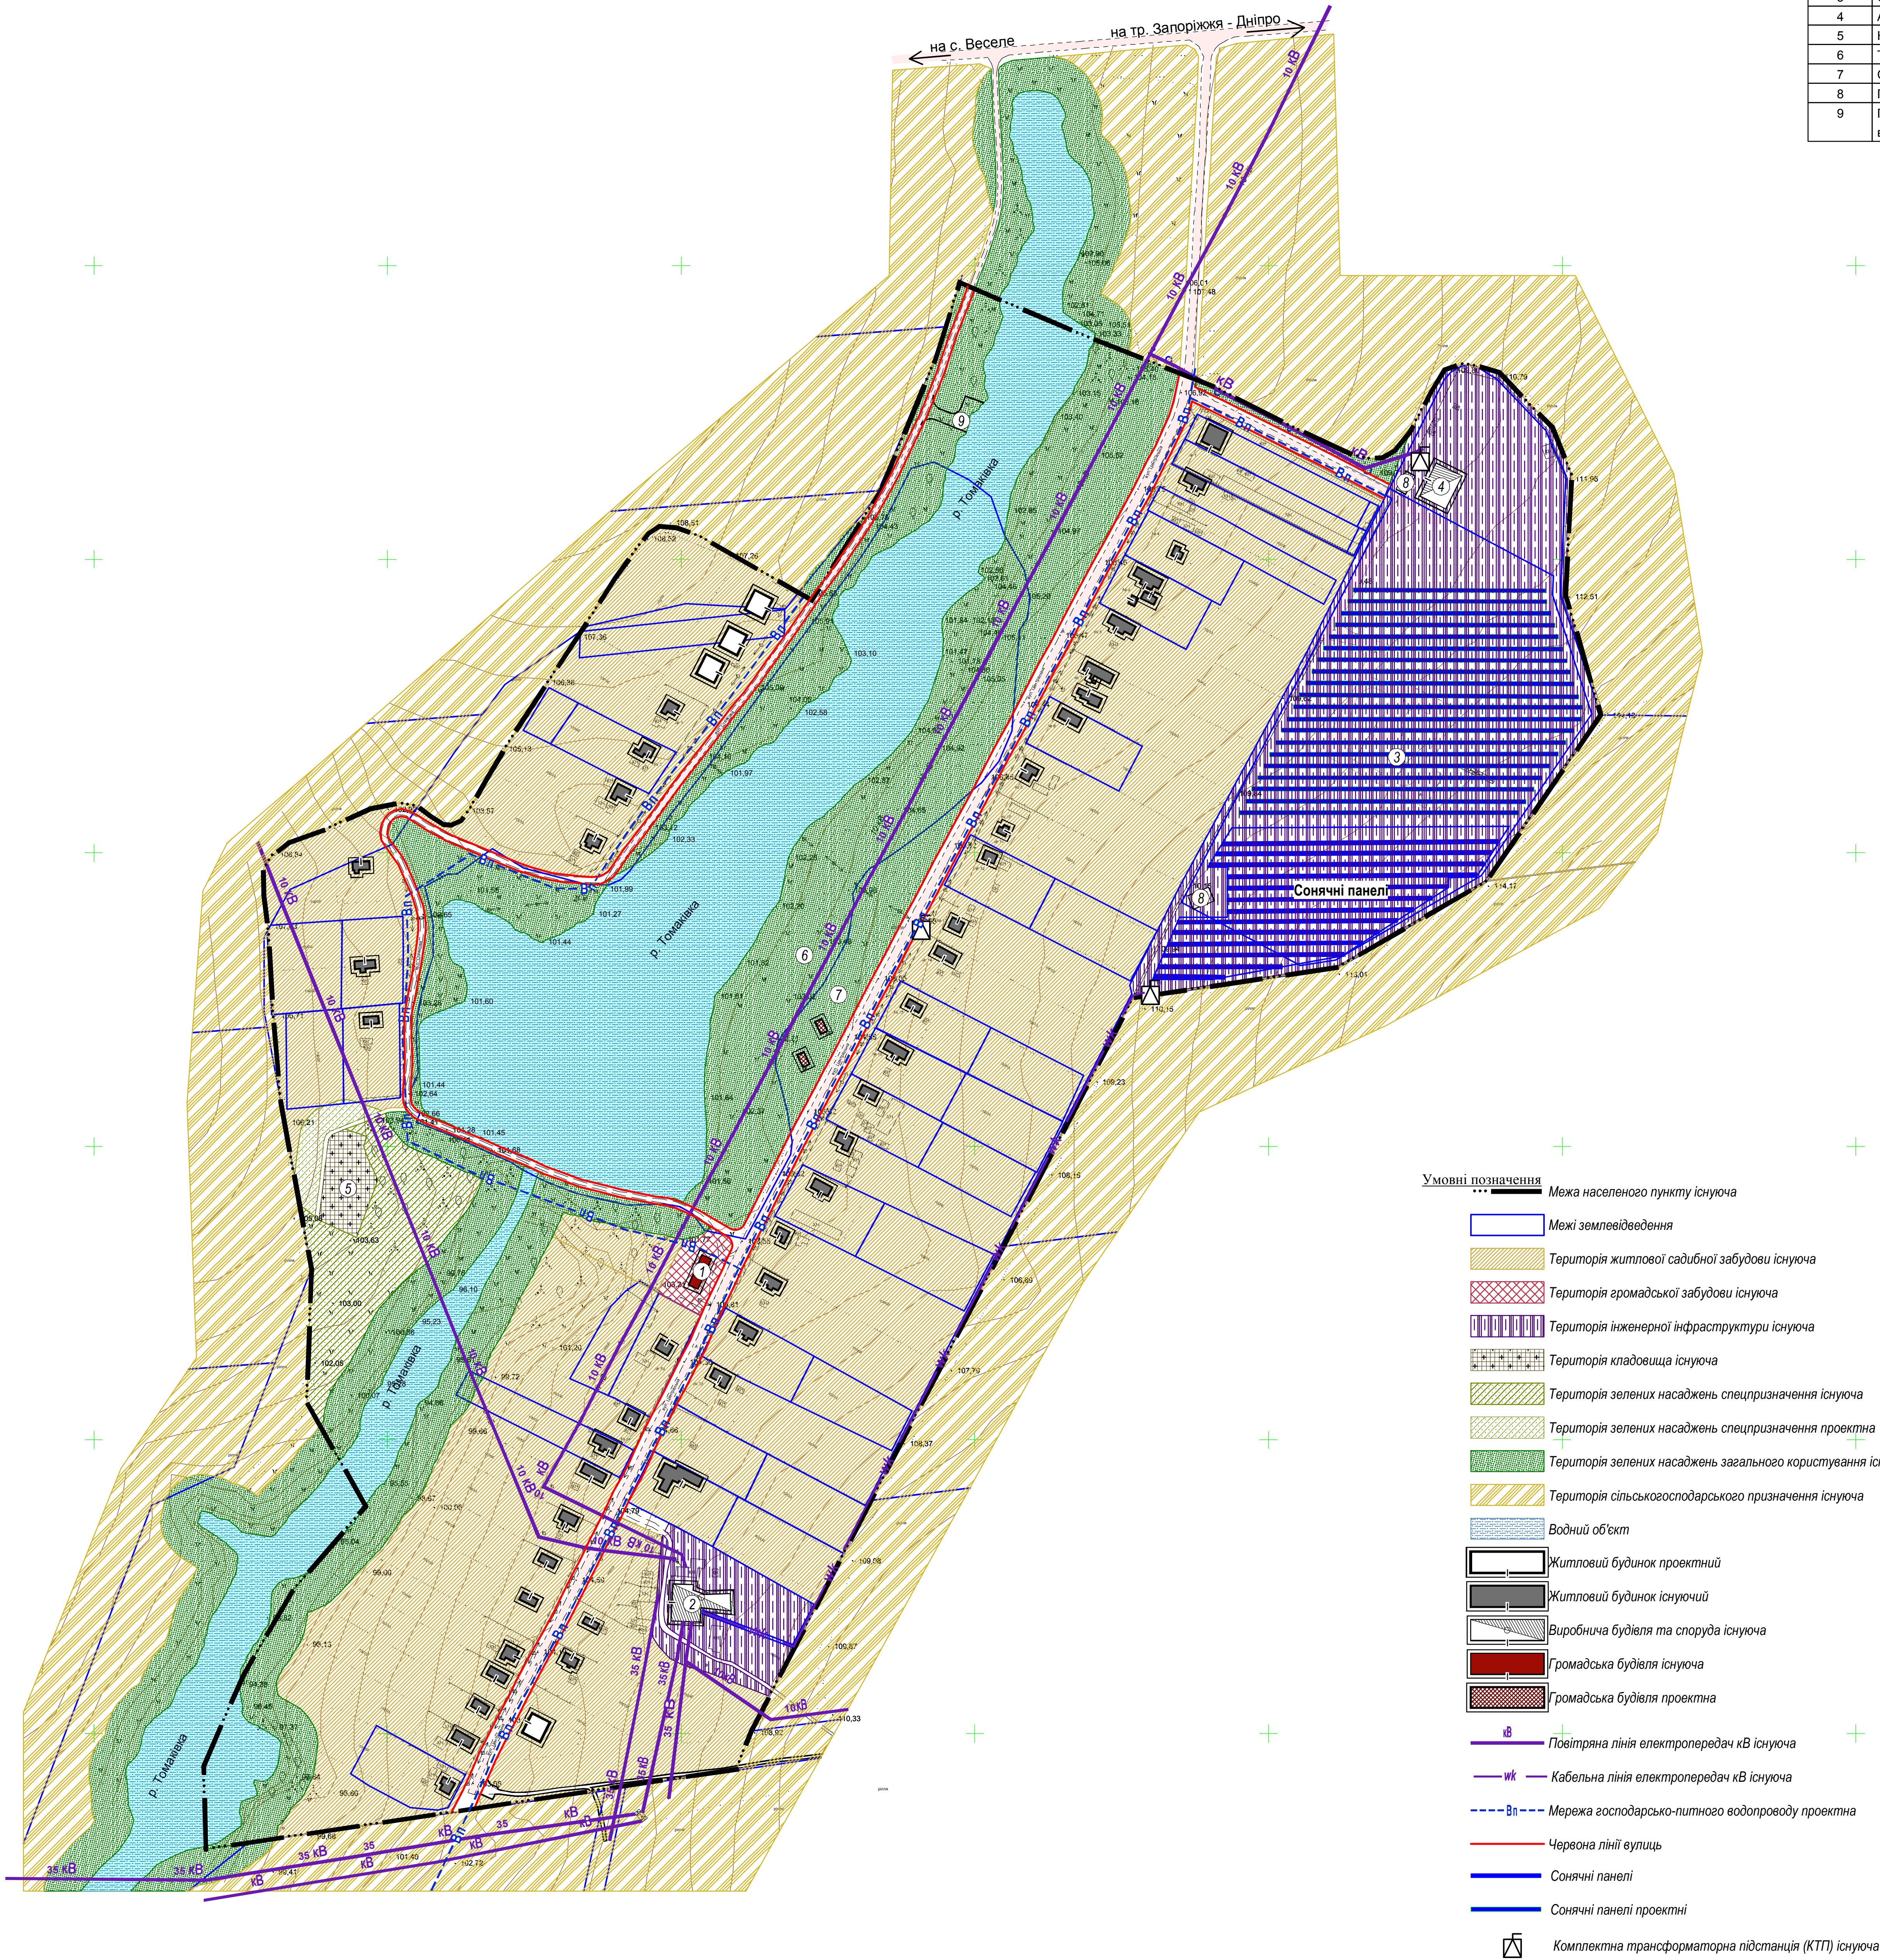

- Умовні позначення
- Межа населеного пункту існуюча
 - Межі землевідведення
 - Територія житлової садибної забудови існуюча
 - Територія громадської забудови існуюча
 - Територія інженерної інфраструктури існуюча
 - Територія кладовища існуюча
 - Територія зелених насаджень спецпризначення існуюча
 - Територія зелених насаджень спецпризначення проектна
 - Територія зелених насаджень загального користування існуюча
 - Територія сільськогосподарського призначення існуюча
 - Водний об'єкт
 - Житловий будинок проектний
 - Житловий будинок існуючий
 - Виробнича будівля та споруда існуюча
 - Громадська будівля існуюча
 - Громадська будівля проектна
 - кВ Повітряна лінія електропередач кВ існуюча
 - кВ Кабельна лінія електропередач кВ існуюча
 - кВ Мережа господарсько-питного водопроводу проектна
 - Червона лінії вулиць
 - Сонячні панелі
 - Сонячні панелі проектні
 - Комплектна трансформаторна підстанція (КТП) існуюча

Примітка:
Топографічною основою креслення слугували
планшети М 1:2000 виконані ФГО-ПІ Бояли В.В. 03.2017р.

						05.2017 ГП			
						Генеральний план, план зонування території села Петропавлівка Широківської сільської ради Запорізького району Запорізької області			
						Замовник: Широківська сільська рада Запорізького району Запорізької області			
						Схема інженерного обладнання території 1:2000			
Змін.	Кільк.	Арк.	№ док.	Підп.	Дата	Стадія	Аркуш	Аркуші	
ГАП	Пруда					ГП	5	7	
Перевіряв	Пруда					ПП "Стиль"			
Розробив	Пруда								