



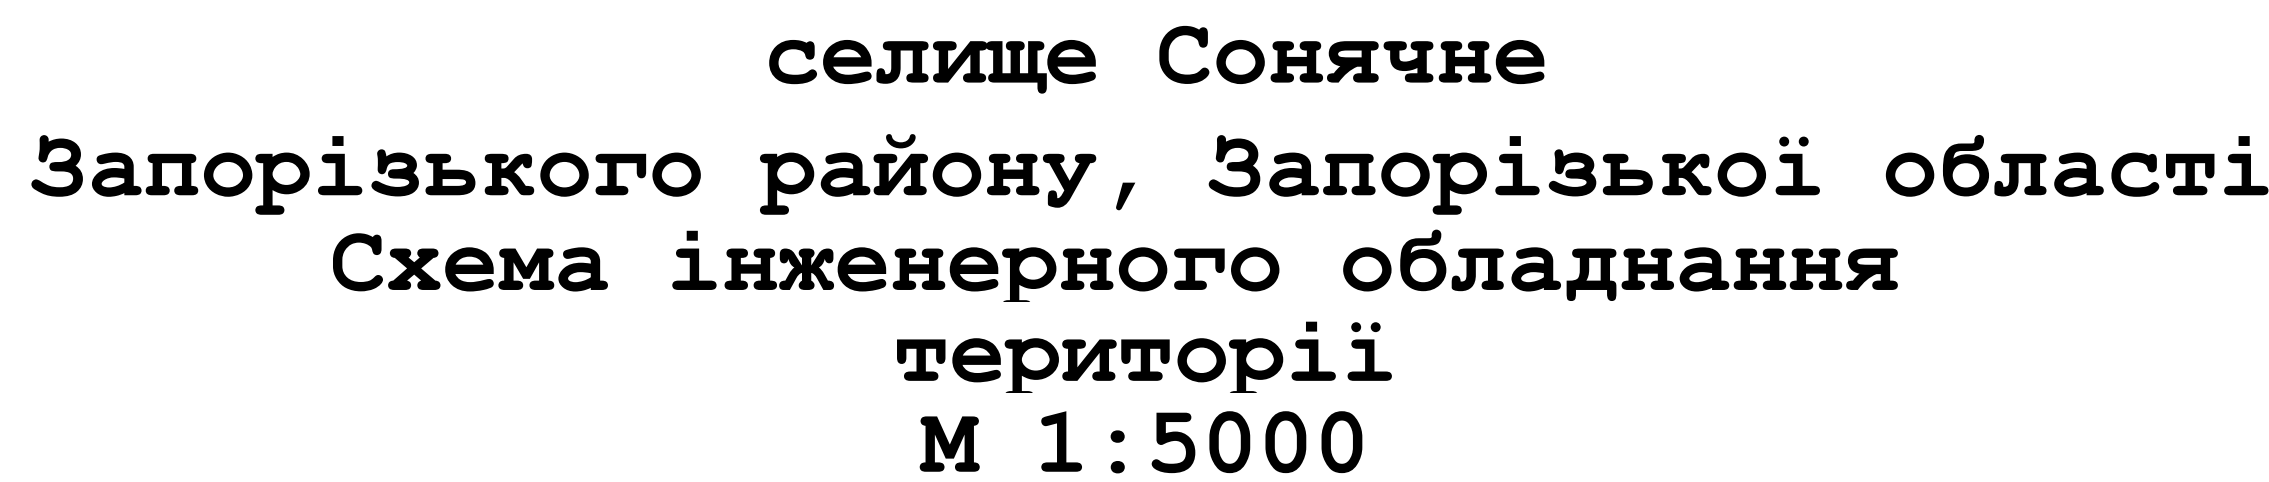

№ п/п	Найменування	Примітка
1	Інститут опійних культур НААН України	Іск.
2	Центр ПМД Широкоівської ОТГ	Проект
3	Адміністративна будівля	Проект
4	Спортивний майданчик (футбольне поле з штучним покриттям)	Проект
5	Спортивно-оздоровчий комплекс	Проект
6	Спортивно-оздоровчий центр	Проект
7	Карантинний розсадник рослин	Іск.
8	Відоме житло	Проект
9	Складські приміщення СЗЗ 50 м.	Проект
10	Ботанічний заказник "Ділина балка"	Іск.
11	Електрична підстанція ОЗ 3 м.	Іск.
12	Базеофункціональний торгівельно-виставковий та логістичний комплекс	Проект
13	Школа	Проект
14	Дитячий садок	Проект
15	Церква	Іск.
16	Гаражні кооперативи	Іск.
17	Склади промтоварів СЗЗ 50 м.	Іск.
18	Парк	Проект
19	Насосна станція	Проект
20	Газові модулі СЗЗ 100 м.	Іск.
21	Торгов. виставкової та логістичні центри	Проект
22	Дачні кооперативи	Іск.
23	Адміністративний центр, магазин	Проект
24	Насосна станція теплових мереж СЗЗ 15 м.	Іск.
25	Автомийка СЗЗ 50 м.	Іск.
26	АЗС СЗЗ 50 м.	Іск.
27	Адміністративно - торговельний центр	Проект
28	Ландшафтний заказник "Балка Хуторська"	Іск.

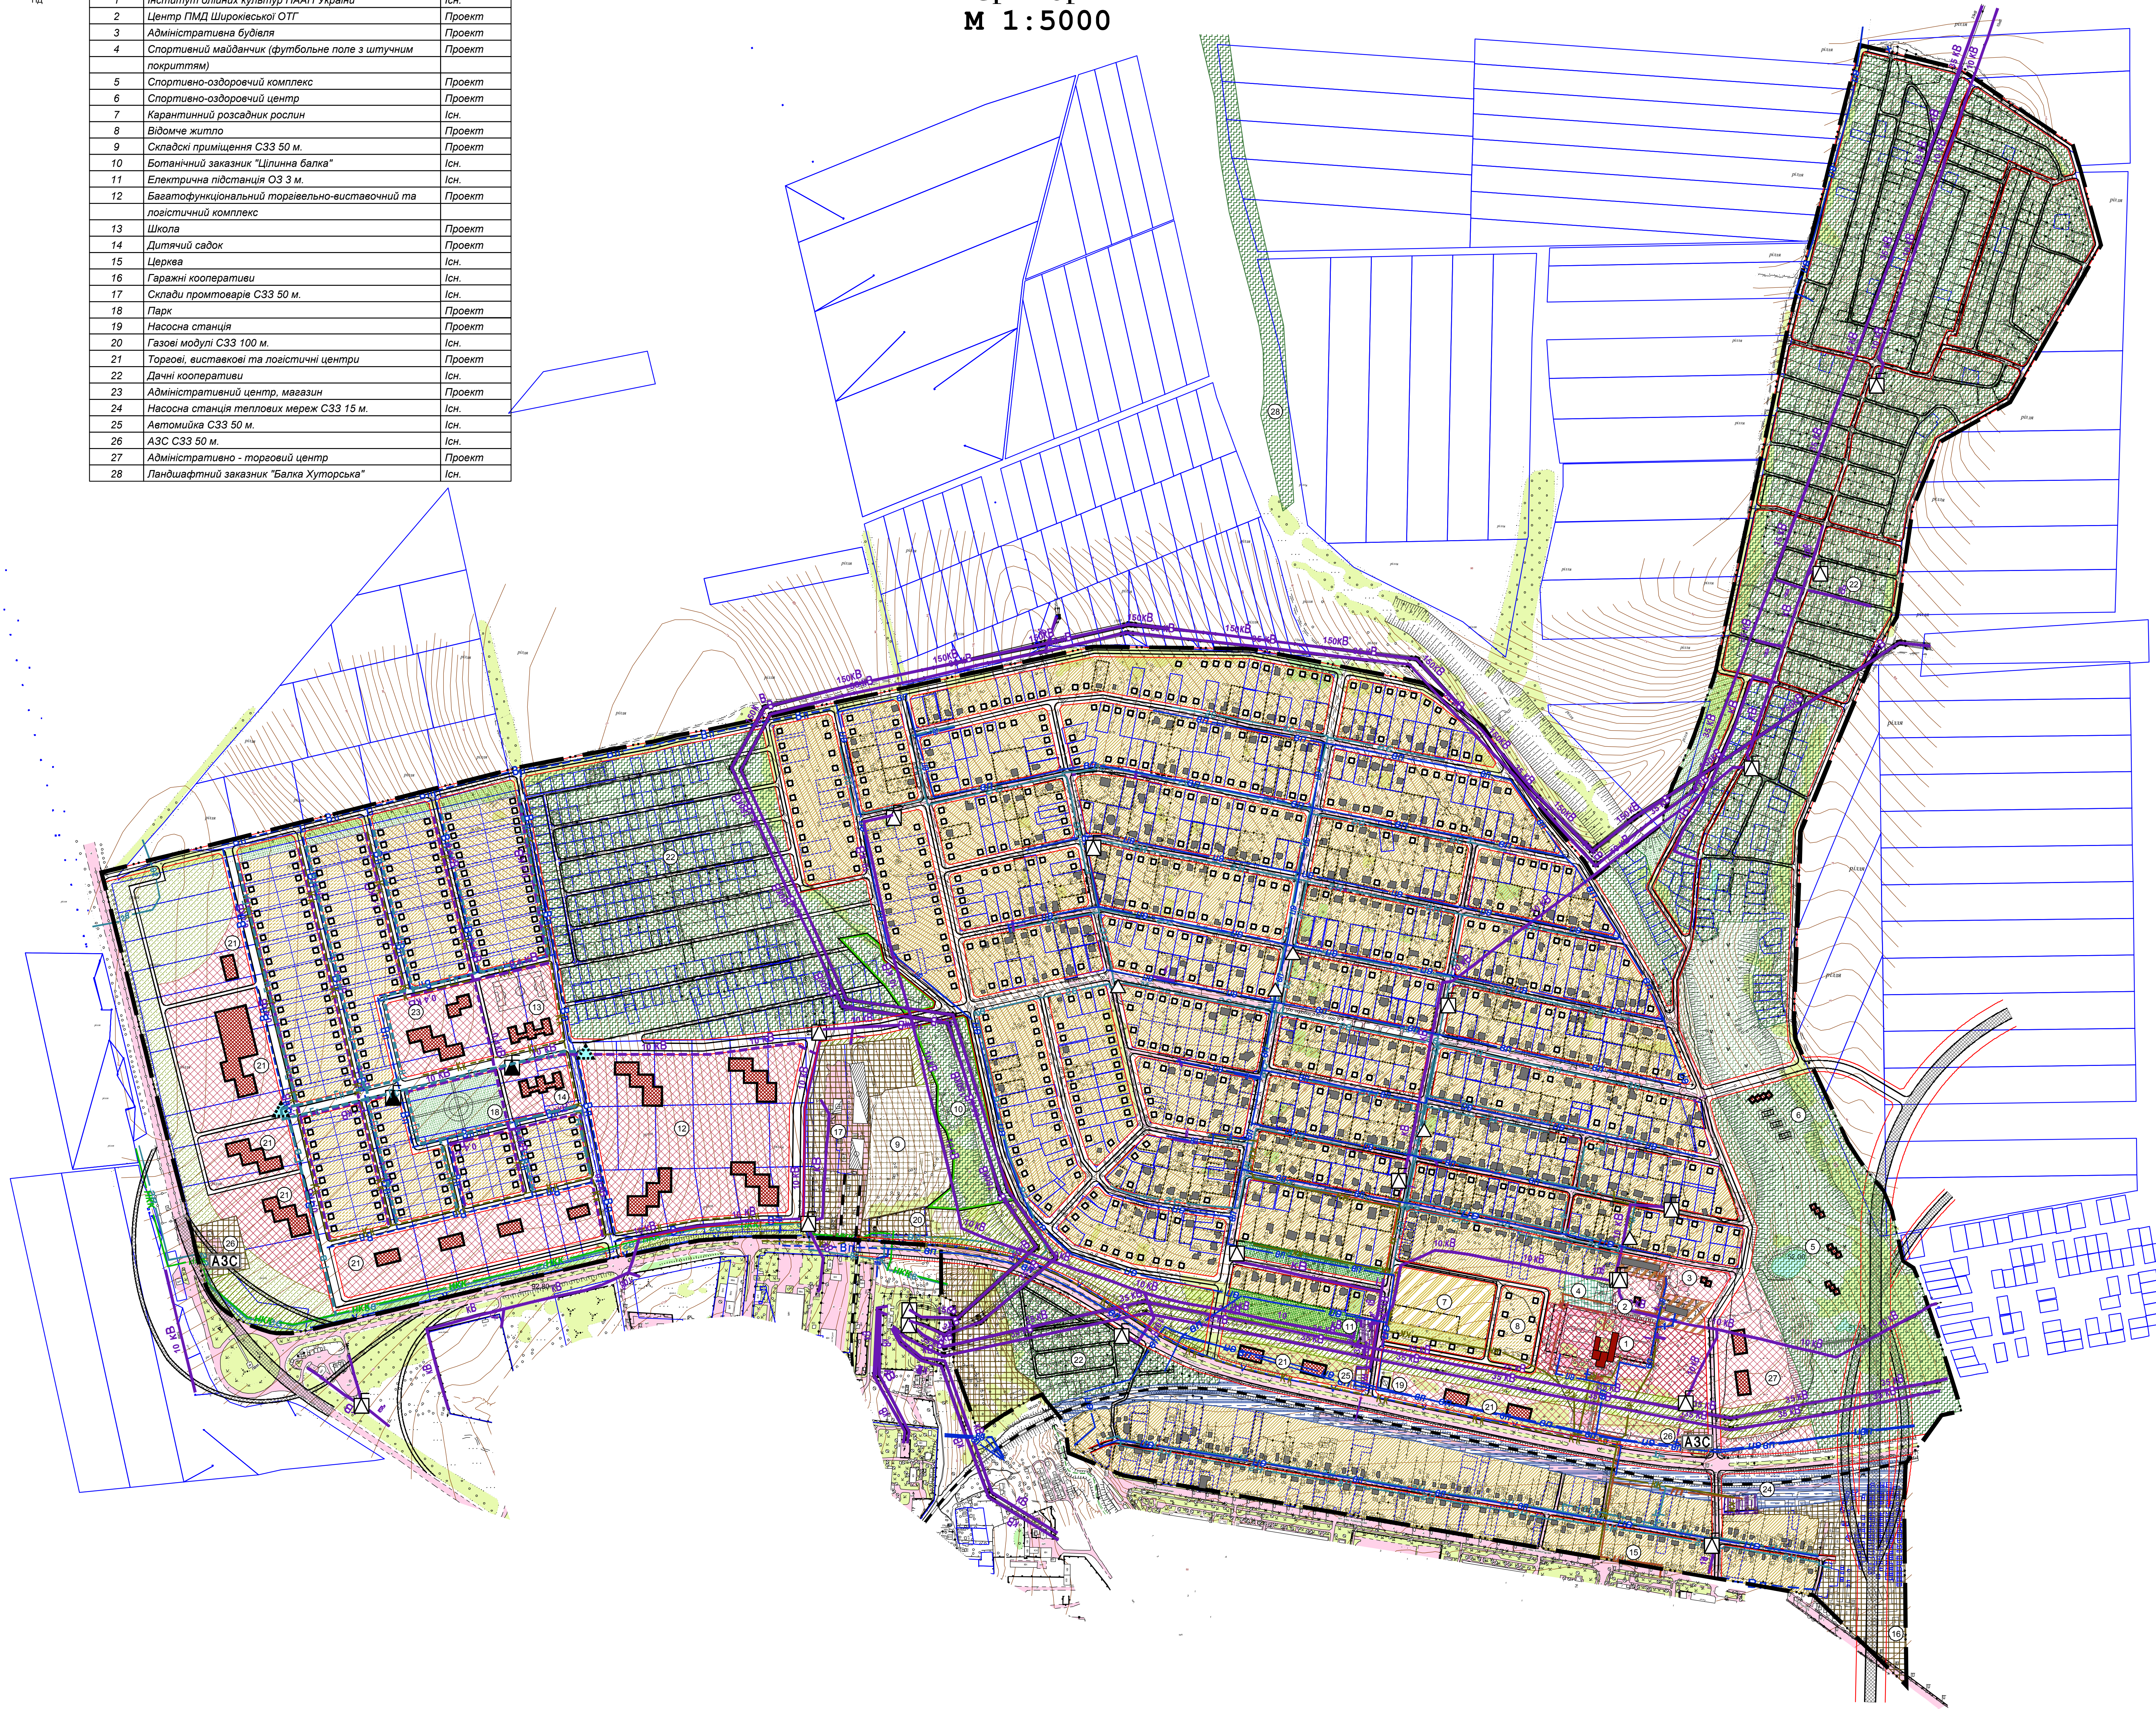

Умовні позначення		
Існуючі	Проект	Найменування
		Межа населеного пункту
		Межі землеволодіння
		Територія житлової садибної забудови
		Територія сільськогосподарського призначення
		Територія житлової багатоквартирної забудови
		Територія громадської забудови
		Територія транспортної інфраструктури
		Територія інженерної інфраструктури
		Територія комунальних об'єктів
		Територія рекреаційного призначення
		Територія оздоровчого призначення
		Територія зелених насаджень загального користування
		Територія зелених насаджень спеціального призначення
		Межі території ПТО місцевого значення
		Житловий будинок
		Виробнича будівля (споруда)
		Громадська будівля
		A3C
		Пробізд
		Чересні лінії
		Запізнювач
		Комплектна трансформаторна підстанція (КТП)
		Газорозподільний пункт (ГРП, ШРП)
		Теплова мережа з водним теплоносієм
		Кабельна лінія електропередач
		Поверхнєві лінії електропередач
		Мережа господарсько-питного водопроводу
		Самостійна каналізаційна мережа комунальної каналізації
		Напірна каналізаційна мережа комунальної каналізації
		Газопровід високого тиску
		Газопровід середнього тиску
		Газопровід низького тиску
		Телефонна каналізація

[illegible]