


село Придніпровське
Запорізького району, Запорізької області



Схема вулично - дорожньої мережі, міського (сільського)
та зовнішнього транспорту
М 1:2000

Умовні позначення		
Існуючі	Проект	Найменування
—	—	Межа населеного пункту
□	□	Об'єкти Державного земельного кадастру
▨	▨	Територія житлової садибної забудови
▩	▩	Територія громадської забудови
▧	▧	Територія сільськогосподарського призначення
▦	▦	Територія кладовища
▥	▥	Територія зелених насаджень спеціального призначення
▤	▤	Територія зелених насаджень загального користування
▣	▣	Територія інженерної інфраструктури
■	■	Житловий будинок
■	■	Громадська будівля
□	□	Комплексна трансформаторна підстанція (КТТП)
□	□	Газорозподільний пункт (ГРП, ШРП)
□	□	Каналізаційна насосна станція
□	□	Очисні споруди каналізації
□	□	Станція очищення поверхневих стічних вод
—	—	Червоні лінії
—	—	Проездна частина з твердим покриттям
▤	▤	Наземний пішохідний перехід
—	—	Основний шлях руху пішоходів
—	—	Маршрут автобуса
Ⓐ	Ⓐ	Зупинка громадського транспорту

Експлікація будівель та споруд		
№ п/п	Найменування	Примітка
1	Крамниця	
2	Кладовище (тілягає закриття)	СЗЗ - 300 м.
3	Садибне товариство "Суверен"	
4	Обслуговуючий садовий кооператив "Підія"	
5	Садове товариство "Таврія-2"	
6	Садове товариство "Привілля"	
7	Садове товариство "Сільський будівельник"	
8	Садове товариство "Привілля"	
9	Обслуговуючий садовий кооператив "Славутич-2"	
10	Базатофункціональний громадський центр	
11	Крамниця змішаної торгівлі	
12	Будівля побутового обслуговування населення	
13	Підприємства громадського харчування	
14	Садове товариство "Колос"	
15	Трансформаторна підстанція	ОЗ - 3 м.
16	Каплиця	
17	Пляж, яхт клуб	
18	Каналізаційна насосна станція	СЗЗ - 15 м.
19	Очисні споруди каналізації	СЗЗ - 150 м.
20	Станція очищення поверхневих стічних вод	

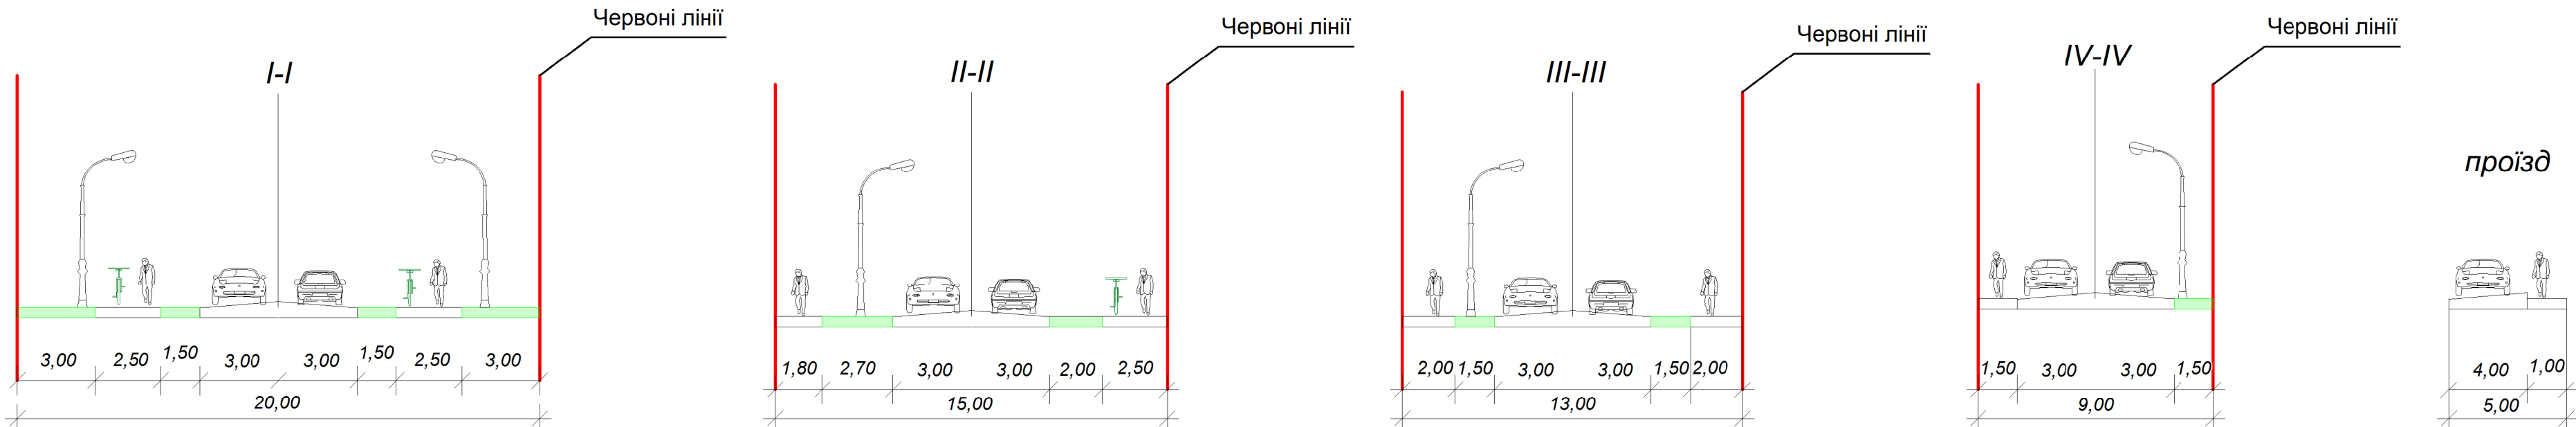

12821/1-171					
Генеральний план села Придніпровське Запорізького району Запорізької області. Описання з розширенням меж населеного пункту та планування села Придніпровське Запорізького району Запорізької області (у складі загальної планування).					
Зем.	Карт.	Арх.	Мех.	Підп.	Дат.
Замовник: Широкивська сільська рада, Запорізького району Запорізької області					
Складає: Пруда					
Перевіряє: Пруда					
Розробляє: Пруда					
Схема вулично - дорожньої мережі, міського (сільського) та зовнішнього транспорту М 1:2000					
Формат 900 x 1200					