


Експлікація будівель та споруд

№ п/п	Найменування	Примітка
1	Інститут олійних культур НААН України	Існ.
2	Центр ПМД Широцької ОТГ	Проект
3	Адміністративна будівля	Проект
4	Спортивний майданчик (футбольне поле з штучним покриттям)	Проект
5	Спортивно-оздоровчий комплекс	Проект
6	Спортивно-оздоровчий центр	Проект
7	Карантинний розсадник рослин	Існ.
8	Відомче житло	Проект
9	Складські приміщення СЗЗ 50 м.	Проект
10	Ботанічний заказник "Шлинина балка"	Існ.
11	Електрична підстанція ОЗ 3 м.	Існ.
12	Базовофункціональний торгівельно-виставочний та логістичний комплекс	Проект
13	Школа	Проект
14	Дитячий садок	Проект
15	Церква	Існ.
16	Гаражні кооперативи	Існ.
17	Склади промтоварів СЗЗ 50 м.	Існ.
18	Парк	Проект
19	Насосна станція	Проект
20	Газові модулі СЗЗ 100 м.	Існ.
21	Торгові, виставкові та логістичні центри	Проект
22	Дачні кооперативи	Існ.
23	Адміністративний центр, магазин	Проект
24	Насосна станція теплових мереж СЗЗ 15 м.	Існ.
25	Автомобільна СЗЗ 50 м.	Існ.
26	АЗС СЗЗ 50 м.	Існ.
27	Адміністративно - торговий центр	Проект
28	Ландшафтний заказник "Балка Хуторська"	Існ.


селище Сонячне
Запорізького району, Запорізької області
Схема вулично-дорожньої мережі,
міського (сільського) та
зовнішнього транспорту
1:5000

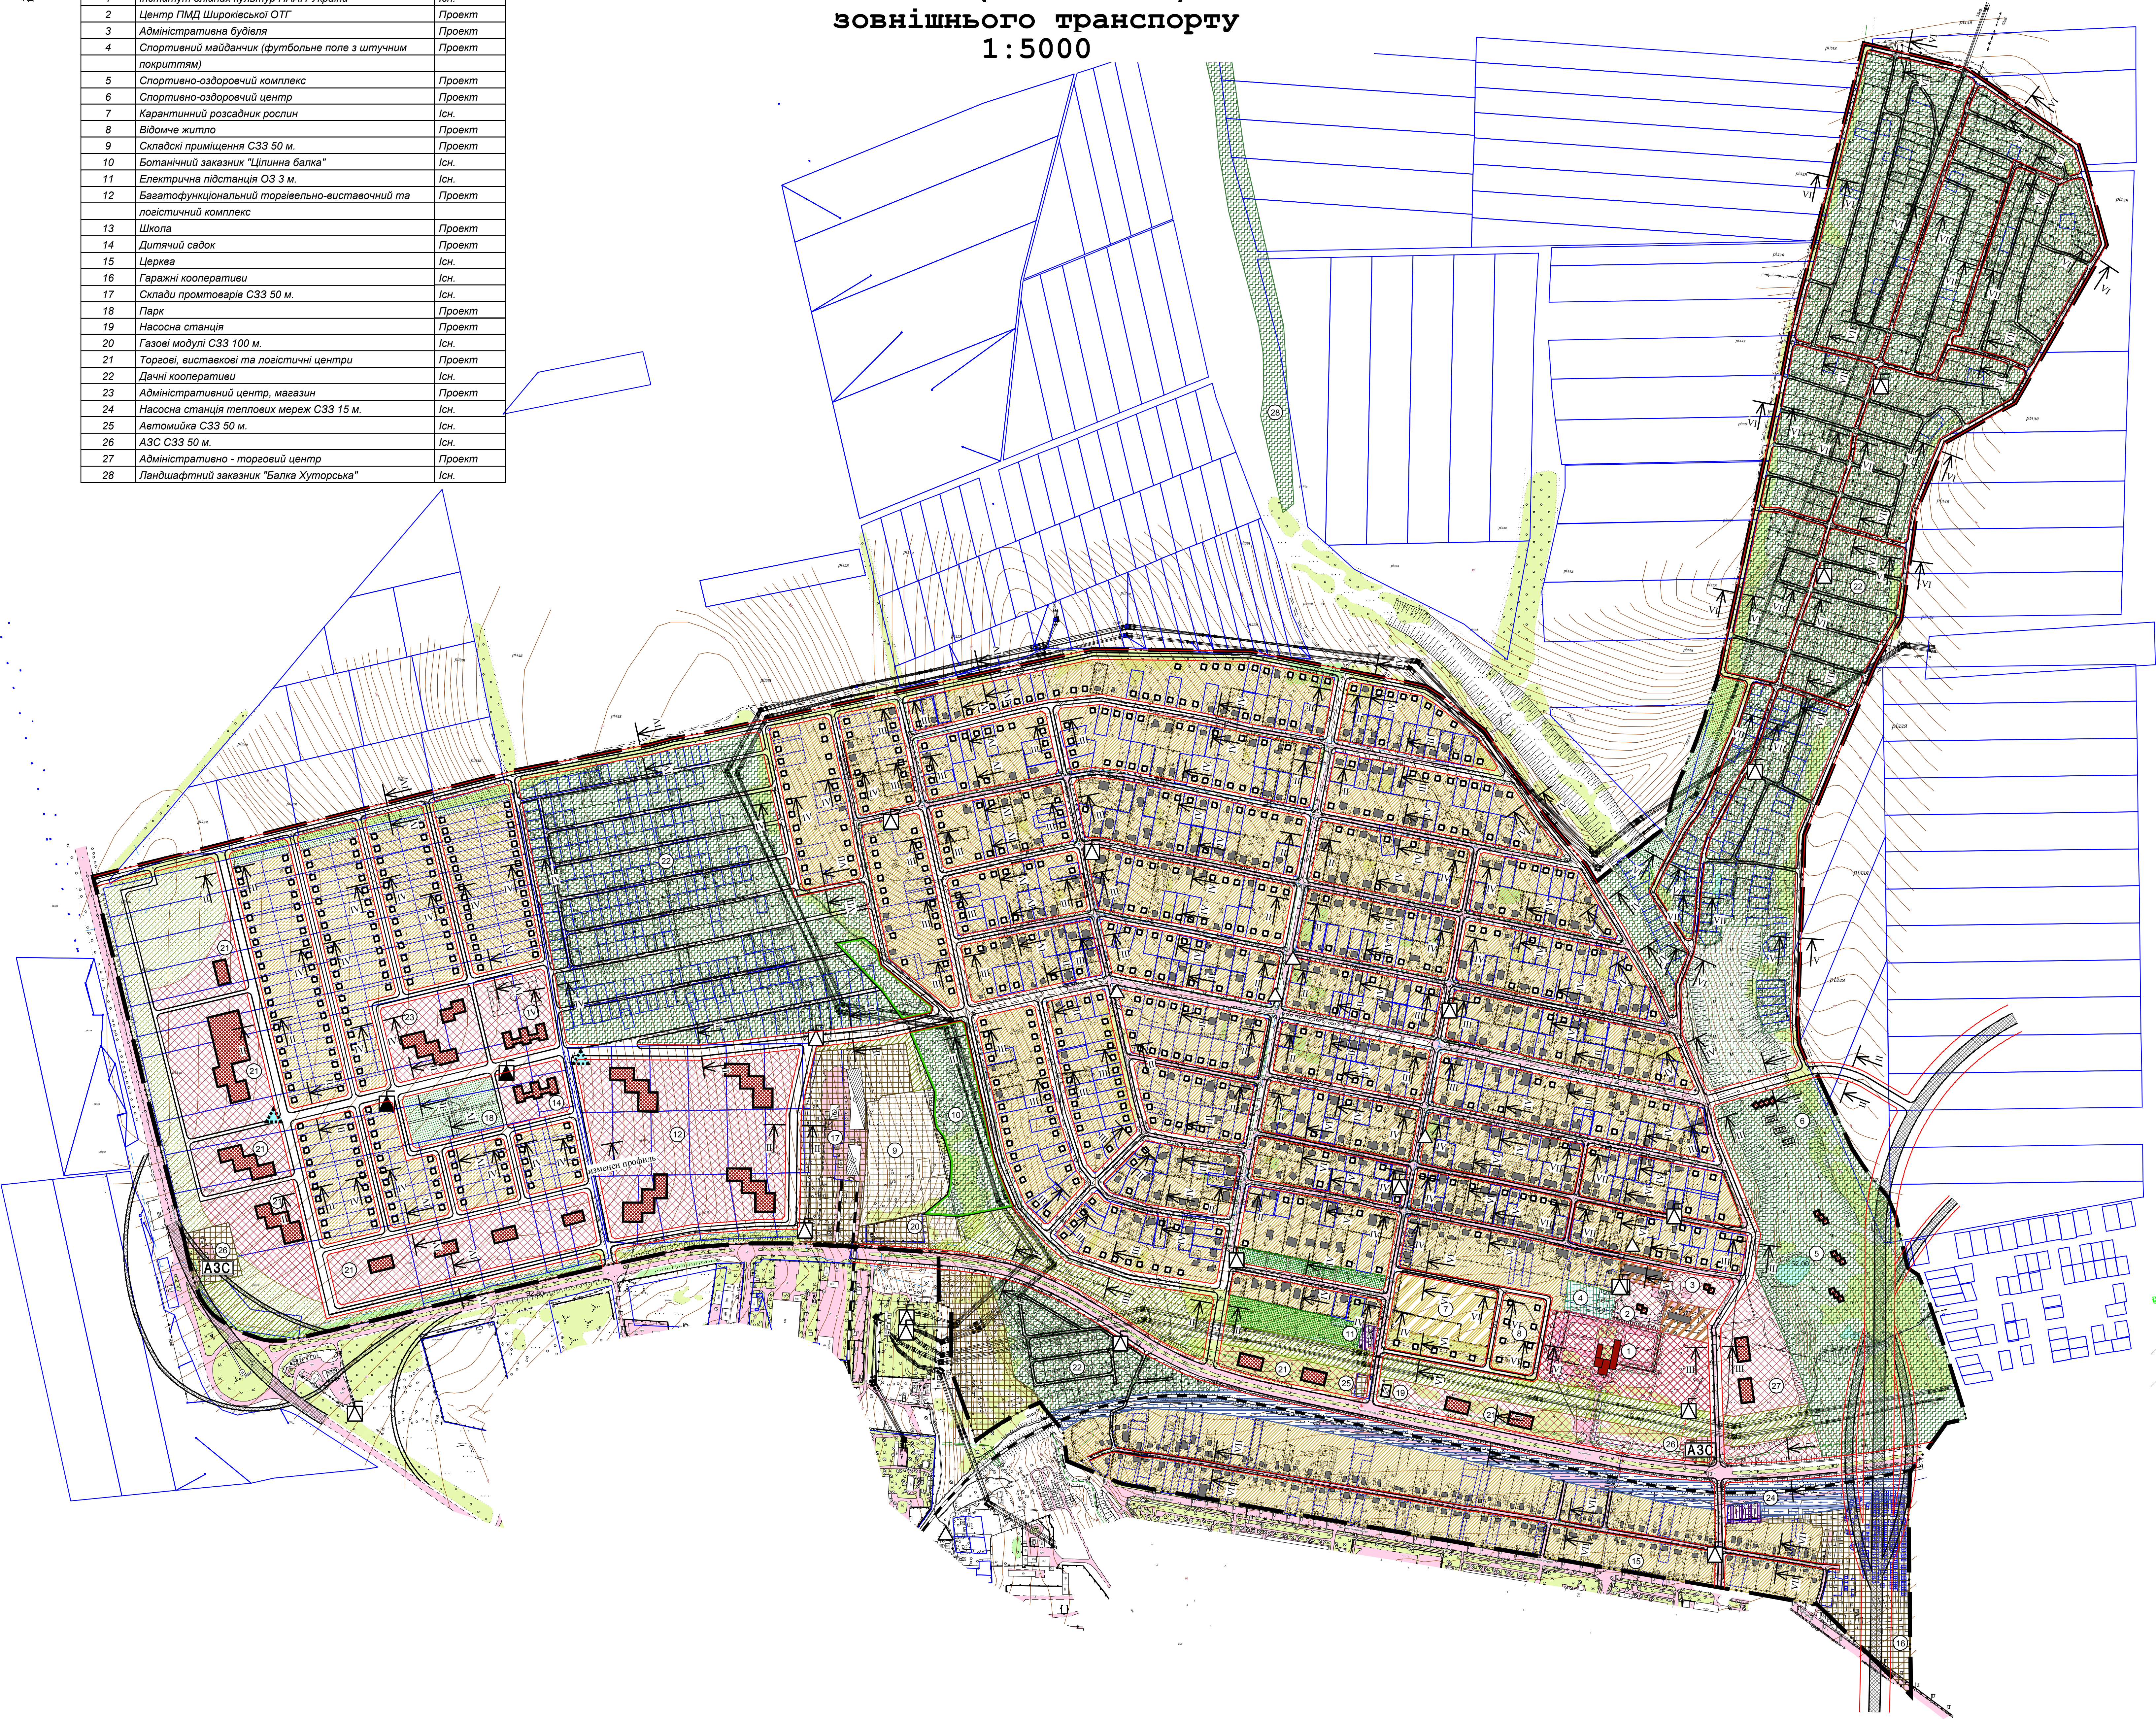

Умовні позначення

Існуючі	Проект	Найменування
—	—	Межа населеного пункту
□	□	Межі землекористування
□	□	Територія житлової садибної забудови
□	□	Територія сільськогосподарського призначення
□	□	Територія житлової багатоквартирної забудови
□	□	Територія громадської забудови
□	□	Територія транспортної інфраструктури
□	□	Територія інженерної інфраструктури
□	□	Територія комунальних об'єктів
□	□	Територія рекреаційного призначення
□	□	Територія оздоровчого призначення
□	□	Територія зелених насаджень загального користування
□	□	Територія зелених насаджень спеціального призначення
□	□	Межі території ПЗЗ місцевого значення
□	□	Житловий будинок
□	□	Виробнича будівля (споруда)
□	□	Громадська будівля
АЗС	АЗС	АЗС
—	—	Пролод
—	—	Червоні лінії
—	—	Залізниця
□	□	Комплексна трансформаторна підстанція (КТП)
□	□	Газорозподільний пункт (ГРП, ШРП)

Креслення поперечних профілів
вулиць
М 1:200

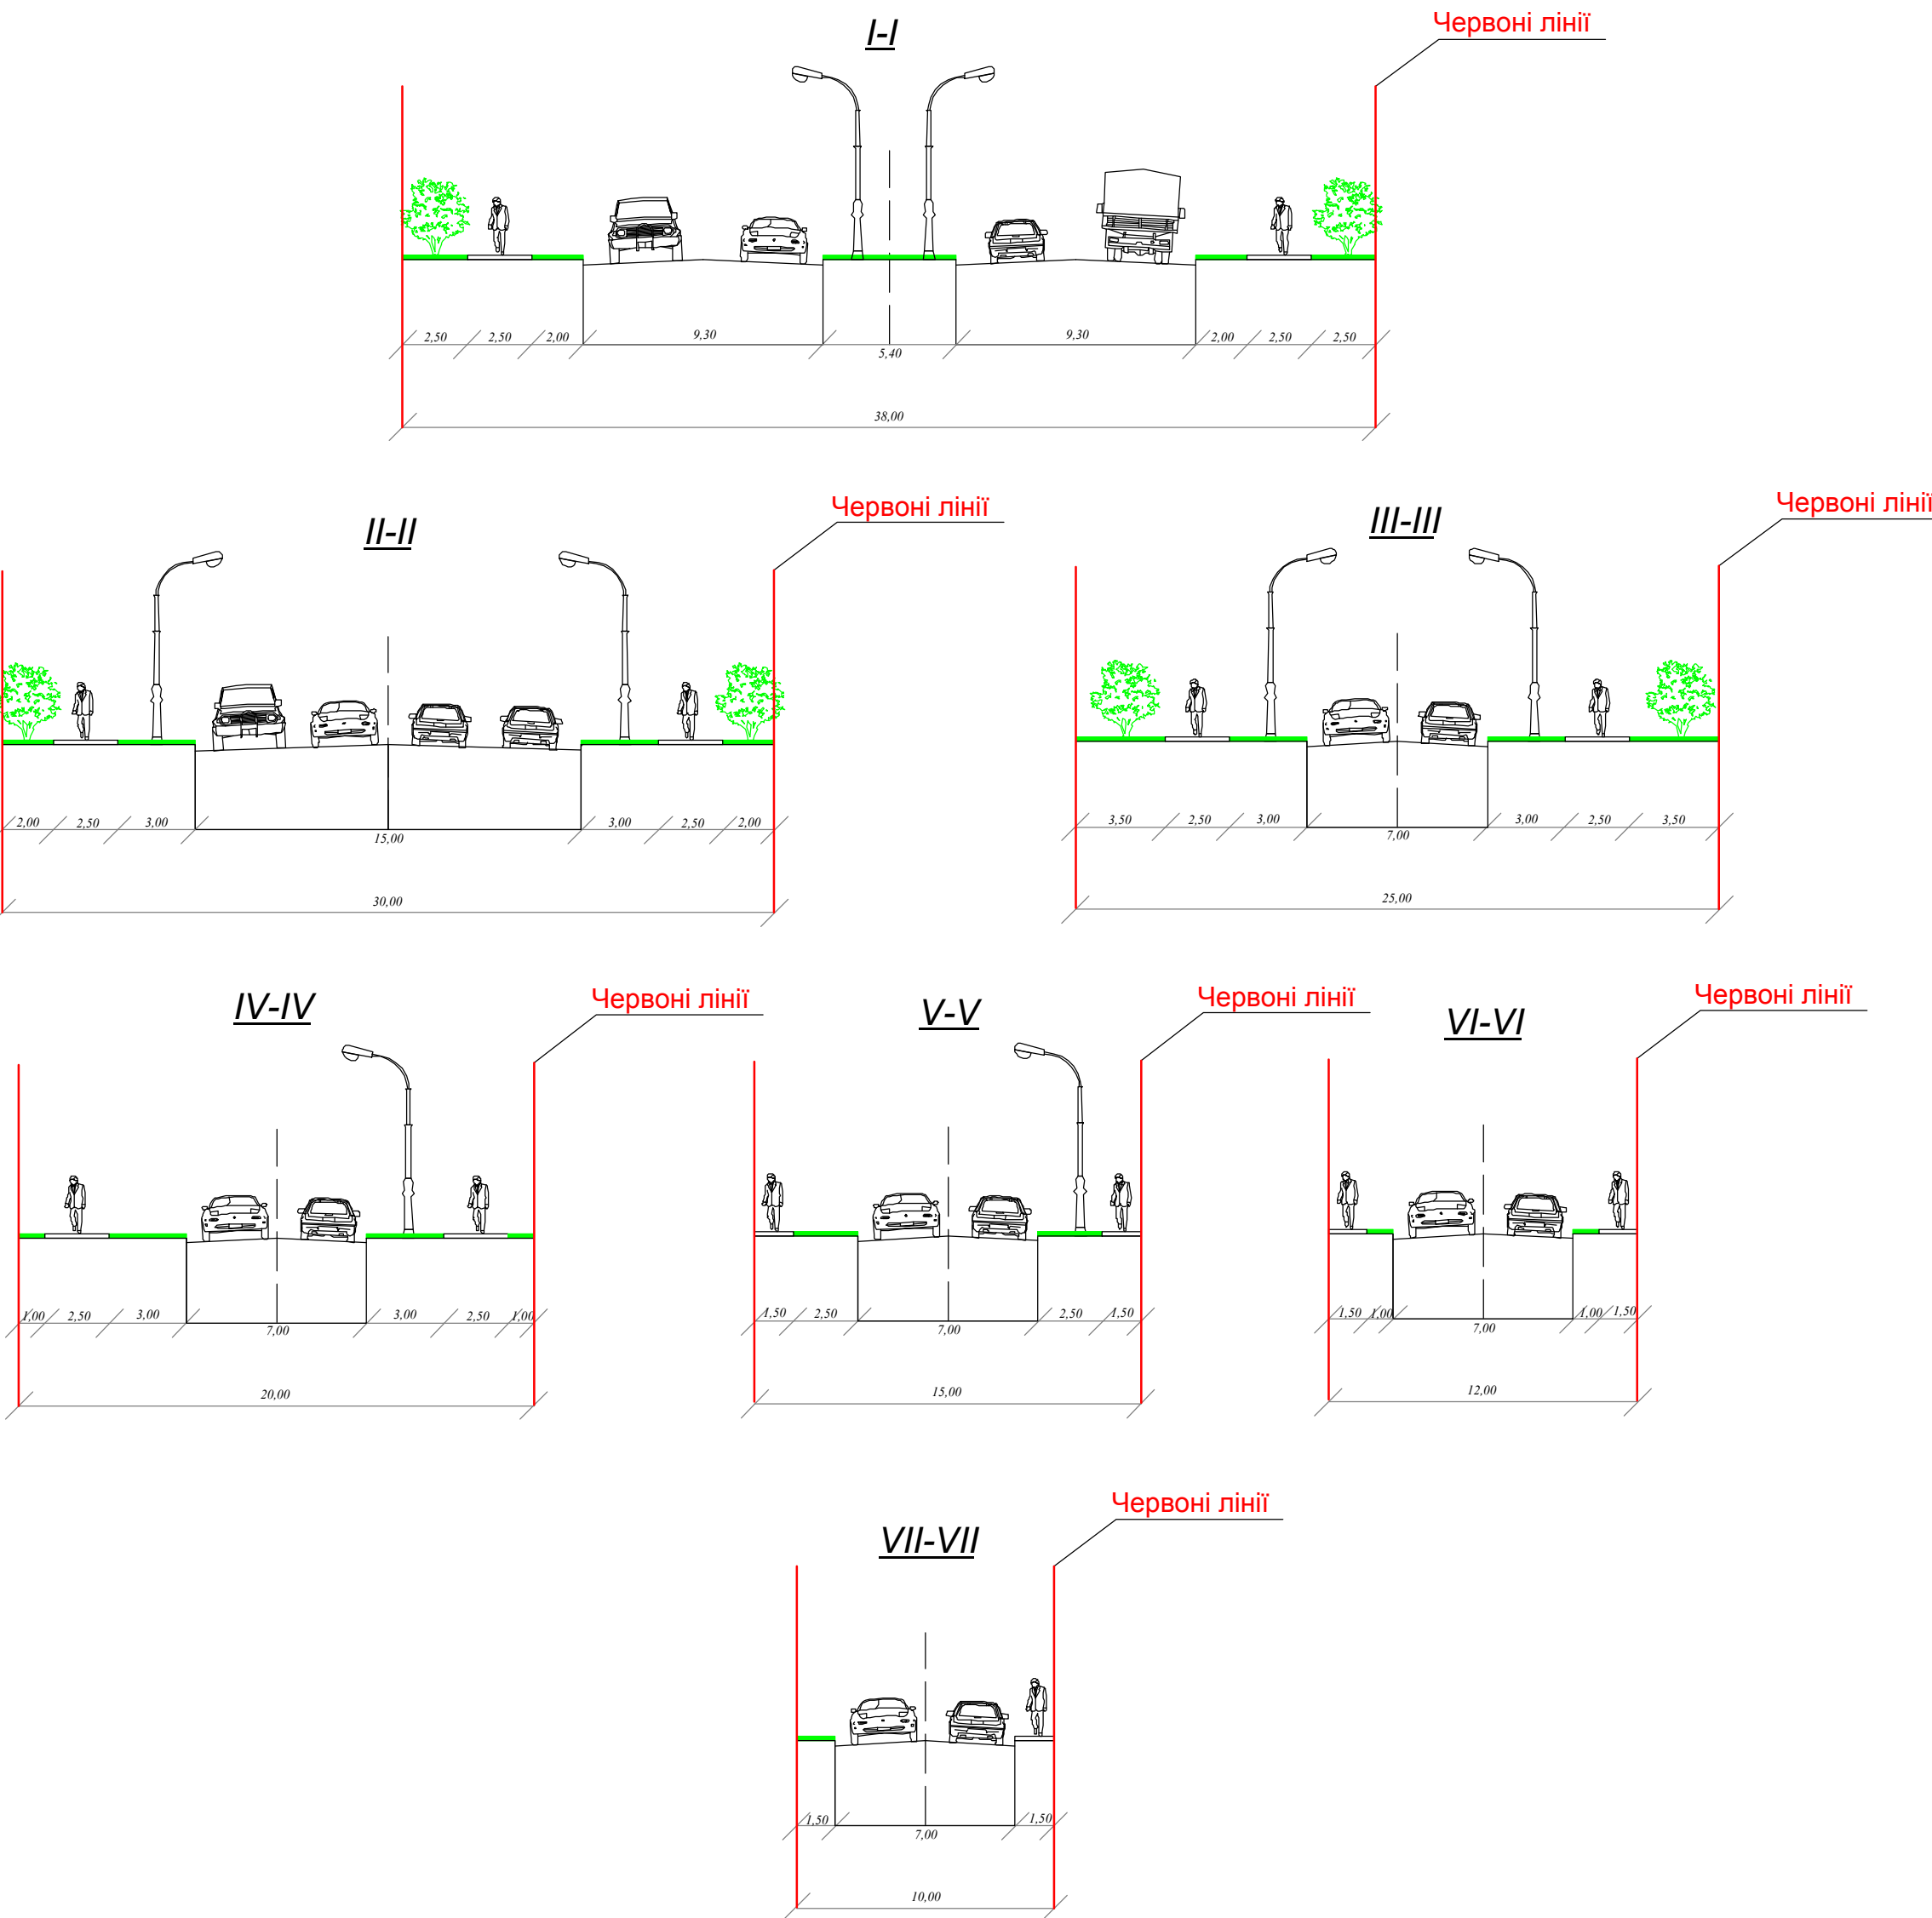

Змін	Кільк.	Арк.	№ док.	Підп.	Дата	Інформація про зміни	Статус	Архив	Архив
Г.А.П.	Продовж.					Додаток: Широцька сільська рада	ГП	6	9
Перевіряв	Продовж.					Схема вулично-дорожньої мережі, міського (сільського) та зовнішнього транспорту 1:5000			©ОП Прудов І.А.