


с. Петропавлівка
Широківської сільської ради Запорізького району

Генеральний план,
схема проектних планувальних обмежень
1:2000

Експлікація будівель та споруд		
№ п/п	Найменування	Примітка
1	Будівля магазину	Реконст.
2	Електрична підстанція	
3	Сонячна підстанція	
4	Адміністративна будівля	
5	Кладовище	
6	Територія зеленого туризму	
7	Спортивний майданчик	
8	Господарські будівлі	
9	Під'їзд пожежних машин до водозабору	

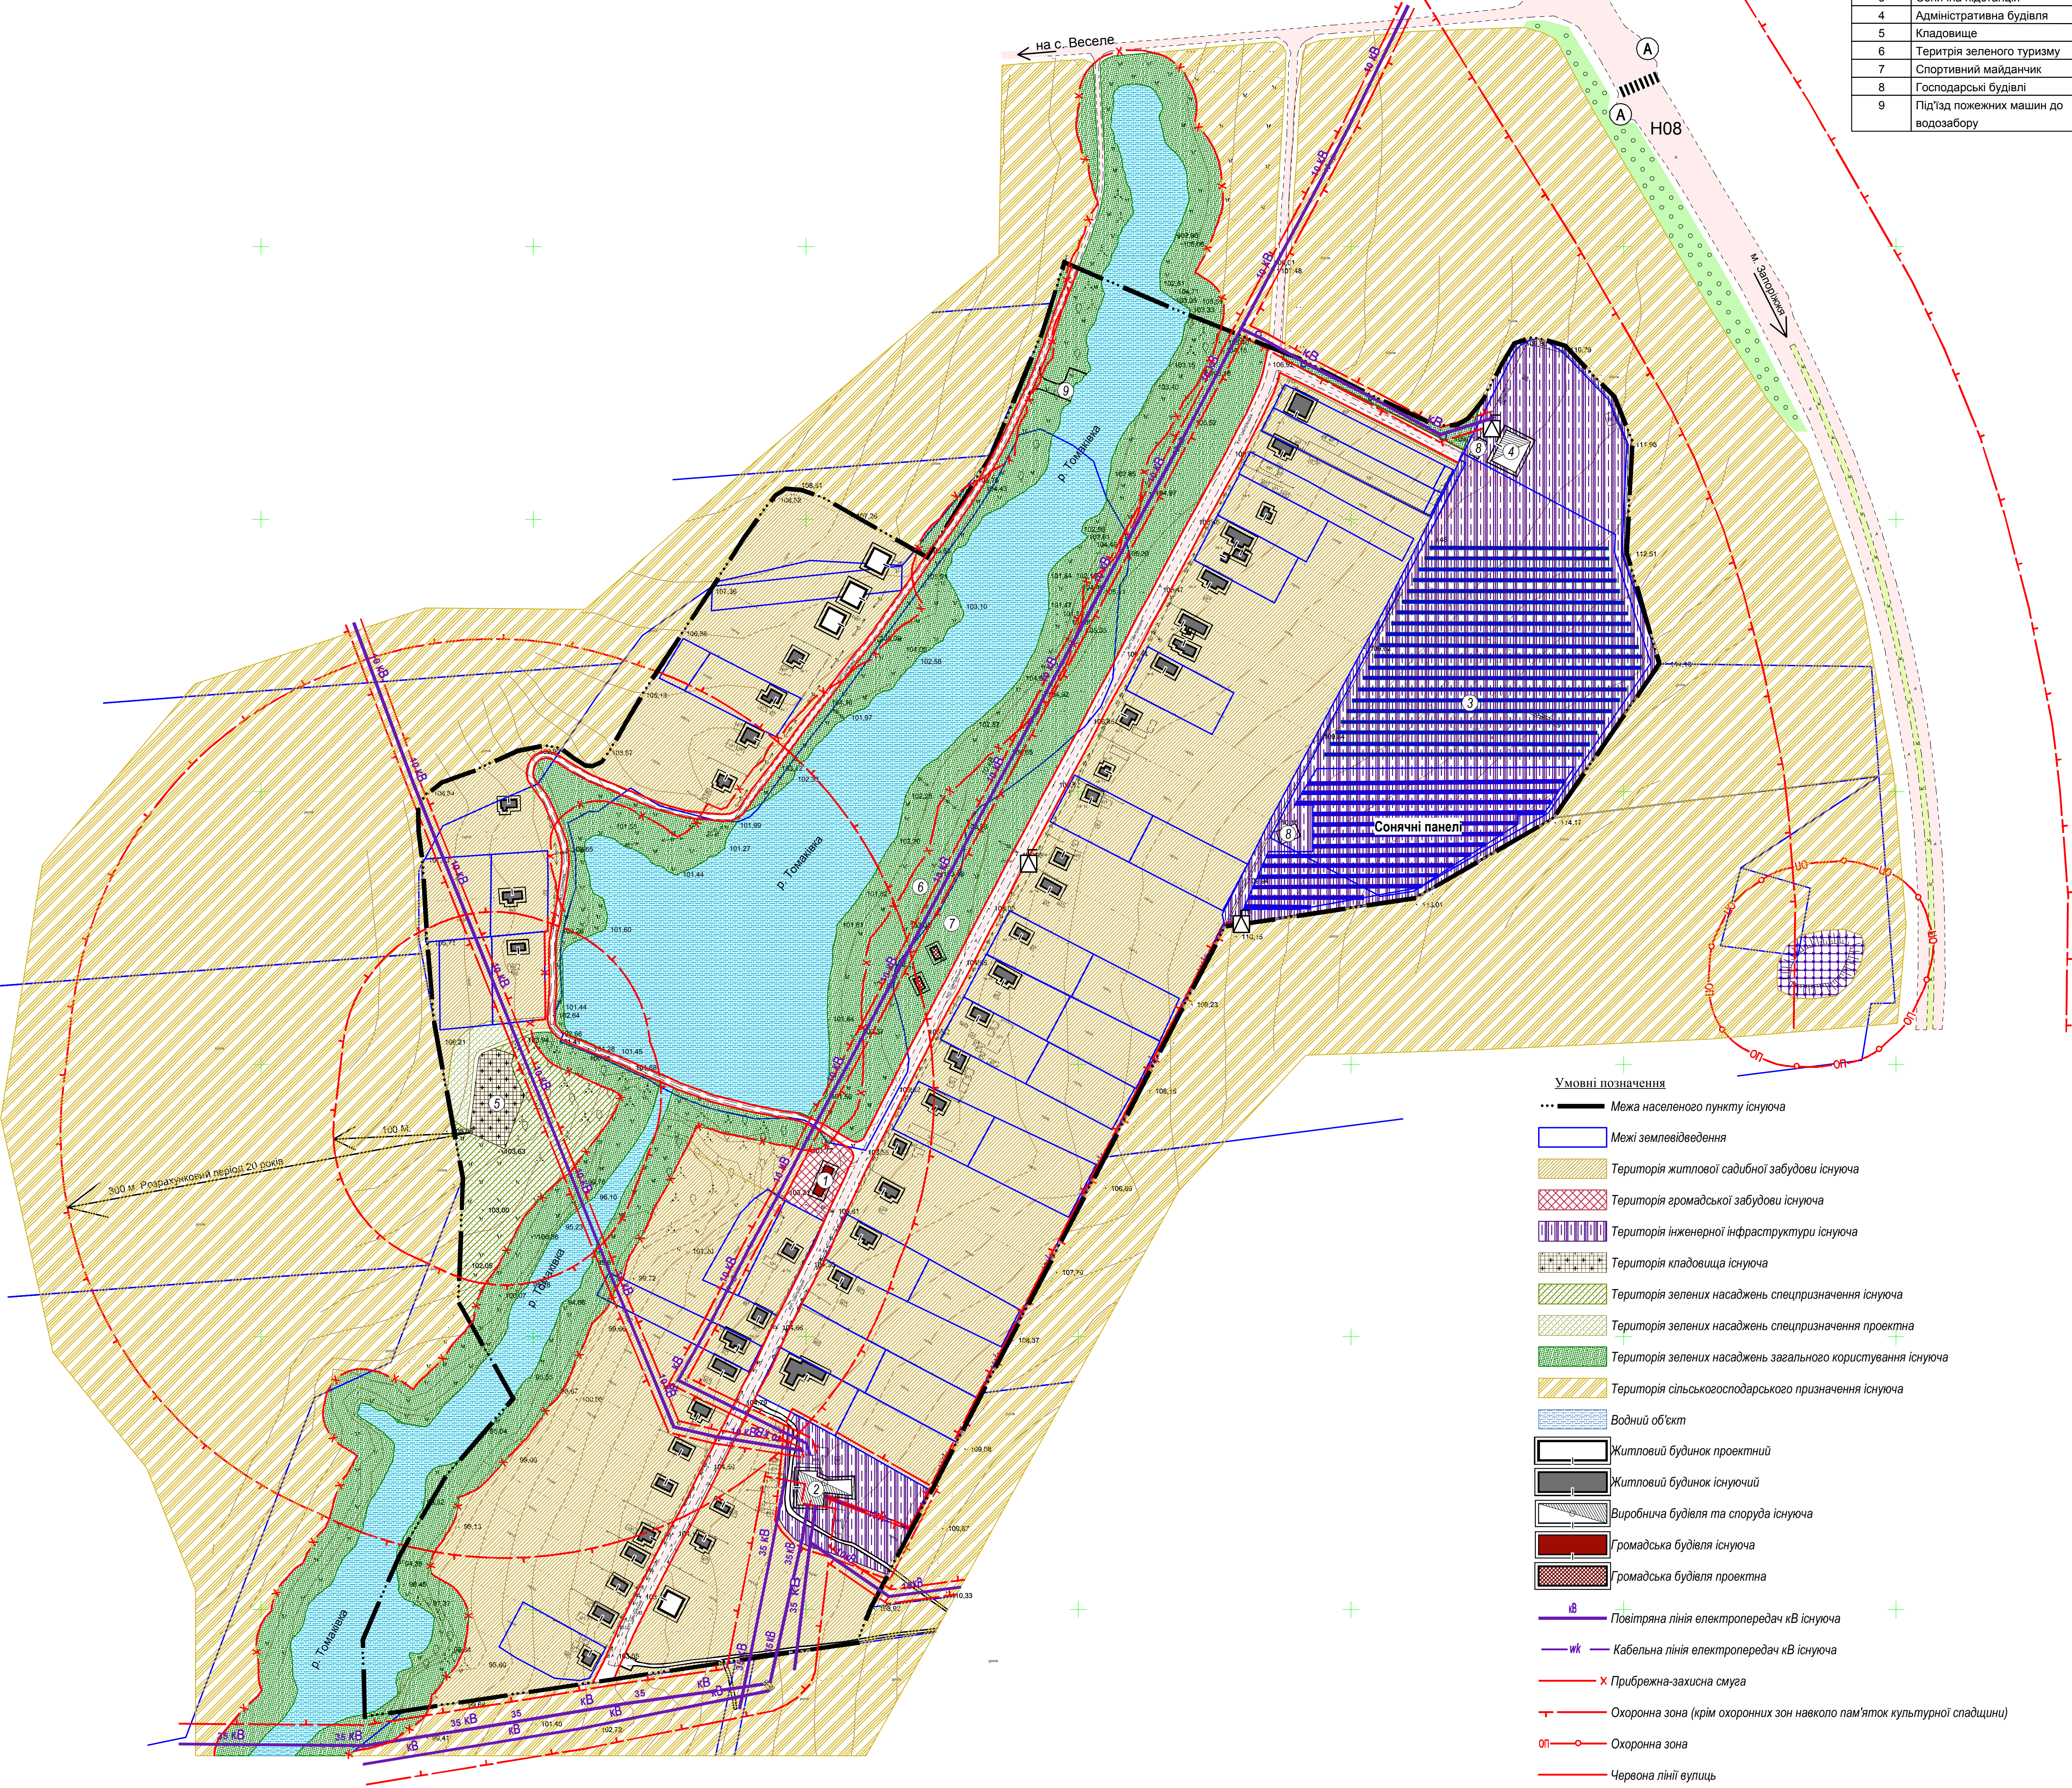

- Умовні позначення**
- Межа населеного пункту існуюча
 - Meжі землевідведення
 - Територія житлової садибної забудови існуюча
 - Територія громадської забудови існуюча
 - Територія інженерної інфраструктури існуюча
 - Територія кладовища існуюча
 - Територія зелених насаджень спецпризначення існуюча
 - Територія зелених насаджень спецпризначення проекту
 - Територія зелених насаджень загального користування існуюча
 - Територія сільськогосподарського призначення існуюча
 - Водний об'єкт
 - Житловий будинок проектний
 - Житловий будинок існуючий
 - Виробнича будівля та споруда існуюча
 - Громадська будівля існуюча
 - Громадська будівля проектна
 - кВ Повітряна лінія електропередач кВ існуюча
 - кВ Кабельна лінія електропередач кВ існуюча
 - Прибрежна-захисна смуга
 - Охоронна зона (крім охоронних зон навколо пам'яток культурної спадщини)
 - ОП Охоронна зона
 - Червона лінії вулиць
 - Сонячні панелі
 - Сонячні панелі проектні
 - Територія історико-культурного призначення
 - Наземний пішохідний перехід
 - А Автобусна зупинка
 - Комплектна трансформаторна підстанція (КТП) існуюча

Примітка:
Топографічною основою креслення слугували
планшети М 1:2000 виконані ФГО-П Іоанні В.В. 03.2017р.

						05.2017 ГП			
						Генеральний план, план зонування території села Петропавлівка Широківської сільської ради Запорізького району Запорізької області			
						Замовник: Широківська сільська рада Запорізького району Запорізької області		Стадія	Архив
						Генеральний план, схема проектних планувальних обмежень 1:2000		ГП	3
						ПІП "Стиль"		7	