


село Малишівка
Запорізького району, Запорізької області

Схема вулично - дорожньої мережі, міського (сільського)
та зовнішнього транспорту
М 1:2000

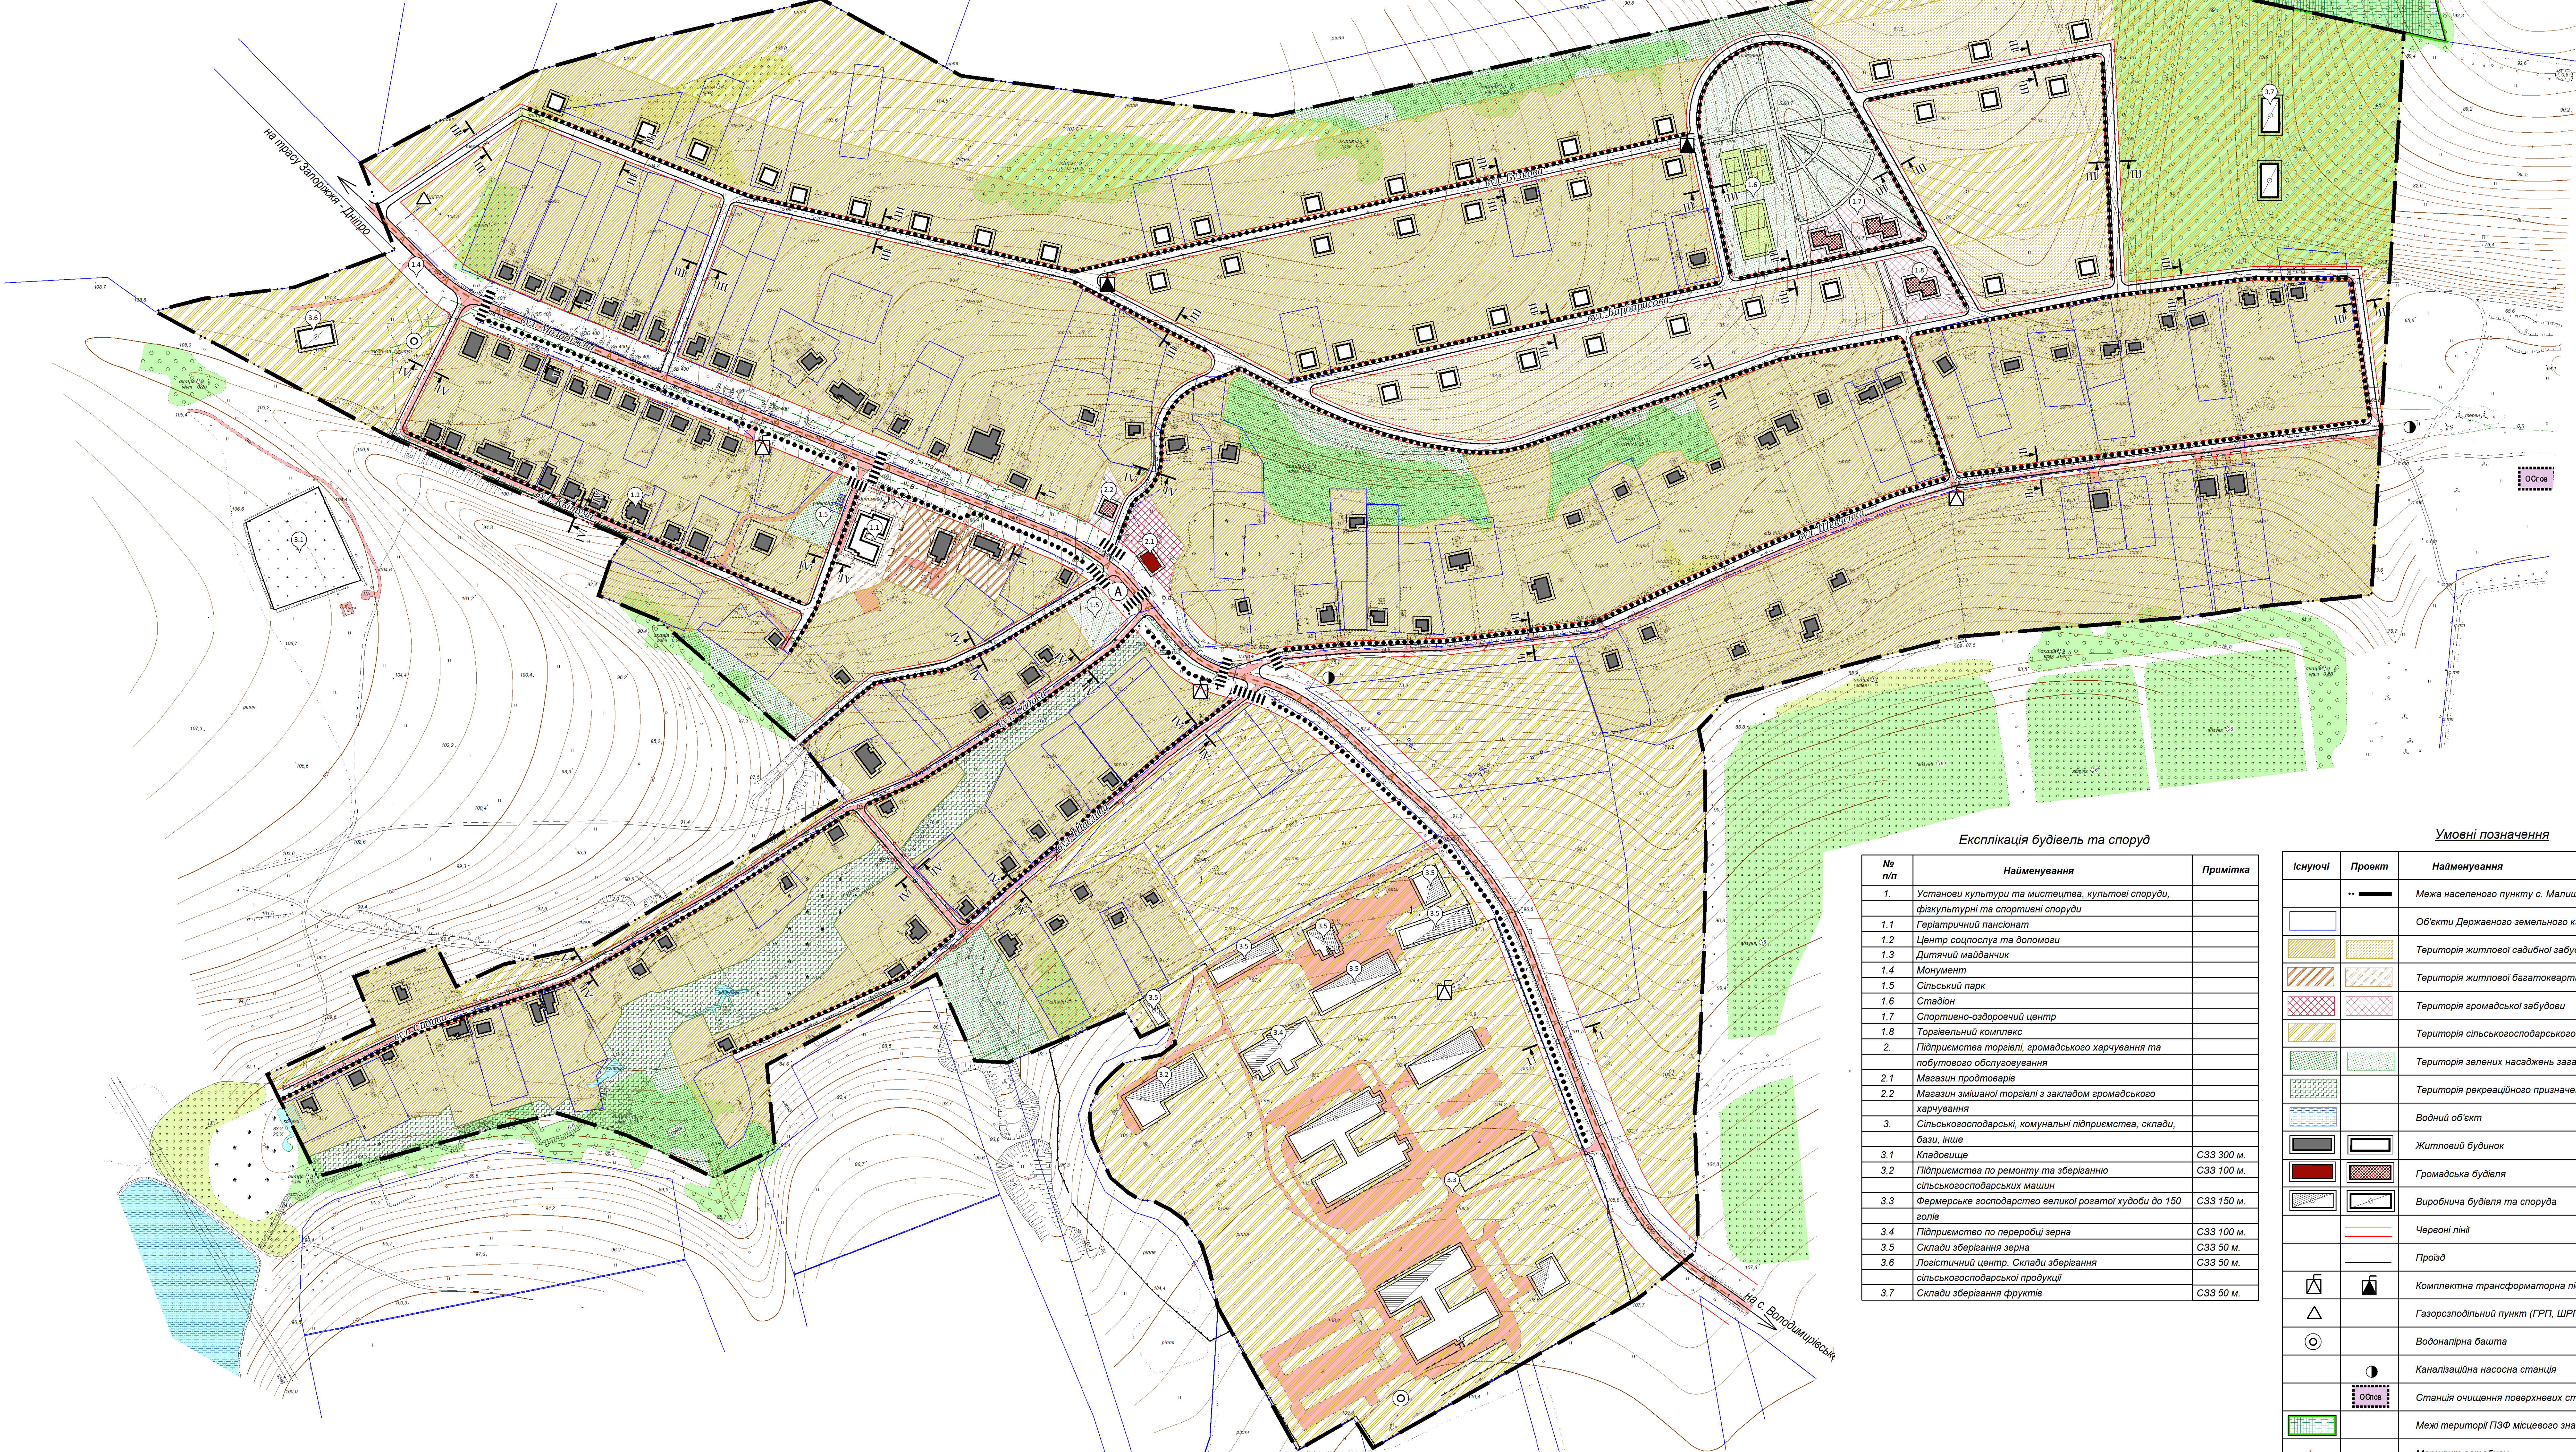


Експлікація будівель та споруд

№ п/п	Найменування	Примітка
1.	Установи культури та мистецтва, культові споруди, фігуранти та спортивні споруди	
1.1	Геріатричний пансіонат	
1.2	Центр соціальної та допомоги	
1.3	Дитячий майданчик	
1.4	Монумент	
1.5	Сільський парк	
1.6	Стадіон	
1.7	Спортивно-оздоровчий центр	
1.8	Торгівельний комплекс	
2.	Підприємства торгівлі, громадського харчування та побутового обслуговування	
2.1	Магазин продовольства	
2.2	Магазин змішаної торгівлі з закладом громадського харчування	
3.	Сільськогосподарські, комунальні підприємства, склади, бази, інші	
3.1	Кладовище	С33 300 м.
3.2	Підприємства по ремонту та зберіганню сільськогосподарських машин	С33 100 м.
3.3	Фермерське господарство великої рогатої худоби до 150 голів	С33 150 м.
3.4	Підприємство по переробці зерна	С33 100 м.
3.5	Склади зберігання зерна	С33 50 м.
3.6	Логістичний центр. Склади зберігання сільськогосподарської продукції	С33 50 м.
3.7	Склади зберігання фруктів	С33 50 м.

Умовні позначення

Існуючі	Проект	Найменування
		Межа населеного пункту с. Малишівка
		Об'єкти Державного земельного кадастру
		Територія житлової садибної забудови
		Територія житлової багатоквартирної забудови
		Територія громадської забудови
		Територія сільськогосподарського призначення
		Територія зелених насаджень загального користування
		Територія рекреаційного призначення
		Водний об'єкт
		Житловий будинок
		Громадська будівля
		Виробнича будівля та споруда
		Червоні лінії
		Провід
		Комплектна трансформаторна підстанція (КТП)
		Газорозподільний пункт (ГРП, ШРП)
		Водонапірна башта
		Каналізаційна насосна станція
		Станція очищення поверхневих стічних вод
		Межі території ПЗФ місцевого значення
		Маршрут автобусу
		Пішохідний перехід
		Шлях руху пішоходів
		Автобусна зупинка

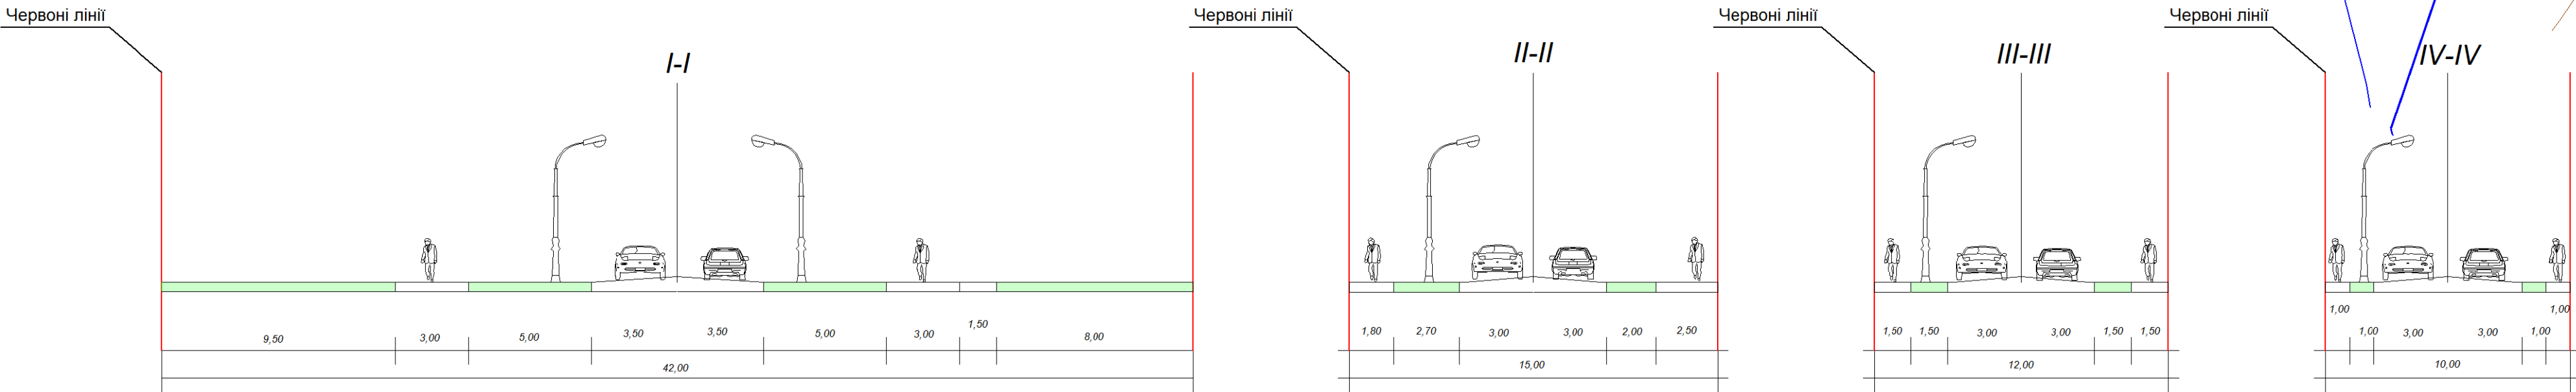

194/197П					
Генеральний план села Малишівка Запорізького району Запорізької області					
Оновлення з розширенням меж населеного пункту та план зонювання села Малишівка Запорізького району Запорізької області (у складі генерального плану)					
Зміст	Кільк.	Арк.	№рек.	Підп.	Датум
Завдання				Широкошасна сільська рада	Сторінка
ГАП				Прудка	4
Перевіряє				Прудка	7
Розробив				Прудка	7
Схема вулично - дорожньої мережі, міського (сільського) та зовнішнього транспорту М 1:2000					
Формат 1188 x 850					