*село Малишівка*
*Запорізького району, Запорізької області*

*Схема інженерного обладнання території*
*М 1:2000*

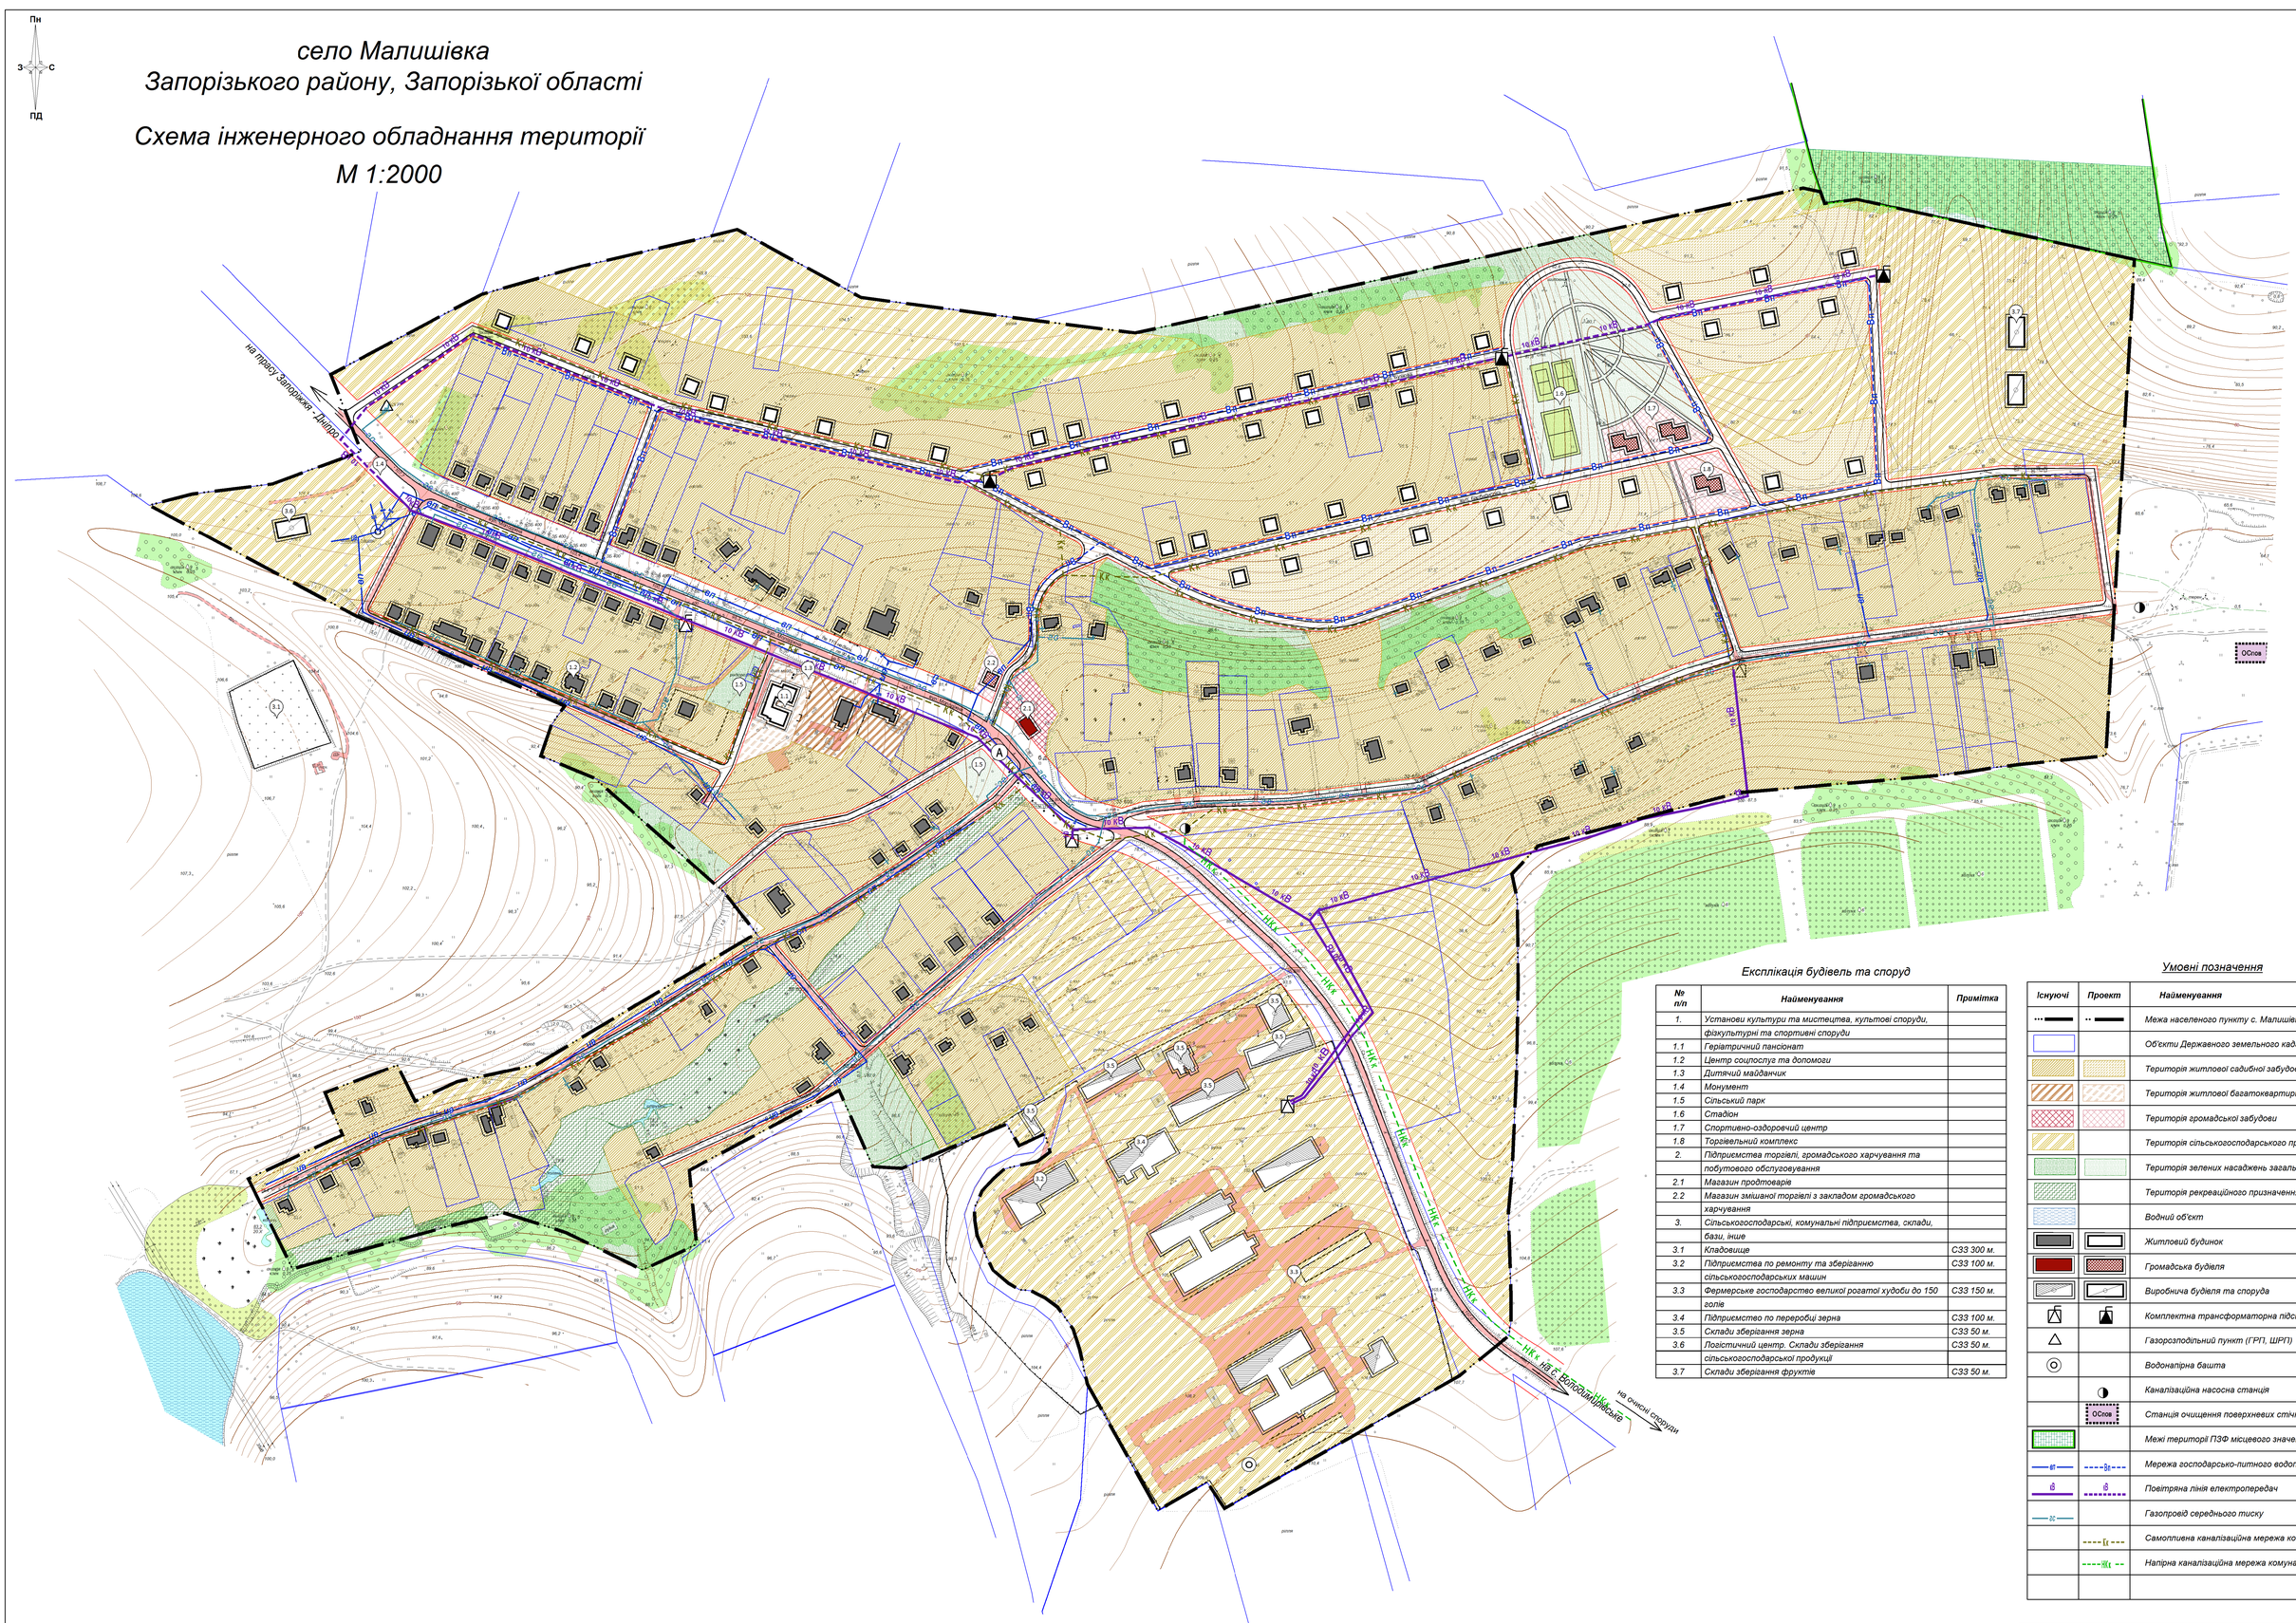


*Експлікація будівель та споруд*

| № п/п | Найменування | Примітка |
|---|---|---|
| 1. | Установи культури та мистецтва, культові споруди, | |
| | фізкультурні та спортивні споруди | |
| 1.1 | Геріатричний пансіонат | |
| 1.2 | Центр соцпослуг та допомоги | |
| 1.3 | Дитячий майданчик | |
| 1.4 | Монумент | |
| 1.5 | Сільський парк | |
| 1.6 | Стадіон | |
| 1.7 | Спортивно-оздоровчий центр | |
| 1.8 | Торгівельний комплекс | |
| 2. | Підприємства торгівлі, громадського харчування та | |
| | побутового обслуговування | |
| 2.1 | Магазин продтоварів | |
| 2.2 | Магазин змішаної торгівлі з закладом громадського | |
| | харчування | |
| 3. | Сільськогосподарські, комунальні підприємства, склади, | |
| | бази, інше | |
| 3.1 | Кладовище | СЗЗ 300 м. |
| 3.2 | Підприємства по ремонту та зберіганню | СЗЗ 100 м. |
| | сільськогосподарських машин | |
| 3.3 | Фермерське господарство великої рогатої худоби до 150 | СЗЗ 150 м. |
| | голів | |
| 3.4 | Підприємство по переробці зерна | СЗЗ 100 м. |
| 3.5 | Склади зберігання зерна | СЗЗ 50 м. |
| 3.6 | Логістичний центр. Склади зберігання | СЗЗ 50 м. |
| | сільськогосподарської продукції | |
| 3.7 | Склади зберігання фруктів | СЗЗ 50 м. |

*Умовні позначення*

| Існуючі | Проект | Найменування |
|---|---|---|
| | | *Межа населеного пункту с. Малишівка* |
| | | *Об'єкти Державного земельного кадастру* |
| | | *Територія житлової садибної забудови* |
| | | *Територія житлової багатоквартирної забудови* |
| | | *Територія громадської забудови* |
| | | *Територія сільськогосподарського призначення* |
| | | *Територія зелених насаджень загального користування* |
| | | *Територія рекреаційного призначення* |
| | | *Водний об'єкт* |
| | | *Житловий будинок* |
| | | *Громадська будівля* |
| | | *Виробнича будівля та споруда* |
| | | *Комплектна трансформаторна підстанція (КТП)* |
| | | *Газорозподільний пункт (ГРП, ШРП)* |
| | | *Водонапірна башта* |
| | | *Каналізаційна насосна станція* |
| | ОСпов | *Станція очищення поверхневих стічних вод* |
| | | *Межі територій ПЗФ місцевого значення* |
| | | *Мережа господарсько-питного водопроводу* |
| | | *Повітряна лінія електропередач* |
| | | *Газопровід середнього тиску* |
| | | *Самопливна каналізаційна мережа комунальної каналізації* |
| | | *Напірна каналізаційна мережа комунальної каналізації* |
| | | |

| Змін. | Кільк. | Арк. | №док. | Підп. | Дата | 194/19ГП | | |
|---|---|---|---|---|---|---|---|---|
| | | | | | | Генеральний план села Малишівка Запорізького району Запорізької області. Оновлення з розширенням меж населеного пункту та план зонування села Малишівка Запорізького району Запорізької області (у складі генерального плану) | | |
| | | | | | | Замовник: Широківська сільська рада | Стадія | Аркуш | Аркушів |
| | | | | | | | ГП | 5 | 7 |
| ГАП | | Прудка | | | | Схема інженерного обладнання території М 1:2000 | ФОП Прудка І.А | | |
| Перевірив | | | | | | | | | |
| Розробив | | Прудка | | | | | | | |

Формат 1188 х 850