ФО – П Прудка І. А.

69039 м. Запоріжжя, пров. Вантажний, буд. 13
email: 2136006@ ukr.net.

Замовник:

Широківська сільська рада Запорізького району

Запорізької області

Генеральний план села Лукашеве Запорізького району Запорізької області. Оновлення з розширенням меж населеного пункту та План зонування села Лукашеве Запорізького району Запорізької області (у складі Генерального плану)

Пояснювальна записка до плану зонування

Шифр: 14/07-2017-ПЗ

ТОМ 3

Фізична особа підприємець _____ І. А. Прудка

Головний архітектор проекту _____І. А. Прудка

2018 р.

Погоджено

Зам. Інв. №

Підпис і дата

Інв. № об.

Позначення	Найменування	Аркуш
14/07-2017-З	Зміст	
14/07-2017-СУ	Склад проекту	
14/07-2017-ПД	Підтвердження ГАП	
14/07-2017-ВУ	Відомості про учасників проектування	
14/07-2017-ПЗ	Пояснювальна записка	
	1. Передмова	
	2. Загальні положення. Основні терміни, зміст та призначення зонінгу	
	3. Принципи зонування території населеного пункту	
	4. Перелік територіальних зон, що визначаються на схемі зонування, та обґрунтування їх меж	
	5. Містобудівні регламенти як сукупність обов'язкових вимог до використання земельних ділянок та об'єктів нерухомості, що встановлюються у межах відповідних територіальних зон	
	6. Перелік дозволених видів забудови та іншого використання земельних ділянок у межах різних територіальних зон	
	- Громадські зони	
	- Житлові зони	
	- Ландшафтно – рекреаційні зони	
	- Зони транспортної інфраструктури	
	- Зони інженерної інфраструктури	
	- Комунально – складські зони	
	- Виробничі зони	
	- Зони земель сільськогосподарського призначення	
	- Спеціальні зони	
	- Інші зони	
	7. Режими використання території, пов'язані з дією обмежень, що розповсюджуються на територію населеного пункту	
	8. Додатки	

Зам. Інв. №

Підпис і дата

Інв. №

Зм.	Кільк	Арк.	№	Підпис	Дат	14/07-2017-З			
Розробив		Прудкая			12.18	Зміст	Стадія	Аркуш	Аркуші
Перевірив							РП	1	1
ГАП		Прудкая			12.18		ФО-П Прудка І. А.		

№ тому	Позначення	Найменування	Примітки
		Текстові матеріали	
1.	14/07-2017-ПЗ	Пояснювальна записка до генерального плану	
2.	14/07-2017-ПЗ	Основні положення генерального плану	
3.	14/07-2017-ПЗ	Пояснювальна записка до плану зонування території	
4.		Графічні матеріали	
	Лист 1	Схема розташування населеного пункту в системі розселення М 1:50000	
	Лист 2	План існуючого використання території. Схема існуючих планувальних обмежень М 1:5000	
	Лист 3	Генеральний план (основне креслення). Схема планувальних обмежень М 1:5000	
	Лист 4	Схема вулично – дорожньої мережі, міського (сільського) та зовнішнього транспорту М 1:5000	
	Лист 5	Схема інженерного обладнання території М 1:5000	
	Лист 6	Схема інженерної підготовки та захисту території М 1:5000	
	Лист7	Схема зонування населеного пункту М1:5000	
		Інженерно-технічні заходи цивільного захисту (цивільної оборони)	У вигляді окремих томів

Зам. Інв. №

Підпис і дата

Інв. №

Зм.	Кіл.	Арк.	№	Підпис	Дат	14/07-2017-СП			
Розробив		Прудка			12.18	Склад проекту	Стадія	Аркуш	Аркуші
Перевірив							РП	1	1
ГАП		Прудка			12.18		ФО-П Прудка І. А.		

Генеральний план, план зонування території села Лукашеве Широківської сільської ради Запорізького району Запорізької області. Оновлення з розширенням меж населеного пункту та план зонування села Лукашеве Запорізького району Запорізької області (у складі генерального плану) виконано згідно з вимогами ДБН Б.1.1-15:2012 "Склад та зміст генерального плану населеного пункту", ДБН Б.1.1-22:2017 «Склад та зміст плану зонування території», ДБН Б. 2.2-12:2018 «Планування і забудова територій», екологічних, санітарно-гігієнічних та протипожежних норм, що діють на території України, а також Закону України «Про містобудівну діяльність».

Головний архітектор проекту І. А. Прудка

Кваліфікаційний сертифікат відповідального виконавця окремих видів робіт (послуг), пов'язаних із створенням об'єкта архітектури (розроблення містобудівної документації) Серія АА №003280

						14/07-2017-ПД			
Зм.	Кільк	Арк.	№	Підпис	Дат		Стадія	Аркуш	Аркуші
Розробив		Прудка			12.18	Підтвердження ГАПа (ГІПа)	РП	1	1
Перевірив							ФО-П Прудка І. А.		
ГАП		Прудка			12.18				

Зам. Інв. №

Підпис і дата

Інв. №

Розділ проекту	Посада	Ініціали, прізвище	Підпис
ПЗ	Головний архітектор проекту	І. А. Прудка	
ГП	Головний архітектор проекту	І. А. Прудка	

Зам. Інв. №

Підпис і дата

Інв. №

Зм.	Кіл.	Арк.	№	Підпис	Дат	14/07-2017-ВУ			
Розробив		Прудка			12.18	Відомість про учасників проектування	Стадія	Аркуш	Аркуші
Перевірив							РП	1	1
ГАП		Прудка			12.18		ФО-П Прудка І. А.		

1. Передмова.

Замовником Генерального плану є Широківська сільська рада Запорізького району Запорізької області.

Виконавцем Генерального плану та плану зонування є:
Фізична особа підприємець Прудка І. А.
69039, м. Запоріжжя, пров. Вантажний, 13.
ІНН 2803210762.

Головний архітектор проекту – І. А. Прудка, кваліфікаційний сертифікат Серія АА № 003280 (розроблення містобудівної документації).

У складі авторського колективу – М. С. Прудкий

Рішення прийняті в зонінгу населеного пункту з урахуванням чинного законодавства України у сфері містобудування та вимог державних будівельних норм, а саме:
Земельного кодексу України;
Водного кодексу України;
Закону України «Про регулювання містобудівної діяльності»
Закону України «Про основи містобудування»
Закону України «Про благоустрій населених пунктів»
ДБН Б.1.1-22:2017 «Склад та зміст плану зонування території»
Наказу «Про затвердження порядку надання містобудівних умов та обмежень забудови земельної ділянки, їх склад та зміст»
ДБН Б.2.2-12:2018 «Планування і забудова територій»;
Профільних ДБН за типом об'єкту;
ДСП «Державні санітарні правила планування та забудова населених пунктів» від 19.06.96 р. № 173;
профільних СанПін за типом об'єкту.

2. Загальні положення.
Основні терміни, зміст та призначення зонінгу

У цій роботі вживаються терміни, встановлені законами України «Про основи містобудування», Закон України «Про регулювання містобудівної діяльності», Закон України «Про охорону культурної спадщини», Закон України «Про охорону навколишнього середовища», Земельним Кодексом України та державними будівельними нормами ДБН Б.2.2-12:2018 «Планування і забудова територій»;

Нижче наведені використані терміни та визначення понять

Зонінг – містобудівна документація, що визначає умови та обмеження використання території для містобудівних потреб у межах визначених зон.

Зонування – встановлення територіальних зон в межах населеного пункту з визначенням відповідних видів використання території, об'єктів нерухомості та встановленням містобудівного регламенту.

Містобудівний регламент – сукупність обов'язкових вимог до використання земельних ділянок, що встановлюється у межах відповідних територіальних зон і визначає дозволені види використання території земельних ділянок, граничні (мінімальні і (або) максимальні) розміри земельних ділянок, граничні параметри дозволеного будівництва та реконструкції об'єктів нерухомості, обмеження використання земельних ділянок і об'єктів нерухомості, що встановлюються відповідно до законодавства України. Містобудівний регламент використовуються в процесі проектування, забудови та наступної експлуатації об'єктів.

Вид використання території – забудова та інше використання території, що поєднуються за подібністю відповідних ознак. Розрізняються переважні (безумовно дозволені) та супутні (допоміжні), які є дозволенними за наявністю переважних видів використання.

Переважний вид використання території – вид використання, який відповідає переліку дозволених видів для даної територіальної зони.

Дозволений (переважний та супутній) вид використання території – використання, яке відповідає переліку переважних та супутніх видів використання для відповідної зони, встановленої в зонінгу відповідно до містобудівної документації.

Супутній вид використання території (земельної ділянки) – вид використання, який є дозволенним та необхідним для забезпечення функціонування переважного виду використання земельної ділянки.

Коефіцієнт забудови – відношення сумарної поверхової (загальної) площі будинків та споруд до площі земельної ділянки. Встановлюється для житлової та громадської забудови.

Коефіцієнт озеленення – співвідношення площі земельної ділянки, що може бути забудована, до всієї площі земельної ділянки.

Максимальний відсоток забудови у межах земельної ділянки – відношення сумарної площі земельної ділянки, що може бути забудована, до всієї площі земельної ділянки.

Максимально допустима щільність населення (для нової багатоквартирної житлової забудови), люд/га – відношення кількості осіб, що можуть проживати на ділянці перспективної забудови, до площі ділянки за умови розташування на ділянці зелених насаджень, майданчиків, місць паркування автомобілів, інженерного обладнання, проходів та проїздів відповідно до державних будівельних норм.

Мінімальна площа земельної ділянки для розміщення об'єкта допускається не менша ніж сума площі, зайнятої існуючим чи запроектованим об'єктом будівництва, площі необхідних озеленених територій, площі для паркування автомобілів, проїздів та інших необхідних допоміжних об'єктів, призначених для обслуговування і експлуатації об'єкта згідно з зонінгом.

Територіальна зона – територія (у визначених межах) на схемі зонування, стосовно якої встановлені єдині зональні вимоги.

Територіальна підзона – частина зони, в межах якої умови та обмеження забудови земельних ділянок, відрізняються від аналогічних показників територіальної зони окремими показниками, що пов'язані з відповідними планувальними обмеженнями.

Охоронна зона – зона, в якій встановлюється спеціальний режим охорони об'єктів, які в ній розміщені.

Санітарно - захисна зона – територія навколо потенційно небезпечного підприємства, в межах якої заборонено проживання населення та ведення господарської діяльності, розміри якої встановлюються проектною документацією відповідно до державних нормативних документів.

Червоні лінії – визначені в містобудівній документації відносно пунктів геодезичної мережі лінії, які відмежовують елементи транспортної інфраструктури (вулиці, проїзди, площі) від елементів планувальної структури (кварталів, мікрорайонів та ін.).

Блакитні лінії – лінія обмеження висоти та силуету забудови, спрямована на регулювання естетичних та історіко – містобудівних якостей забудови.

Зелені лінії – обмеження щодо розміщення об'єктів у межах усіх озеленених територій загального користування, рекреаційних лісів і лісопарків (існуючих та тих, що резервуються), об'єктів природно – заповідного фонду, зон охоронювального ландшафту.

Зонінг населеного пункту створюється з метою:

- регулювання планування та забудови територій з урахуванням державних, громадських та приватних інтересів;
- раціонального використання території населеного пункту;
- забезпечення умов для реалізації планів і програм сталого розвитку населених пунктів, збереження природного середовища та охорони культурної спадщини
- встановлення правових гарантій з використання і будівельної зміни нерухомості для власників і осіб, що мають намір придбати права володіння, користування і розпорядження земельними ділянками, іншими об'єктами нерухомості;
- створення сприятливих умов для залучення інвестицій у будівництво шляхом забезпечення можливості вибору інвестором найбільш ефективного виду використання земельної ділянки для містобудівних потреб у відповідності з містобудівними регламентами;
- забезпечення вільного доступу громадян до інформації стосовно розвитку населеного пункту, взаємоузгодження державних інтересів, громади та інвесторів;
- забезпечення сумісності забудови окремих земельних ділянок з оточуючою забудовою та землекористуванням;
- сприяння реалізації завдань довгострокового розвитку міста, іншого населеного пункту з урахуванням його містобудівних особливостей, наявності об'єктів культурної спадщини, природно-заповідного фонду, соціального, економічного та екологічного стану.
- Основною задачею зонінгу є визначення меж зон (підзон) однорідних видів та умов використання на території населеного пункту і встановлення, диференційовано по зонах (підзонах), містобудівних регламентів.

3. Принципи зонування території населеного пункту.

Планом зонування (зонінгом) на території населеного пункту визначаються межі зон (підзон) з однорідними видами та умовами використання та встановлюються містобудівні регламенти, що діють у межах цих зон (підзон).

Зонінг розроблявся на основі генерального плану населеного пункту.

Зонінг не визначає розміщення конкретних об'єктів та обсяги будівництва, а встановлює види використання території ділянок, умови та обмеження в межах визначених зон та підзон.

При розробленні населеного пункту схема зонування території виконувалась у межах структурно-планувальних елементів – планувальних зон та планувальних утворень (житлові, промислові, рекреаційні райони, мікрорайони, квартали и т.д.), обмежених магістральними вулицями або природними межами.

Основною складовою зонінгу є схема зонування, яка розробляється в цифровій векторній формі в державній системі координат УСК 2000.

На схемі зонування територія населеного пункту у відповідності з функціональним призначенням поділяється на територіальні зони, для кожної з яких встановлюється містобудівний регламент.

На схемі зонування відображаються: межі та кодові позначення встановлених зонінгом територіальних зон та підзон.

Кодові позначення зон та підзон групуються за видами. Кодова позначка підзони включає код територіальної зони, в межах якої вона виділена, і цифровий додаток, що встановлюється в залежності від виду планувальних обмежень, які розповсюджуються на територію підзони.

Сукупність видів використання та граничних параметрів нового будівництва та реконструкції об'єктів нерухомості у складі містобудівного регламенту є єдиною для усіх об'єктів у межах відповідної зони (підзони), якщо інше не обумовлене у складі регламенту.

Містобудівні регламенти підзон можуть відрізнятися від містобудівного регламенту територіальних зон тільки за окремими показниками дозволеного будівництва, обумовленими дією планувальних обмежень.

Для територіальної підзони окремо не встановлюються додаткові переліки переважних, супутніх та допустимих видів забудови та іншого використання території земельних ділянок.

Для окремої земельної ділянки дозволеним є таке використання, яке відповідає містобудівному регламенту зони (підзони), на території якої ділянка знаходиться.

Невідповідність наміру забудови встановленим видам дозволеного використання земельних ділянок і об'єктів, зазначеним у містобудівному регламенті, означає, що його застосування у відповідній територіальній зоні не допускається.

Суттєва зміна параметрів існуючих земельних ділянок і об'єктів нерухомості, види використання і граничні параметри яких не відповідають містобудівному регламенту, можлива лише шляхом приведення таких об'єктів у відповідність з містобудівним регламентом або шляхом зменшення їх невідповідності.

Розташування в межах земельних ділянок супутніх видів забудови інженерно-технічних об'єктів, споруд, комунікацій, що забезпечують реалізацію дозволеного використання об'єктів нерухомості на цих ділянках, можливе за умов обов'язкового дотримання технічних умов (норм).

Земельні ділянки та розташовані на них об'єкти, які існували до впровадження в дію зонінгу, граничні параметри яких не відповідають містобудівному регламенту, можуть використовуватись без визначення терміну їх приведення у відповідність з містобудівним регламентом, якщо вони не створюють загрози для життя, здоров'я людей, для навколишнього середовища, об'єктів культурної спадщини та природно-заповідного фонду.

Зміна видів використання земельних ділянок і об'єктів нерухомості фізичними та юридичними особами здійснюється у відповідності з переліком переважних, супутніх видів забудови в межах відповідної територіальної зони за дотримання інших вимог містобудівних регламентів та в порядку, визначеному законодавством.

4. Перелік територіальних зон, що визначаються на схемі зонування, та обґрунтування їх меж.

На основі аналізу існуючої забудови населеного пункту, перспективи функціонально-планувального розвитку, який передбачений генеральним планом, виділено функціональні типи території, що поділяються на планувальні елементи – територіальні зони.

Межі територіальних зон встановлені по
- лініях магістралей
- вулиць
- проїздів, що розділяють транспортні потоки протилежних напрямів
- червоних лініях
- межах земельних ділянок
- кордонах населених пунктів
- межах природних об'єктів
- інших кордонах.

Назви і кодові позначення зон групуються за видами. Зонуванням в межах населеного пункту села Кінські Роздори встановлюються такі типи територіальних зон:

Громадські зони – Г

Г-1 Громадська зона розміщення сільського центру та повсякденного обслуговування

Призначаються для розташування адміністративних, наукових, ділових, фінансових, торгівельних установ, закладів обслуговування та супутніх до них елементів транспортної та інженерної інфраструктури. Зона призначена для обслуговування населення.

Г-3 Зона розміщення навчальних закладів

Призначаються для розташування вищих навчальних закладів, закладів середньої спеціальної освіти, об'єктів наукового обслуговування та закладів з підготовки, перепідготовки та підвищення кваліфікації кадрів.

Зони встановлюються з метою концентрації освітніх і супутніх до них функцій: навчальних, інформаційних, культурних, оздоровчих, дозвілля.

Г-4, П-Г-4 Зона розміщення культурних та спортивних закладів

Призначаються для розташування спортивних закладів, майданчиків та інших спортивних споруд, а також для розміщення культурно-освітніх закладів таких як клуби, бібліотеки, кінотеатри, гуртки, музеї, культових споруд тощо.

Г-5 Зона розміщення лікувальних закладів

Призначаються для розташування лікарень, поліклініки, амбулаторій, аптек, інших лікувальних закладів. Зону формують території, на яких розміщуються об'єкти, що відносяться для установ охорони здоров'я та соціального забезпечення.

П-Г-6 Торгівельна зона

Призначаються для розташування магазинів, торгівельних комплексів, ринків, ринкових комплексів. Зону формують території громадської забудови, на яких за містобудівною документацію розміщуються торгівельні заклади та інші об'єкти обслуговування населення.

Житлові зони – Ж

До житлових зон відносяться території, що призначаються для розташування житлових будинків, споруд для зберігання індивідуальних транспортних засобів, окремих вбудованих чи прибудованих об'єктів соціального і культурно-побутового обслуговування населення та інших об'єктів, що не потребують встановлення санітарно-захисних зон та не створюють негативного впливу на навколишнє середовище.

Житлові зони призначені для забудови житловими будинками різних типів і поверховості в залежності від місця розташування і характеру забудови території населеного пункту. Житлові зони формуються на території існуючої сельбищної забудови населеного пункту та в районах, передбачених містобудівною документацією під нову житлову забудову.

Ж-1, П-Ж-1 Зона садибної забудови

Призначається для розташування одноквартирних житлових будинків до 4 поверхів (включно з мансардним поверхом) із земельними ділянками або зблокованих житлових будинків на сусідніх земельних ділянках.

П-Ж-1/1 Зона садибної забудови в санітарно-захисній зоні промислових підприємств I-V класу шкідливості, комунальних, складських, сільськогосподарських підприємств

Ж-1/24 Зона садибної забудови в охоронних зонах магістральних електромереж

Ж-1/27 Зона садибної забудови в охоронних зонах магістрального газопроводу

Зони на яких діють планувальні обмеження.

Ж-3 Багатоквартирна житлова забудови

Призначається для розташування багатоквартирних житлових будинків до 2-5 поверхів, супутніх об'єктів повсякденного обслуговування та інше.

Ж-3/1 Зона багатоквартирної житлової забудови в санітарно-захисній зоні промислових підприємств I-V класу шкідливості, комунальних, складських, сільськогосподарських підприємств

Зони на яких діють планувальні обмеження.

Ландшафтно – рекреаційні зони – Р

До рекреаційних зон належать території, що призначаються і використовуються для відпочинку населення. Крім рекреаційних, ці території можуть виконувати функції охоронні, захисні, санітарно-гігієнічні і мати історико-культурний потенціал.

Р-1-1/11 Рекреаційна зона природних ландшафтів в прибережній захисній смузі

Зона призначається для виконання рекреаційних функцій в деяких місцях ПЗС з використанням водних об'єктів. До неї належать території

об'єктами для відпочинку на пляжних об'єктах. Ці території мають бути забезпечені високим рівнем благоустрою, належним переліком споруд для відпочинку, тимчасових споруд та інших об'єктів супутніх видів активності.

Р-3-1, П-Р-3-1 Зона розміщення парків, скверів, міських садів, бульварів

Призначається для повсякденного відпочинку населення і включає парки, сквери, сади, бульвари, міські ліси, водойми, пляжі, лугопарки, лісопарки, гідропарки, меморіальні та інші спеціалізовані парки. Мета організації зони полягає в забезпеченні мешканців населеного пункту місцями відпочинку з високим рівнем благоустрою (парки, сади, сквери, бульвари, водойми).

Зона транспортної інфраструктури ТР

ТР-2 Зона транспортної інфраструктури вулиць в червоних лініях

Відносяться території вулиць, майданів (в межах червоних ліній) доріг.

Зони інженерної інфраструктури – ІН

ІН-1 Зона розміщення об'єктів інженерної інфраструктури електромереж

Призначена для розміщення головних об'єктів електромережі.

ІН-2 Зона розміщення головних об'єктів водопостачання, каналізації, газопостачання

Призначається для розміщення мереж та об'єктів водопостачання та каналізації та газопостачання

Комунально складські зони – КС

КС-4, П-КС-4 Зона розміщення об'єктів IV класу санітарної класифікації СЗЗ-100 м

Призначається для розміщення проектних об'єктів, що потребують встановлення СЗЗ 100 м

Призначається для розміщення проектних об'єктів, що потребують встановлення СЗЗ 100 м

КС-4-1 Зона розміщення об'єктів IV класу санітарної класифікації (кладовище) СЗЗ-100 м

Призначається для розміщення об'єктів, що потребують встановлення СЗЗ 100 м

П-КС-5 Зона розміщення об'єктів V класу санітарної класифікації

Призначається для розміщення об'єктів, що потребують встановлення СЗЗ 50 м

Виробничі зони – В

В-4 Зона розміщення підприємств IV класу шкідливості СЗЗ 100 м

Призначається для існуючих підприємств, що є джерелами забруднення навколишнього середовища і потребують встановлення СЗЗ – 100 м

В-5 Зона розміщення підприємств V класу шкідливості СЗЗ 50 м

Призначається для існуючих підприємств, що є джерелами забруднення навколишнього середовища і потребують встановлення СЗЗ – 50 м

Зони сільськогосподарського призначення СВ

СВ-1 Зона земель сільськогосподарського призначення

Використовується для багаторічних насаджень, ріллі, сіножатей та пасовищ, господарських шляхів і прогонів, фермерських господарств.

СВ-1/1 Зона земель підприємств лісового господарства в СЗЗ промислових підприємств I-V класу шкідливості, сільськогосподарських, комунальних, складських територій

СВ-1/27 Зона земель сільськогосподарського призначення в охоронній зоні магістрального газопроводу

Зони на яких діють планувальні обмеження.

СВ-2-4 Зона сільськогосподарських підприємств, установ та організацій з СЗЗ-100 м

Використовуються для науково – дослідних, навчальних цілей, ведення товарного сільськогосподарського виробництва.

СВ-2-5 Зона сільськогосподарських підприємств, установ та організацій з СЗЗ-50м

Використовуються для науково – дослідних, навчальних цілей, ведення товарного сільськогосподарського виробництва.

Спеціальні зони – С

П-С-4 Зона озеленення спеціального призначення

Зона формується в межах територій, на яких за містобудівною документацію передбачається організація санітарно – захисних зон.

Інші зони

ВП Водні поверхні

Зона існуючі водних поверхонь річок та ставків

ІК Зона земель історико – культурного призначення

Зона розміщення курганів та інших історико-культурних об'єктів

Крім основних типів територіальних зон генеральним планом обумовлено появу зон з кодовими позначками: " П " – Проектні, який стоїть перед кодом зони

. Це зони, розташовані на територіях, де за генпланом на розрахунковий період визначена Проектна забудова того чи іншого призначення, зі зміною функціонального призначення існуючої забудови або без такої.

Переважні та супутні види забудови та використання земельних ділянок в межах зон з такими кодовими позначками ідентичні видам забудови та використання земельних ділянок без таких кодових позначок.

5. Містобудівні регламенти як сукупність обов'язкових вимог до використання земельних ділянок та об'єктів нерухомості, що встановлюються у межах відповідних територіальних зон

Сукупність видів використання та граничних параметрів нового будівництва та реконструкції об'єктів нерухомості у складі містобудівного регламенту є єдиною для усіх об'єктів у межах відповідної зони (підзони), якщо інше не обумовлене у складі регламенту.

Містобудівні регламенти підзон можуть відрізнятися від містобудівного регламенту територіальних зон тільки за окремими показниками дозволеного будівництва, обумовленими дією планувальних обмежень.

Для окремої земельної ділянки дозволеним є таке використання, яке відповідає містобудівному регламенту зони (підзони), на території якої ділянка знаходиться. Невідповідність наміру забудови встановленим видам дозволеного використання земельних ділянок і об'єктів, зазначеним у містобудівному регламенті, означає, що його застосування у відповідній територіальній зоні не допускається.

Суттєва зміна параметрів існуючих земельних ділянок і об'єктів нерухомості, види використання і граничні параметри яких не відповідають містобудівному регламенту, можлива лише шляхом приведення таких об'єктів у відповідність з містобудівним регламентом або шляхом зменшення їх невідповідності.

Розташування в межах земельних ділянок супутніх видів забудови – інженерно-технічних об'єктів, споруд, комунікацій, що забезпечують реалізацію дозволеного використання об'єктів нерухомості на цих ділянках, можливе за умов обов'язкового дотримання технічних умов (норм).

Земельні ділянки та розташовані на них об'єкти, які існували до впровадження в дію зонінгу, граничні параметри яких не відповідають містобудівному регламенту, можуть використовуватись без визначення терміну їх приведення у відповідність з містобудівним регламентом, якщо вони
не створюють загрози для життя, здоров'я людей, для навколишнього середовища, об'єктів культурної спадщини та природно-заповідного фонду.

Зміна видів використання земельних ділянок і об'єктів нерухомості фізичними та юридичними особами здійснюється у відповідності з переліком переважних, супутніх видів забудови в межах відповідної територіальної зони за дотримання інших вимог містобудівних регламентів та в порядку, визначеному законодавством.

Види територіальних зон, перелік видів використання земельних ділянок, параметри забудови у складі містобудівних регламентів конкретизуються в залежності від містобудівних особливостей населеного пункту, місцевих умов, рішень містобудівної документації.

6. Перелік дозволених видів забудови та іншого використання земельних ділянок у межах різних територіальних зон

Громадські зони – Г

Г-1 Зона розміщення об'єктів сільського центру та повсякденного обслуговування

Переважні види використання:

- Адміністративні будівлі організацій;
- Установи управління;
- Нотаріальні контори;
- Офіси;
- ЦНАП;
- Об'єкти побутового обслуговування населення;
- Відділення банку, пошта;
- Об'єкти торгівлі та громадського харчування;
- Пам'ятні знаки, монументи, малі архітектурні форми, об'єкти благоустрою.

Супутні види використання:

- Об'єкти, що технологічно пов'язані з об'єктами переважних видів або сприяють їх безпеці, в тому числі, протипожежні;
- Споруди, що призначені для охорони об'єктів переважного чи допустимого виду використання;
- Об'єкти інженерної інфраструктури;
- Об'єкти транспортної інфраструктури (автостоянки, велостоянки, гаражі, паркінги наземні та підземні);
- Дитячі майданчики, місця для відпочинку;
- Тимчасові споруди;
- Громадські вбиральні

Г-3 Зона розміщення навчальних закладів

Переважні види використання:

- Установи освіти та виховання в тому числі загально освітні та інші школи;
- Дитячи садочки;
- Наукові та науково-пошукові заклади;
- Центри наукової інформації, бібліотеки;
- спортивні майданчики, тенісні корти інше;
- Школи мистецтв;
- Школи-інтернати для дітей;
- Об'єкти благоустрою (дитячі, спортивні майданчики, місця для відпочинку);
- Пам'ятні знаки, історичні та культурно-освітні.

Супутні види використання:

- Об'єкти, що технологічно пов'язані з об'єктами переважних видів або сприяють їх безпеці, в тому числі, протипожежні, відповідно до чинної нормативно-технічної документації;
- Споруди, що призначені для охорони об'єктів переважного чи допустимого виду використання;

- Об'єкти інженерної інфраструктури;
- Об'єкти транспортної інфраструктури (автостоянки, велостоянки, гаражі, паркінги наземні та підземні)
- Тимчасові споруди;
- Громадські вбиральні.

Г-4, П-Г-4 Зона розміщення культурних та спортивних закладів

Переважні види використання:
- Спортзали, басейні;
- Фізкультурно-оздоровчі комплекси;
- Спортивні майданчики, тенісні корти, стадіони;
- Будівлі культурно-масової роботи;
- Танцювальні зали;
- Клубні установи та центри дозвілля;
- Кінотеатри;
- Бібліотеки;
- Культові споруди;
- Пам'ятні знаки, історичні та культурно-освітні,
- Заклади громадського харчування;
- Об'єкти благоустрою (дитячі, спортивні майданчики, місця для відпочинку);
- Малі архітектурні форми.

Супутні види використання:
- Об'єкти, що технологічно пов'язані з об'єктами переважних видів або сприяють їх безпеці, в тому числі, протипожежні, відповідно до чинної нормативно-технічної документації;
- Споруди, що призначені для охорони об'єктів переважного чи допустимого виду використання;
- Об'єкти інженерної інфраструктури;
- Об'єкти транспортної інфраструктури (автостоянки, велостоянки, гаражі, паркінги наземні та підземні)
- Тимчасові споруди;
- Громадські вбиральні.

Г-5 Зона розміщення лікувальних закладів

Переважні види використання:
- Стаціонари усіх типів;
- ФАП, поліклініки, амбулаторії, диспансери без стаціонару;
- Станції (підстанції) швидкої медичної допомоги;
- Санітарно-епідеміологічні установи;
- Будинки-інтернати, територіальні центри соціального обслуговування людей похилого віку та інвалідів;
- Аптеки;
- Об'єкти благоустрою.

Супутні види використання:

- Об'єкти, що технологічно пов'язані з об'єктами переважних видів або сприяють їх безпеці, в тому числі, протипожежні, відповідно до чинної нормативно-технічної документації;
- Споруди, що призначені для охорони об'єктів переважного чи допустимого виду використання;
- Об'єкти інженерної інфраструктури;
- Об'єкти транспортної інфраструктури (автостоянки, велостоянки, гаражі, паркінги наземні та підземні);
- Тимчасові споруди;
- Громадські вбиральні.

П-Г-6 Торгівельна зона

Переважні види використання:

- Ринкові комплекси;
- Торгівельна – виставкові павільйони, комплекси;
- Логістичні центри;
- Готелі, мотелі;
- Об'єкти громадського харчування;
- Тимчасові споруди;
- Об'єкти благоустрою.

Супутні види використання:

- Об'єкти, що технологічно пов'язані з об'єктами переважних видів або сприяють їх безпеці, в тому числі, протипожежні, відповідно до чинної нормативно-технічної документації;
- Споруди, що призначені для охорони об'єктів переважного чи допустимого виду використання;
- Об'єкти інженерної інфраструктури;
- Об'єкти транспортної інфраструктури (автостоянки, велостоянки, гаражі, паркінги наземні та підземні);
- Громадські вбиральні.

Житлові зони Ж

Ж-1, П-Ж-1 Зона садибної забудови

Переважні види використання:

- Окремі житлові будинки садибного типу;
- Блоковані житлові будинки на 2 сім'ї;
- Дитячі дошкільні установи;
- Дитячі дошкільні установи об'єднані з початковою школою;
- Окремо розташовані та вбудовано-прибудовані індивідуальні гаражі;
- Окремо розташовані або вбудовано-прибудовані господарські будівлі;
- Оранжереї та теплиці;

- Окремі вбудовані чи прибудовані об'єкти повсякденного обслуговування: магазини, перукарні, аптеки, об'єкти побутового обслуговування;
- На присадибних ділянках дозволяється вирощування квітів, фруктів, овочів, розведення птиці, індивідуальна трудова діяльність;
- Об'єкти благоустрою.

Супутні види використання:

- Об'єкти, що технологічно пов'язані з об'єктами переважних видів або сприяють їх безпеці, в тому числі, протипожежні, відповідно до чинної нормативно-технічної документації;
- Споруди, що призначені для охорони об'єктів переважного чи допустимого виду використання;
- Об'єкти інженерної інфраструктури;
- Об'єкти транспортної інфраструктури (автостоянки, велостоянки, гаражі, паркінги наземні та підземні).
- Тимчасові споруди для здійснення підприємницької діяльності.

Масиви нової забудови

- Максимальна площа земельної ділянки – 0.25 га
- Мінімальна довжина лицьової сторони ділянки (по фронту вулиці) – 25 м
- Мінімальна ширина (глибина) ділянки– 50 м
- Максимальна висота огорожі – 1.7 м

Ж-1/1 Зона садибної забудови в санітарно-захисній зоні промислових підприємств I-V класу шкідливості, сільськогосподарських, комунальних, складських територій

Ж-1/24 Зона садибної забудови в охоронних зонах магістральних електромереж

Ж-1/27 Зона садибної забудови в охоронній зоні магістрального газопроводу

Переважні види використання:

- Заборона на нове будівництво, можлива реконструкція існуючих будівель та споруд;
- Зелені насадження.

Супутні види використання:

- Об'єкти, що технологічно пов'язані з об'єктами переважних видів або сприяють їх безпеці, в тому числі, протипожежні, відповідно до чинної нормативно-технічної документації;
- Споруди, що призначені для охорони об'єктів переважного чи допустимого виду використання;
- Об'єкти інженерної інфраструктури.

Зона на якій діють планувальні обмеження згідно ДСП «Державні санітарні правила планування та забудова населених пунктів» від 19.06.96 р. № 173 та ДБН Б.2.2-12:2018 «Планування і забудова територій»

Ж-3 Багатоквартирна житлова забудови

Переважні види використання:

- Житлові будинки 2-5-поверхові, окремо розташовані або зблоковані;
- Вбудовані або прибудовані спеціалізовані учбові заклади всіх типів, дитячі дошкільні установи, бібліотеки, виставочні зали;
- Окремо розташовані і вбудовано-прибудовані адміністративні установи, підприємства торгівлі, обслуговування, громадського харчування, амбулаторії, консультативні медичні заклади, поштові відділення
- Озеленені території, місця для відпочинку, дитячі та спортивні майданчики;
- Господарські майданчики.

Супутні види використання:

- Об'єкти, що технологічно пов'язані з об'єктами переважних видів або сприяють їх безпеці, в тому числі, протипожежні, відповідно до чинної нормативно-технічної документації;
- Споруди, що призначені для охорони об'єктів переважного чи допустимого виду використання;
- Об'єкти інженерної інфраструктури;
- Об'єкти транспортної інфраструктури (автостоянки, велостоянки, гаражі, паркінги наземні та підземні).

Ж-3/1 Зона багатоквартирної житлової забудови в санітарно-захисній зоні промислових підприємств I-V класу шкідливості, комунальних, складських, сільськогосподарських підприємств

Переважні види використання:

- Заборона на нове будівництво, можлива реконструкція існуючих будівель та споруд;
- Зелені насадження.

Супутні види використання:

- Об'єкти, що технологічно пов'язані з об'єктами переважних видів або сприяють їх безпеці, в тому числі, протипожежні, відповідно до чинної нормативно-технічної документації;
- Споруди, що призначені для охорони об'єктів переважного чи допустимого виду використання;
- Об'єкти інженерної інфраструктури.

Зона на якій діють планувальні обмеження згідно ДСП «Державні санітарні правила планування та забудова населених пунктів» від 19.06.96 р. № 173 та ДБН Б.2.2-12:2018 «Планування і забудова територій».

Ландшафтно – рекреаційні зони Р

Р-1-1 Рекреаційна зона природних ландшафтів

Переважні види використання:

- Майданчики для відпочинку дорослих та дітей;
- Рекреаційні установи культурно-оздоровчих цілей;
- Місця короткочасного відпочинку з відповідним обладнанням;
- Малі архітектурні форми;
- Адміністративно-господарські споруди;
- Заклади прокату необхідного інвентарю;
- Заклади громадського харчування, торгівлі та сервісного обслуговування;
- Тимчасові споруди для обслуговування даної зони.

Супутні види використання:

- Об'єкти, що технологічно пов'язані з об'єктами переважних видів або сприяють їх безпеці, в тому числі, протипожежні, відповідно до чинної нормативно-технічної документації;
- Споруди, що призначені для охорони об'єктів переважного чи допустимого виду використання;
- Об'єкти інженерної інфраструктури;
- Об'єкти транспортної інфраструктури (автостоянки, велостоянки, гаражі, паркінги наземні та підземні);
- Громадські вбиральні.

Р-1-1/11 Рекреаційна зона природних ландшафтів в прибережній захисній смузі

Переважні види використання:

- Майданчики для відпочинку дорослих та дітей;
- Місця короткочасного відпочинку з відповідним обладнанням;
- Малі архітектурні форми, об'єкти благоустрою;
- Заклади прокату необхідного інвентарю;
- Тимчасові споруди для обслуговування даної зони.

Супутні види використання:

- Об'єкти, що технологічно пов'язані з об'єктами переважних видів або сприяють їх безпеці, в тому числі, протипожежні, відповідно до чинної нормативно-технічної документації;
- Споруди, що призначені для охорони об'єктів переважного чи допустимого виду використання;
- Об'єкти інженерної інфраструктури;
- Об'єкти транспортної інфраструктури (автостоянки, велостоянки, гаражі, паркінги наземні та підземні);
- Громадські вбиральні.

Р-3-1, П-Р-3-1 Зона розміщення парків, скверів, міських садів, бульварів

Переважні види використання:

- Малі архітектурні форми;
- Об'єкти благоустрою, майданчики для відпочинку
- Дитячі та спортивні майданчики, тенісні корти, баскетбольні площадки та інше;
- Пункти прокату інвентарю;
- Об'єкти громадського харчування;
- Тимчасові споруди для обслуговування даної зони.

Супутні види використання:

- Об'єкти, що технологічно пов'язані з об'єктами переважних видів або сприяють їх безпеці, в тому числі, протипожежні, відповідно до чинної нормативно-технічної документації;
- Споруди, що призначені для охорони об'єктів переважного чи допустимого виду використання;
- Об'єкти інженерної інфраструктури;
- Об'єкти транспортної інфраструктури (автостоянки, велостоянки, гаражі, паркінги наземні та підземні).
- Громадські вбиральні.

- Мінімальний коефіцієнт озеленення – 75%

Зона транспортної інфраструктури ТР

ТР-2 Зона транспортної інфраструктури вулиць в червоних лініях

Переважні види використання:

- Проїзні частини, пішохідні тротуари, велосипедні доріжки;
- Пішохідні переходи;
- Зупинки громадського транспорту та їх обладнання, з кіосками продажу проїзних квітів;
- Захисні зелені насадження вздовж проїзної частини;
- Транспортні розв'язки;
- Споруди лінійного та енергетичного господарства;
- Інженерні комунікації;
- Огорожа вулиць та відбійники;
- Дорожня інформація (знаки та ін.).

Супутні види використання:

- Об'єкти, що технологічно пов'язані з об'єктами переважних видів або сприяють їх безпеці, в тому числі, протипожежні, відповідно до чинної нормативно-технічної документації;
- Споруди, що призначені для охорони об'єктів переважного чи допустимого виду використання;

- Об'єкти транспортної інфраструктури (автостоянки, велостоянки, гаражі, паркінги наземні та підземні).

Зона інженерної інфраструктури ІН

ІН-1 Зона розміщення об'єктів інфраструктури електромереж

Переважні види використання:
- Електричні підстанції;
- Трансформаторні підстанції;
- Технологічні проїзди та проходи;
- Огорожі;
- Адміністративні будівлі та споруди, що пов'язані з функціонуванням об'єктів зони;
- Зелені насадження спеціального призначення;
- Споруди інженерної інфраструктури.

Супутні види використання:
- Об'єкти, що технологічно пов'язані з об'єктами переважних видів або сприяють їх безпеці, в тому числі, протипожежні, відповідно до чинної нормативно-технічної документації;
- Споруди, що призначені для охорони об'єктів переважного чи допустимого виду використання;
- Об'єкти транспортної інфраструктури (автостоянки, велостоянки, гаражі, паркінги наземні та підземні).

ІН-2 Зона розміщення головних об'єктів водопостачання, каналізації, газопостачання

Переважні види використання:
- Насосні станції, водонапірні башти; резервуари;
- Каналізаційні насосні станції;
- ГРП, ЗТП;
- Технологічні проїзди та проходи;
- Огорожі;
- Зелені насадження спеціального призначення;
- Споруди інженерної інфраструктури;

Супутні види використання:
- Об'єкти, що технологічно пов'язані з об'єктами переважних видів або сприяють їх безпеці, в тому числі, протипожежні, відповідно до чинної нормативно-технічної документації;
- Споруди, що призначені для охорони об'єктів переважного чи допустимого виду використання;
- Об'єкти транспортної інфраструктури (автостоянки, велостоянки, гаражі, паркінги наземні та підземні).

Комунально складські зони КС

КС-4, П-КС-4 Зона розміщення об'єктів IV класу санітарної класифікації СЗЗ-100 м

Переважні види використання:

- АЗС,АГЗС;
- СТО;
- Шино монтаж, автомійки вантажного та легкового транспорту;
- Служби автомобільних доріг;
-
- Адміністративні будівлі та споруди, що пов'язані з функціонуванням зони;
- Об'єкти транспортної інфраструктури (автостоянки, велостоянки, гаражі);
- Зелені насадження.

Супутні види використання:

- Об'єкти, що технологічно пов'язані з об'єктами переважних видів або сприяють їх безпеці, в тому числі, протипожежні, відповідно до чинної нормативно-технічної документації;
- Споруди, що призначені для охорони об'єктів переважного чи допустимого виду використання;
- Об'єкти інженерної інфраструктури;
- Громадські вбиральні.

КС-4-1 Зона розміщення об'єктів IV класу санітарної класифікації (закриваємі кладовища) СЗЗ – 100 м

Переважні види використання:

- Кладовища;
- Технологічні проїзди та проходи;
- Огорожі;
- Адміністративні будівлі та споруди, що пов'язані з функціонуванням зони;
- Зелені насадження
- Громадські вбиральні;
- Храми, альтанки;
- Зелені насадження

Супутні види використання:

- Об'єкти, що технологічно пов'язані з об'єктами переважних видів або сприяють їх безпеці, в тому числі, протипожежні, відповідно до чинної нормативно-технічної документації;
- Споруди, що призначені для охорони об'єктів переважного чи допустимого виду використання;
- Об'єкти інженерної інфраструктури;

- Об'єкти транспортної інфраструктури (автостоянки, велостоянки, гаражі).

П-КС-5 Зона розміщення об'єктів V класу санітарної класифікації СЗЗ – 50 м

Переважні види використання:
- Підприємства по обслуговуванню автомобілів;
- Пожежні депо;
- Підприємства комунального господарства;
- Будівельні двори;
- Гаражі, автомобільні стоянки для тимчасового зберігання транспортних засобів, автотранспортні підприємства інші об'єкти з санітарно-захисною зоною не більш 50 м;
- Адміністративні будівлі та споруди, що пов'язані з функціонуванням об'єктів зони;
- Зелені насадження спеціального призначення.

Супутні види використання:
- Об'єкти, що технологічно пов'язані з об'єктами переважних видів або сприяють їх безпеці, в тому числі, протипожежні, відповідно до чинної нормативно-технічної документації;
- Споруди, що призначені для охорони об'єктів переважного чи допустимого виду використання;
- Об'єкти інженерної інфраструктури;
- Громадські вбиральні.

Виробничі зони – В

В-4 Зона розміщення підприємств IV класу шкідливості – 100 м

Призначається для існуючих підприємств, що є джерелами забруднення навколишнього середовища і потребують встановлення СЗЗ – 100 м

Переважні види використання:
- Цегельний завод;
- Адміністративні будівлі та споруди, що пов'язані з функціонуванням об'єктів зони;
- Зелені насадження спеціального призначення.

Супутні види використання:
- Об'єкти, що технологічно пов'язані з об'єктами переважних видів або сприяють їх безпеці, в тому числі, протипожежні, відповідно до чинної нормативно-технічної документації;
- Споруди, що призначені для охорони об'єктів переважного чи допустимого виду використання;
- Об'єкти інженерної інфраструктури;
- Громадські вбиральні.

В-5 Зона розміщення підприємств IV класу шкідливості – 50 м

Призначається для існуючих підприємств, що є джерелами забруднення навколишнього середовища і потребують встановлення СЗЗ – 50 м

Переважні види використання:

- Підприємство по виробництву електротехнічної продукції;
- Адміністративні будівлі та споруди, що пов'язані з функціонуванням об'єктів зони;
- Зелені насадження спеціального призначення.

Супутні види використання:

- Об'єкти, що технологічно пов'язані з об'єктами переважних видів або сприяють їх безпеці, в тому числі, протипожежні, відповідно до чинної нормативно-технічної документації;
- Споруди, що призначені для охорони об'єктів переважного чи допустимого виду використання;
- Об'єкти інженерної інфраструктури;
- Громадські вбиральні.

Зони сільськогосподарського призначення СВ

СВ-1 Зона земель сільськогосподарського призначення

Переважні види використання:

- Пішохідні доріжки, проїзди, проходи дороги;
- Багаторічні зелені насадження, ріллі, пасовища, зелені насадження спецпризначення;
- Фермерські господарства.

Супутні види використання:

- Об'єкти, що технологічно пов'язані з об'єктами переважних видів або сприяють їх безпеці, в тому числі, протипожежні, відповідно до чинної нормативно-технічної документації;
- Споруди, що призначені для охорони об'єктів переважного чи допустимого виду використання;
- Об'єкти інженерної інфраструктури;
- Об'єкти транспортної інфраструктури (автостоянки, велостоянки, гаражі, паркінги наземні та підземні).
- Громадські вбиральні.

СВ-1/1 Зона земель сільськогосподарського призначення в СЗЗ промислових підприємств
СВ-1/27 Зона земель сільськогосподарського призначення в охоронній зоні магістрального газопроводу
СВ-1/30 Зона земель сільськогосподарського призначення з обмеженнями на територіях всіх видів зон охорони пам'яток культурної спадщини (5 м від підошви кургану)

Переважні види використання:

- Пішохідні доріжки, проїзди, проходи дороги;
- Багаторічні зелені насадження, зелені насадження спецпризначення;
- Підприємства по вирощуванню декоративних рослин.

Супутні види використання:

- Об'єкти, що технологічно пов'язані з об'єктами переважних видів або сприяють їх безпеці, в тому числі, протипожежні, відповідно до чинної нормативно-технічної документації;
- Споруди, що призначені для охорони об'єктів переважного чи допустимого виду використання;
- Об'єкти інженерної інфраструктури;
- Об'єкти транспортної інфраструктури (автостоянки, велостоянки, гаражі, паркінги наземні та підземні).

Зона на якій діють планувальні обмеження згідно ДСП «Державні санітарні правила планування та забудова населених пунктів» від 19.06.96 р. № 173 та ДБН Б.2.2-12:2018 «Планування і забудова територій»

СВ-2-4 Зона сільськогосподарських підприємств, установ та організацій з СЗЗ - 100 м

Переважні види використання:

- Гаражі та підприємства по ремонту сільгосптехніки;
- Сільськогосподарські підприємства рослинницькі, тваринницькі с СЗЗ не більш 100 м;
- Підприємства по переробці та зберіганню сільськогосподарської продукції с СЗЗ не більш 100 м;
- Склади та овочесховища с СЗЗ не більш 100 м.

Супутні види використання:

- Об'єкти, що технологічно пов'язані з об'єктами переважних видів або сприяють їх безпеці, в тому числі, протипожежні, відповідно до чинної нормативно-технічної документації;
- Споруди, що призначені для охорони об'єктів переважного чи допустимого виду використання;
- Об'єкти інженерної інфраструктури;
- Громадські вбиральні.

СВ-2-5 Зона сільськогосподарських підприємств, установ та організацій з СЗЗ-50 м

Переважні види використання:

- Сільськогосподарські підприємства рослинницькі, тваринницькі с СЗЗ не більш 100 м;
- Підприємства по переробці та зберіганню сільськогосподарської продукції с СЗЗ не більш 100 м;

- Склади та овочесховища с СЗЗ не більш 100 м.

Супутні види використання:

- Об'єкти, що технологічно пов'язані з об'єктами переважних видів або сприяють їх безпеці, в тому числі, протипожежні, відповідно до чинної нормативно-технічної документації;
- Споруди, що призначені для охорони об'єктів переважного чи допустимого виду використання;
- Об'єкти інженерної інфраструктури;
- Громадські вбиральні.

Спеціальні зони С

П-С-4 Зона озеленення спеціального призначення

Переважні види використання:

- Пішохідні доріжки, проїзди, проходи, дороги;
- Багаторічні зелені насадження.
- Об'єкти комунального господарства зі спеціальними інженерними спорудами;
- Підприємства по обслуговуванню транспортних засобів;
- Адміністративні об'єкти, що пов'язані з функціонуванням спеціальних об'єктів;
- Об'єкти інженерної інфраструктури.
- Зелені насадження спеціального призначення.

Супутні види використання:

- Об'єкти, що технологічно пов'язані з об'єктами переважних видів або сприяють їх безпеці, в тому числі, протипожежні, відповідно до чинної нормативно-технічної документації;
- Споруди, що призначені для охорони об'єктів переважного чи допустимого виду використання;
- Об'єкти транспортної інфраструктури (автостоянки, велостоянки, гаражі, паркінги наземні та підземні).

Інші зони

ІК Зона земель історико – культурного призначення

Переважні види використання:

- Збереження пам'яток історії, археології, культури, архітектури, монументального мистецтва, їх музеєфікація;
- Розміщення допоміжних будинків та споруд для обслуговування існуючих пам'яток, туристичних груп;
- Влаштування виставкової, концертної та іншої супутньої діяльності.

Супутні види використання:

- Об'єкти, що технологічно пов'язані з об'єктами переважних видів або сприяють їх безпеці, в тому числі, протипожежні, відповідно до чинної нормативно-технічної документації;
- Споруди, що призначені для охорони об'єктів переважного чи допустимого виду використання;
- Об'єкти інженерної інфраструктури.

ВП водні поверхні

Переважні види використання:

- Природні водойми (річки, озера,);
- Ставки
- Водотоки (річки, струмки).

Супутні види використання:

- Об'єкти, що технологічно пов'язані з об'єктами переважних видів або сприяють їх безпеці, в тому числі, протипожежні, відповідно до чинної нормативно-технічної документації;
- Споруди, що призначені для охорони об'єктів переважного чи допустимого виду використання;
- Об'єкти інженерної інфраструктури.

ІК Зона земель історико – культурного призначення

Переважні види використання:

- Збереження пам'яток історії, археології, культури, архітектури, монументального мистецтва, їх музеєфікація;
- Розміщення допоміжних будинків та споруд для обслуговування існуючих пам'яток, туристичних груп;
- Влаштування виставкової, концертної та іншої супутньої діяльності.

Супутні види використання:

- Об'єкти, що технологічно пов'язані з об'єктами переважних видів або сприяють їх безпеці, в тому числі, протипожежні, відповідно до чинної нормативно-технічної документації;
- Споруди, що призначені для охорони об'єктів переважного чи допустимого виду використання;
- Об'єкти інженерної інфраструктури.

Сумарна площа об'єктів території зон супутнього виду використання не повинна перевищувати загальну площу переважних видів використання.

Використання території зон, розміщення підприємств і установ и т. д. здійснюється відповідно до вимог ДБН Б.2.2-12:2018.

7. Режими використання території, пов'язані з дією обмежень, що розповсюджуються на територію населеного пункту

Містобудівний регламент стосовно обмеження використання земельних ділянок у зонах з особливими умовами використання територій встановлюють на підставі схеми планувальних обмежень, що розповсюджуються на територію населеного пункту, схеми інженерної підготовки території населеного пункту та історико-архітектурного опорного плану, зон охорони пам'яток культурної спадщини (для історичних населених місць).

Виходячи з розповсюдження дії планувальних обмежень у відповідних зонах на плані зонування виділяються підзони з індексацію планувальних обмежень.

Планувальні обмеження
які діють на території населеного пункту

Обмеження, пов'язані з дотриманням санітарно – гігієнічних та природоохоронних норм:	
Планувальні обмеження	Режим використання і забудови територій, на яких діють планувальні обмеження
Санітарно – захисна зона промислових підприємств	У санітарно-захисних зонах не можна допускати розміщення: -житлових будинків з при домовими територіями, гуртожитків, готелів, будинків для приїжджих, аварійних селищ; -дитячих дошкільних закладів, загальноосвітніх шкіл, лікувально-профілактичних та оздоровчих установ загального та спеціального призначення зі стаціонарами, наркологічних диспансерів; -спортивних споруд, садів, парків, садівницьких товариств; -охоронних зон джерел водопостачання, водозабірних споруд та споруд водопровідної розподільної мережі. Не допускається використання для вирощування сільськогосподарських культур, пасовищ для худоби земель санітарно-захисної зони підприємств, що забруднюють навколишнє середовище високотоксичними речовинами та речовинами, що мають віддалену дію (солі важких металів, канцерогенні речовини, діоксини, радіоактивні речовини та ін.). Заборона розглядати зону як резервну територію для розширення підприємств, розвитку сельбищних територій, якщо містобудівною

	документацією не передбачається перенесення або перепрофілювання промислових та складських підприємств. Можливість сільськогосподарського використання земель санітарно-захисних зон, що не забруднюються вище переліченими речовинами, необхідно визначати за погодженням з територіальними органами Мінсільгосппроду і Міністерства охорони здоров'я України.
Санітарна – захисна зона сільськогосподарських підприємств, виробничих та комунальних території	У санітарно-захисних зонах не можна допускати розміщення: - житлових будинків з прибудинковими територіями, гуртожитків, готелів; дитячих дошкільних закладів, загальноосвітніх шкіл, лікувально-профілактичних та оздоровчих установ; спортивних споруд, зелених насаджень загального користування; -заборона розглядати зону як резервну територію для розширення підприємств, розвитку сельбищних територій.
Прибережна захисна смуга	Рекомендовано розчищення русла річки. На території водоохоронних зон забороняється: -використання стійких та сильнодіючих пестицидів; -влаштування кладовищ, скотомогильників, звалищ, полів фільтрації; -скидання неочищених стічних вод, використовуючи рельєф місцевості (балки, пониззя, кар'єри тощо), а також потічки розорювання земель (крім підготовки грунту для залуження і залісення), а також садівництво та городництво; -зберігання та застосування пестицидів і добрив; влаштування літніх таборів для худоби; -будівництво будь-яких споруд (крім гідротехнічних, -гідрометричних та лінійних), у тому числі баз відпочинку, дач, гаражів та стоянок автомобілів; миття та обслуговування транспортних засобів і техніки; -влаштування звалищ сміття, гноєсховищ, накопичувачів рідких і твердих відходів виробництва, кладовищ, скотомогильників, полів фільтрації тощо.
Санітарно – захисна зона кладовища	заборона на розміщення: - житлових будинків з прибудинковими територіями, гуртожитків, готелів, будинків для приїжджих;

	- дитячих дошкільних закладів, загальноосвітніх шкіл, лікувально-профілактичних та оздоровчих установ загального та спеціального призначення зі стаціонарами, наркологічних диспансерів; - спортивних споруд, садів, садівницьких товариств; - джерел централізованого водопостачання, водозабірних споруд, споруд водопровідної розподільної мережі. - заборона розглядати зону як резервну територію для розвитку сельбищних територій, якщо містобудівною документацією не передбачається закриття об'єктів та, відповідно скорочення СЗЗ. Вимоги до водозабезпечення будівель – обов'язкове підключення до мережі централізованого водопроводу
Обмеження, що пов'язані з охоронною магістральних мереж інженерної інфраструктури та об'єктів на них	
Магістральні електромережі та об'єкти на них	В межах санітарно-захисних зон забороняється: розміщувати житлові і громадські будівлі, дачні ділянки та інші місця перебування людей, майданчики для стоянки та зупинки всіх видів транспорту, підприємства по обслуговуванню автомобілів, а також сховища нафти і нафтопродуктів. Сільськогосподарські угіддя, що знаходяться на території санітарно-захисних зон ПЛЕ, можуть бути використані для вирощування сільськогосподарських культур, що не потребують ручної обробки, тобто повинні бути виключені умови для тривалого перебування людини в зоні дії електричного поля. Охоронні зони: – кабелі силові всіх напруг та кабелі зв'язку – 0,6 м; – ПЛ до 20 кВ охоронна зона – 10 м; – ПЛ 35 кВ охоронна зона – 15 м; – Трансформаторна підстанція — 3 м від огорожі
Водоводи, колектори водовідведення, колектори зливової каналізації	В зонах санітарної охорони свердловин 15 м забороняється: -здійснення діяльності щодо утримання та експлуатації інженерних мереж; – будівництво будівель та споруд в охоронній зоні трубопроводів;

	– будівництво, ліквідацію будівель та споруд, вирубання дерев, встановлення загородження, проведення земляних робіт на глибині понад 0,3 м, розрівнювання ґрунту без письмового дозволу підприємства, яке відає цими мережами та присутності працівника підприємства під час проведення робіт. Відстань від фундаментів будівель та споруд до: – мереж водопроводу та напірної каналізації – 5 м; – мереж самопливної каналізації – 3м; – дренажних мереж – 3м;
Газопроводи	У межах охоронних зон без письмового погодження Оператора ГРМ забороняється: 1) проводити будівельні і монтажні роботи, планування ґрунту; 2) влаштовувати стоянки і зупинки транспортних засобів, тракторів та інших самохідних машин; 3) проводити меліоративні роботи, прокладати зрошувальні та осушувальні канали та зводити споруди меліоративних систем; 4) проводити геолого-знімальні, пошукові, геодезичні та інші вишукувальні роботи, пов'язані з улаштуванням свердловин, шурфів і взяттям проб ґрунту; 5) зводити малі архітектурні форми; 6) проводити дноочищувальні і землечерпальні роботи (в охоронних зонах підвідних газопроводів). У межах охоронних зон забороняється: 1) здійснювати будівництво будь-яких будівель; 2) переміщати, демонтувати, засипати, пошкоджувати покажчики трас підземних газопроводів та місць розташування мережевих споруд на них, контрольно-вимірювальні пункти; 3) відкривати самовільно люки газових колодязів і коверів, двері ГРП, ШРП, ВОГ, установок електрохімічного захисту газопроводів тощо, відкривати і закривати крани і засувки, відключати і включати електроживлення обладнання об'єктів газорозподільної системи; 4) влаштовувати звалища, виливати агресивні рідини, в тому числі розчини кислот, солей і лугів; 5) складувати матеріали та обладнання, в тому числі для тимчасового зберігання, вздовж траси підземного газопроводу в межах 2 метрів по обидва боки від осі, а також проводити посадку дерев і чагарників всіх видів в межах 1,5 метра по обидва боки від осі газопроводу;

	6) руйнувати споруди і пристрої, що запобігають пошкодженню газопроводів і споруд на них; 7) кидати якорі, проходити з відданими якорями, ланцюгами, лотами, волокушами, проводити тралення жорсткими і напівжорсткими тралами при перетинанні газопроводами водних перешкод (в охоронних зонах підвідних газопроводів); 8) розпалювати вогнище і розміщувати будь-які відкриті або закриті джерела вогню; 9) проводити будь-які заходи, пов'язані з великим скупченням людей, не зайнятих виконанням дозволених в установленому порядку робіт. Охоронні зони та відстань від фундаментів будівель та споруд до: Газопроводу горючих газів: - низького тиску до 0.05 кгс/кв.см2 -2 м; - газопроводи горючих газів середнього тиску від 0.05 до 3 кгс/кв.см2 -4 м; - газопроводи горючих газів високого тиску від 3 до 6 кгс/кв.см2 - 7 м; - газопроводи горючих газів високого тиску до понад 6 до 12 кгс/кв.см2 – 10 м; - навколо будівель ГРП, ШРП, ВОГ – у вигляді ділянки землі, обмеженої умовною лінією, віддаленої від зовнішніх стін будинку (шаф) ГРП, ВОГ, ШРП при тиску газу на вводі в ГРП, ШРП, ВОГ до 0,6 МПа на 10 метрів у всі сторони, а при тиску газу на вводі в ГРП, ШРП, ВОГ понад 0,6 до 1,2 МПа – на 15 м у всі сторони.
Вимоги до ділянок, що знаходяться в охоронних зонах пам'яток культурної спадщини	
Зона охорони археологічного культурного шару	Заборона - на містобудівні, архітектурні чи ландшафтні перетворення, будівельні, меліоративні, шляхові роботи без дозволу відповідного органу охорони культурної спадщини; -здійснення обстеження та археологічного нагляду за проведенням робіт під час проведення земляних робіт чи нового будівництва на вже забудованих ділянках міста; обов'язкове попереднє археологічне обстеження у випадку проведенням будівельних робіт на нових територіях

8. Додатки

- Зменшена копія креслення: План зонування території
- Рішення Широківської сільської ради про розробку містобудівної документації «Генеральний план села Лукашеве Запорізького району Запорізької області. Оновлення з розширенням меж населеного пункту та план зонування села Лукашеве Запорізького району Запорізької області (у складі генерального плану).
- Завдання на проектування генерального плану з планом зонування території села Лукашеве Запорізького району Запорізької області.
- Лист Запорізької обласної державної адміністрації № 00158/08-27 від 05.02.2018 «Про визначення та врахування державних та регіональних інтересів під час розроблення генерального плану села Лукашеве».
- Копія кваліфікаційного сертифіката серія АА № 003280 зареєстрованого 14 липня 2016 року. Розроблення містобудівної документації.

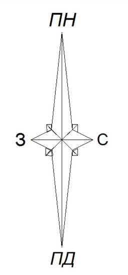

село Лукашеве
Запорізького району, Запорізької області

План зонування території
1:5000

Умовні позначення

Межа населеного пункту проектна

- Громадські зони - Г

Г-1	Зона розміщення об'єктів сільського центру, та повсякденного обслуговування
Г-3	Зона розміщення навчальних закладів
Г-4	Зона розміщення культурних та спортивних закладів
П-Г-4	Зона розміщення культурних та спортивних закладів проектна
Г-5	Зона розміщення лікувальних закладів
П-Г-6	Торгівельна зона проектна

- Житлові зони - Ж

Ж-1	Зона садибної забудови
П-Ж-1	Зона садибної забудови проектна
Ж-1/1	Зона садибної забудови в санітарно-захисній зоні промислових підприємств I-V класу шкідливості, сільськогосподарських, комунальних, складських територій
Ж-1/27	Зона садибної забудови в охоронній зоні магістрального газопроводу
Ж-1/24	Зона садибної забудови в охоронних зонах магістральних електромереж (умовно не вказано)
Ж-3	Багатоквартирна житлова забудова
Ж-3/1	Багатоквартирна житлова забудова в санітарно-захисній зоні промислових підприємств I-V класу шкідливості, сільськогосподарських, комунальних, складських територій

- Ландшафтно-рекреаційні зони - Р

Р-1-1/11	Рекреаційна зона природних ландшафтів в прибережна захисній смузі
Р-3-1	Зона розміщення парків, скверів, садів, бульварів
П-Р-3-1	Зона розміщення парків, скверів, садів, бульварів проектна

- Зони транспортної інфраструктури - ТР

ТР-2	Зона транспортної інфраструктури в межах червоних ліній

- Зони інженерної інфраструктури - ІН

ІН-1	Зона розміщення головних об'єктів електромереж
ІН-2	Зона розміщення головних об'єктів водопостачання, каналізації, газопостачання

- Комунально-складські зони - КС

КС-4	Зона розміщення об'єктів IV класу санітарної класифікації СЗЗ-100 м.
П-КС-4	Зона розміщення об'єктів IV класу санітарної класифікації СЗЗ-100 м. проектна
КС-4-1	Зона розміщення об'єктів IV класу санітарної класифікації (кладовище) СЗЗ-100 м.
П-КС-5	Зона розміщення об'єктів V класу санітарної класифікації СЗЗ-50 м.

- Виробничі зони - В

В-4	Зона розміщення підприємств IV класу шкідливості СЗЗ 100 м.
В-5	Зона розміщення підприємств V класу шкідливості СЗЗ 50 м.

- Зони сільськогосподарського призначення - СВ

СВ-1	Зона земель сільськогосподарського призначення
СВ-1/1	Зона земель сільськогосподарського призначення в санітарно-захисній зоні промислових підприємств I-V класу шкідливості, сільськогосподарських, комунальних, складських територій
СВ-1/27	Зона сільськогосподарського призначення в охоронній зоні магістрального газопроводу
СВ-2-4	Зона сільськогосподарських підприємств, установ та організацій СЗЗ 100 м.
СВ-2-5	Зона сільськогосподарських підприємств, установ та організацій СЗЗ 50 м.

- Спеціальні зони - С

П-С-4	Зона озеленення спецпризначення проектна

- Інщі зони

ВП	Водна поверхня

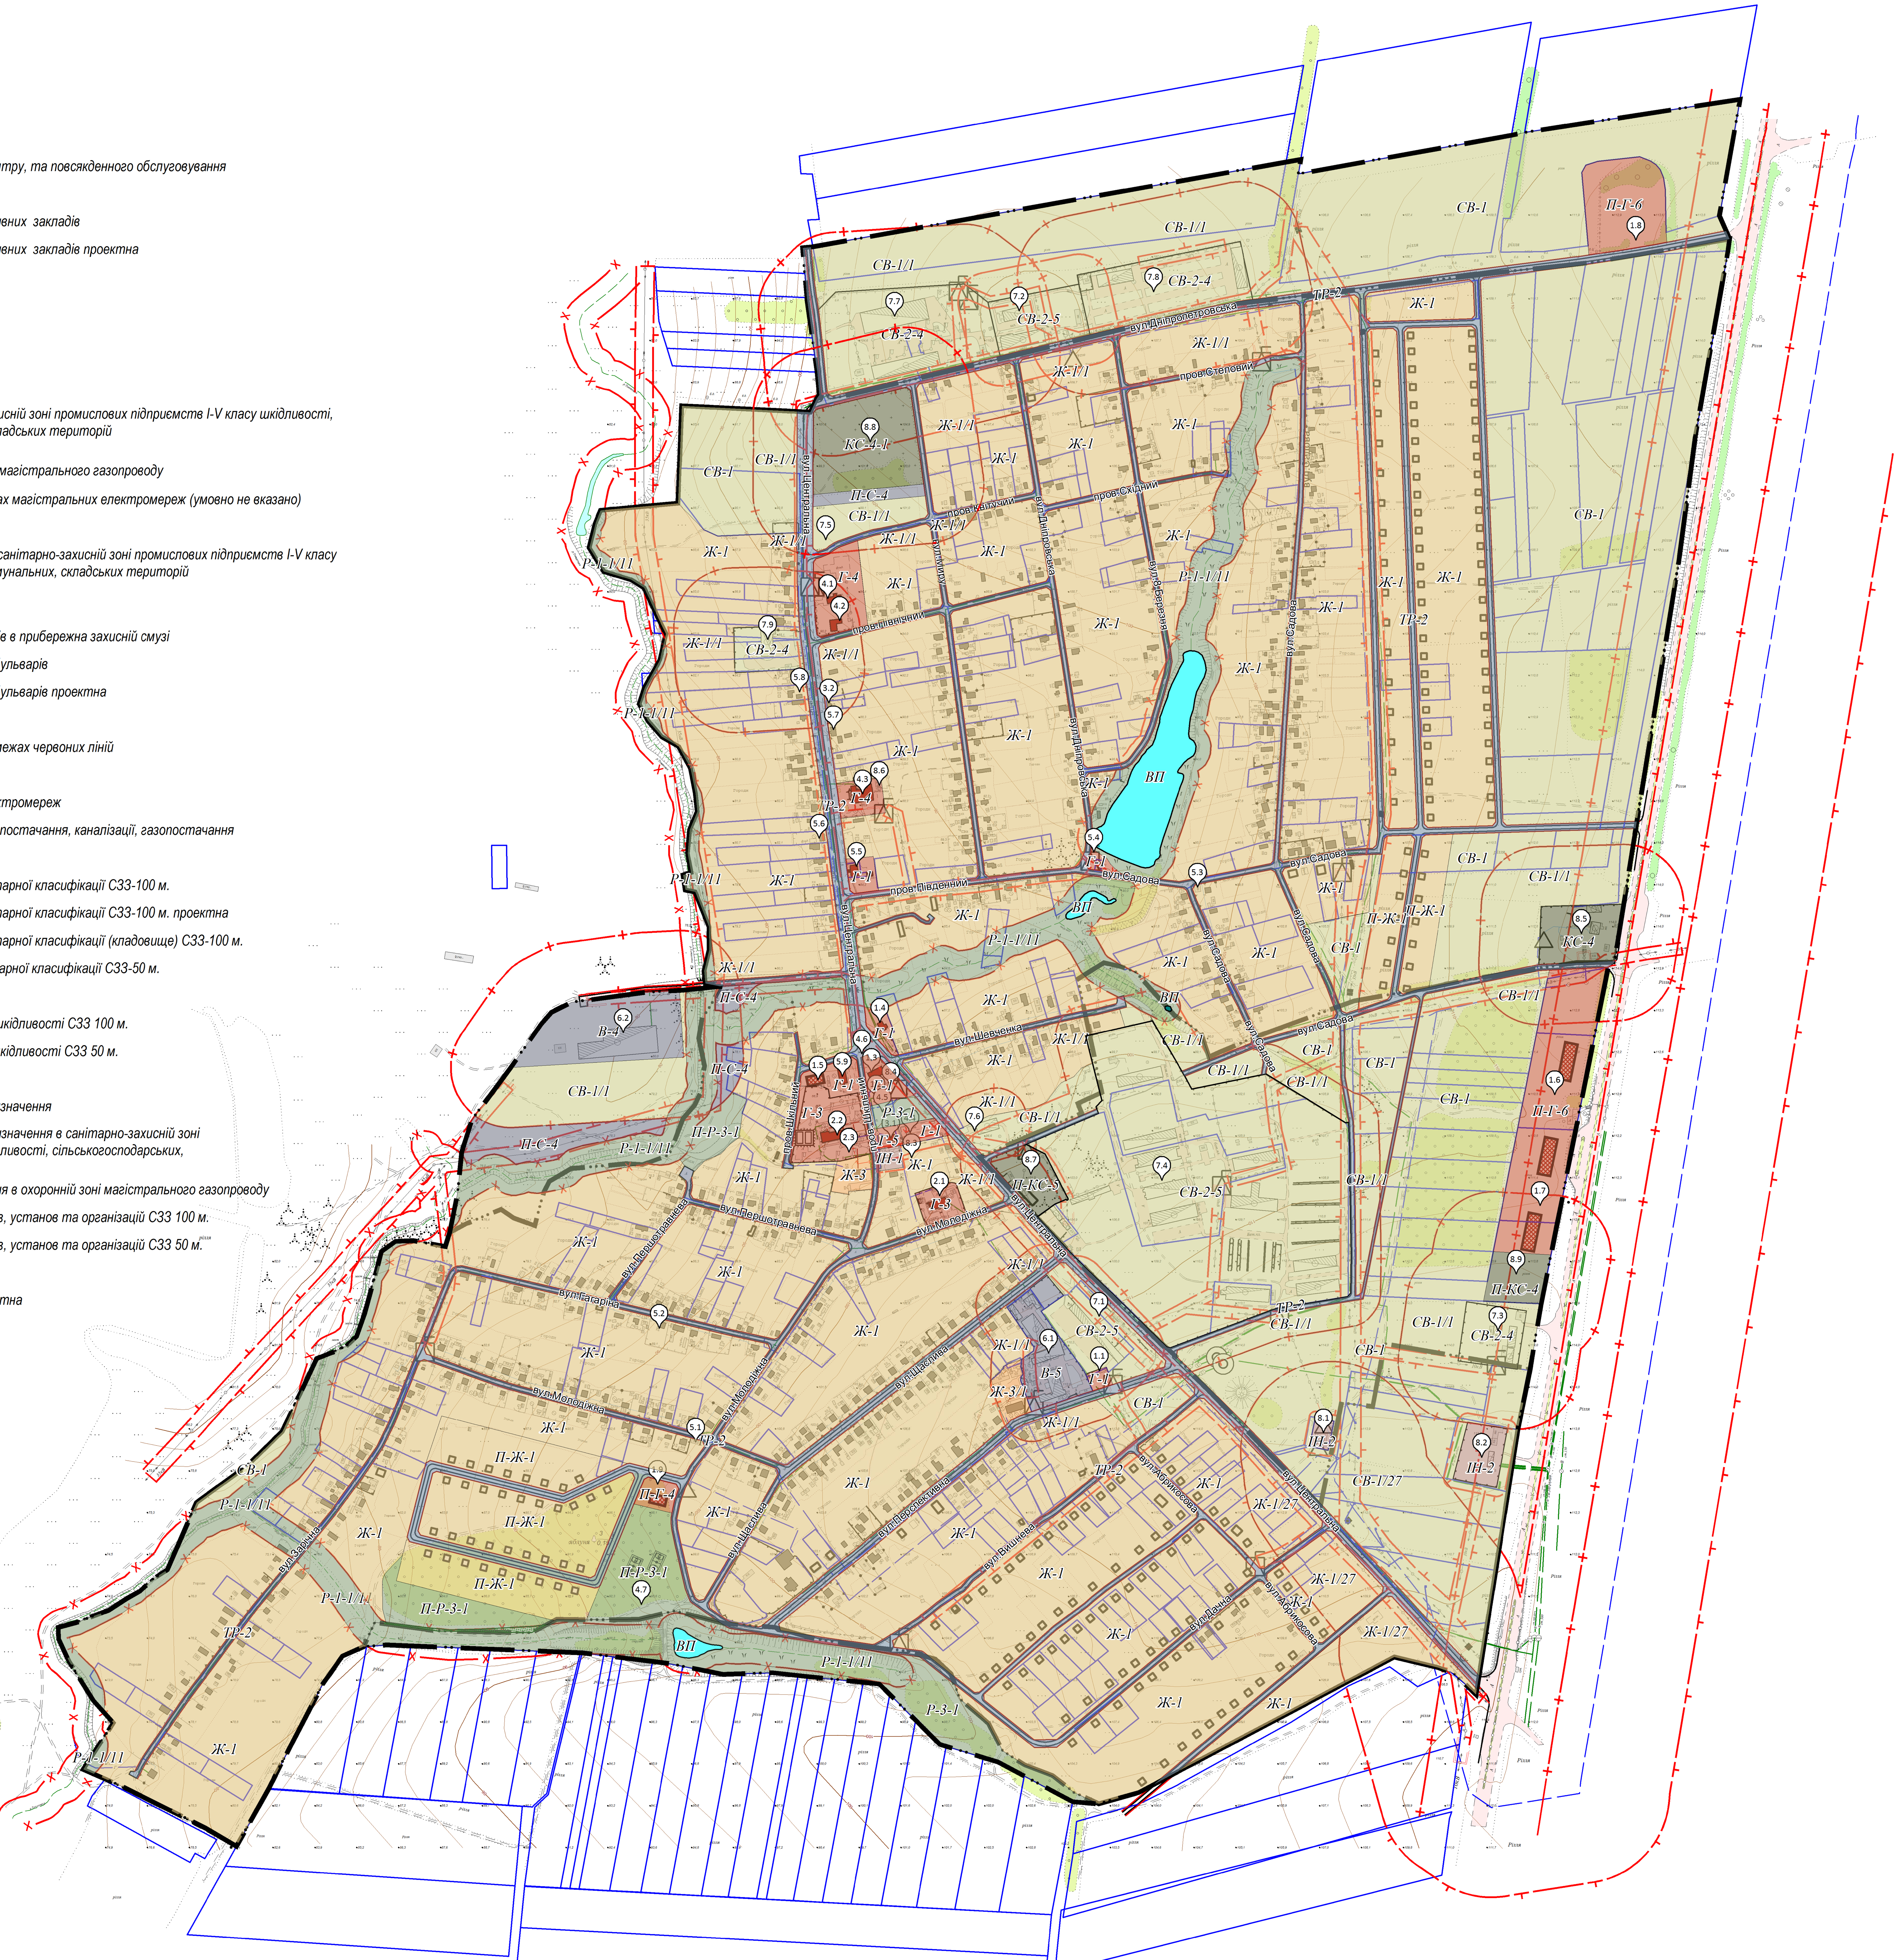

Експлікація будівель та споруд

№ п/п	Найменування	Примітка
1.	Адміністративні та громадські установи	
1.1	Адміністративна будівля Запорізького управління водного господарства	
1.2	Адміністративна будівля	
1.3	Адміністративна будівля	
1.4	Будівля побутового обслуговування населення	Проектн.
1.5	Відділення банку, пошти	Проектн.
1.6	Торгові, виставкові будівлі, логістичні центр	Проектн.
1.7	Готель, кафе	Проектн.
1.8	Ринок сільськогосподарської продукції	Проектн.
1.9	Спортивний зал	Проектн.
2.	Учбові заклади та дитячі установи	
2.1	Дитячий садок Лукашівський НВК	
2.2	Школа Лукашівський НВК,	
2.3	Спортивний майданчик	Проектн.
3.	Установи охорони здоров'я	
3.1	ФАП, приміщення для реабілітації	Реконстр.
3.2	Стоматологія	
4.	Установи культури та мистецтва, культові споруди	
4.1	Церква	
4.2	Будівля недільної школи храму	
4.3	Будинок культури з бібліотекою	
4.4	Братська могила радянських воїнів та пам'ятник воїнам - односельчанам	
4.5	Сільський парк	
4.6	Пам'ятник Шевченку Т.Г.	
4.7	Парк з спортивним та дитячим майданчиком	Проектн.
5.	Підприємства торгівлі, громадського харчування та побутового обслуговування	
5.1	Торгівельний павільйон	
5.2	Крамниця змішаної торгівлі	
5.3	Крамниця	
5.4	Торгівельний павільйон з літнім майданчиком	
5.5	Крамниця змішаної торгівлі	
5.6	Крамниця змішаної торгівлі з кафе	
5.7	Крамниця промислових товарів, кафе	
5.8	Крамниця ветеринарних та зоотоварів	
5.9	Об'єкт громадського харчування, туристичних послуг	
6.	Промислові підприємства	
6.1	Виробництво електротехнічної продукції ПП «Елтіз» СЗЗ 50 м	
6.2	Цегельний завод СЗЗ 100 м	
7.	Сільськогосподарське підприємство	
7.1	Комплекс по зберіганню зерна СЗЗ 50 м	
7.2	Комплекс по зберіганню зерна, овочів СЗЗ 50 м	
7.3	Підприємство по переробці зерна СЗЗ 100 м	
7.4	Склади сільськогосподарської продукції СЗЗ 50 м	
7.5	Територія вирощування декоративних рослин	Проектн.
7.6	Склади зберігання зерна СЗЗ 50	
7.7	Підприємство по переробці зерна СЗЗ 100 м	
7.8	Підприємство по технічному обслуговуванню та ремонту сільськогосподарської техніки СЗЗ 100 м	
7.9	Сільськогосподарське підприємство з складом, ваговою та обслуговуванню сільськогосподарської техніки СЗЗ 100 м	
8.	Комунальні заклади, склади, бази, підприємства транспорту та зв'язку	
8.1	ГРП ОЗ 10 м	
8.2	Насосна ЗСО 15 м	
8.3	ЗТП ОЗ 3 м	
8.4	Газова котельня ОЗ 10 м	
8.5	Господарські будівлі служби автомобільних доріг СЗЗ 100 м	
8.6	Вишка мобільного зв'язку	
8.7	Будівельній двір з виготовлення металевих конструкцій СЗЗ 50 м	Проектн.
8.8	Кладовище СЗЗ 100 м.	
8.9	АЗС, АГЗП СЗЗ 100 м.	Проектн.

Змін.	Кільк.	Арк.	№ док.	Підп.	Дата	14/07-2017		
						Генеральний план, План зонування території села Лукашеве Запорізького району Запорізької області.		
						Замовник: Широківська сільська рада	Стадія	Аркуш	Аркушів
ГАП	Прудка						ГП	7	7
Перевірив						План зонування території 1:5000	ФОП Прудка І.А.		
Розробив	Прудка								

Формат 1015 х 750

УКРАЇНА
ШИРОКІВСЬКА СІЛЬСЬКА РАДА
ЗАПОРІЗЬКОГО РАЙОНУ ЗАПОРІЗЬКОЇ ОБЛАСТІ
ОДИНАДЦЯТА ПОЗАЧЕРГОВА СЕСІЯ СЬОМОГО СКЛИКАННЯ

РІШЕННЯ

21 грудня 2017 року № 20

с. Широке

Про розроблення містобудівної документації«Генеральний план села Лукашеве Запорізького району Запорізької області. Оновлення з розширенням меж населеного пункту та План зонування села Лукашеве Запорізького району Запорізької області (у складі Генерального плану)».

Враховуючи необхідність раціонального використання земель, створення належних умов для життєзабезпечення села Лукашеве та керуючись п. 42 частини 1, ст.26 Закону України "Про місцеве самоврядування в Україні", ст.17 Закону України "Про регулювання містобудівної діяльності", Широківська сільська рада

ВИРІШИЛА:

1. Розробити містобудівну документацію «Генеральний план села Лукашеве Запорізького району Запорізької області. Оновлення з розширенням меж населеного пункту та План зонування села Лукашеве Запорізького району Запорізької області (у складі Генерального плану)» (далі - містобудівна документація).

2. Визначити замовником містобудівної документації Виконавчий комітет Широківської сільської ради Запорізького району Запорізької області.

3. При формуванні проекту бюджету на 2018 рік передбачити кошти на фінансування розроблення містобудівної та землевпорядної документації.

4. Виконавчому комітету Широківської сільської ради Запорізького району Запорізької області:

4.1.Визначити організацію-розробника містобудівної документації, яка має право на виконання даного виду робіт, строки розроблення та джерела його фінансування.

4.2. Повідомити через місцеві засоби масової інформації про початок розроблення містобудівної документації.

4.3. Укласти договір з організацією-розробником містобудівної документації.

4.4. Звернутись до Запорізької обласної державної адміністрації щодо визначення державних інтересів для їх врахування під час розроблення містобудівної документації.

4.5. Забезпечити збір вихідних даних для розроблення містобудівної документації.

4.6. Забезпечити, разом з організацію-розробником, попередній розгляд матеріалів містобудівної документації архітектурно-містобудівною радою при управлінні містобудування та архітектури Запорізької обласної державної адміністрації.

4.7. Забезпечити проведення громадських слухань, погодження містобудівної документації згідно чинного законодавства, із зарученням організації-розробника.

4.8. Погодити містобудівну документацію з органами місцевого самоврядування, що представляють інтереси суміжних територіальних громад (у разі необхідності).

5. Виготовлену та погоджену містобудівну документацію затвердити на сесії сільської ради.

6. Контроль за виконанням даного рішення покласти на постійну комісію з питань містобудування, будівництва, земельних відносин, екології, житлово-комунального господарства та комунальної власності.

Сільський голова Д.О. Коротенко

Додаток № 1 до договору № 207/2018 від 18.06.2018р.
(згідно ДБН Б. 1.1-15:2012 " Склад та зміст Генерального плану населеного пункту ")

Затверджено:

Голова Широківської сільської ради

_____ Коротенко Д.О.

«_____»_____2018р.

М.П.

Погоджено:

Начальник відділу містобудування, архітектури та житлово-комунального господарства Запорізької РДА

_____ Неумивака А.О.

«_____»_____2018р.

М.П.

Погоджено:

ФО-П Прудка І.А.

_____ Прудка І.А.

«_____»_____2018р.

М.П.

ЗАВДАННЯ

на розроблення містобудівної документації «Генеральний план села Лукашеве Запорізького району Запорізької області. Оновлення з розширенням меж населеного пункту та план зонування села Лукашеве Запорізького району Запорізької області (у складі генерального плану)».

Згідно з ДБН Б.1.1-15:2012 « Склад та зміст генерального плану населеного пункту» та ДСТУ-Н Б Б.1.1-12:2011 « Настанова про склад та зміст плану зонування території (зонінг)».

1. Підстави для проектування	Рішення Широківської сільської ради Запорізького району Запорізької області: «Про Розроблення генерального плану села Лукашеве Запорізького району Запорізької області. Оновлення з розширенням меж населеного пункту та план зонування села Лукашеве Запорізького району Запорізької області (у складі генерального плану)» від 21.12.2017 №20
2. Замовник розроблення генерального плану	Широківська сільська рада Запорізького району Запорізької області.
3. Розробник генерального плану	ФО-П Прудка І. А. Головний архітектор проекту Прудка І.А.

	Кваліфікаційний сертифікат Серія АА № 003280 (розроблення містобудівної документації).
4. Строк розроблення генерального плану	Визначається договором на виконання робіт
5. Мета розроблення генерального плану	Генеральний план необхідно розробити з врахуванням: 1. Розширенням меж населеного пункту та його прилеглої зони, уточнення параметрів забудови; 2. Зміни показників розрахункової чисельності населення та нормативну забезпеченість села об'єктами обслуговування; 3. Необхідністю розроблення нових розділів генплану відповідно до діючого законодавства. 4. З метою визначення умов та обмежень використання території для містобудівних потреб.
6.Строк розрахункового етапу генерального плану та першої черги реалізації	Розрахунковий етап - 2038р.(20років), Перша черга реалізації – 2023р. (5років).
7. Основні показники населеного пункту.	Розробити генерального плану для розміщення населення - проектна площа 719,2 га, - на розрахунковий період – 2,450 тис. осіб, Показник уточняється при розробці генерального плану
8. Вихідні дані для розроблення генерального плану (надаються Замовником)	1. Тахеометрична зйомка виконана у державній геодезичній системі координат УСК-2000. 2. Матеріали інженерних, інженерно-геологічних та геодезичних вишукувань. 3. Матеріали санітарно-гігієнічного стану території села, обмеження щодо використання різних територій, інших природно-географічних та геологічних факторів. 4. Місцеві програми соціально-економічного розвитку, демографічні дані за останні 10 років, наявність об'єктів соціального, побутового та комунального обслуговування. 5. Дані щодо існуючого використання території (на основі державного земельного кадастру). 6. Історико-культурні об'єкти, охоронні зони та інші умови відносно збереження історико-культурної спадщини. 7. Перелік раніше розробленої містобудівної, землевпорядної документації, проектно-дослідницьких та вишукувальних робіт, які необхідно врахувати при проектуванні.
9. Графічні матеріали з зазначенням масштабу	1. Схема розташування територій, щодо яких вносяться зміни, у функціонально-планувальній

	2. План існуючого використання території. Схема існуючих планувальних обмежень М 1:5000 3. Генеральний план (основне креслення). Схема проектних планувальних обмежень М 1:5000 4. Схема вулично – дорожньої мережі, міського (сільського) та зовнішнього транспорту М 1:5000 5. Схема інженерного обладнання території М 1:5000 6. Схема інженерної підготовки та захисту території М 1:5000 7. План зонування території М1:5000
10. Перелік додаткових розділів та графічних матеріалів, або додаткові вимоги до змісту окремих розділів чи графічних матеріалів.	1. Виготовити план зонування території у складі генерального плану населеного пункту 2. Окремим томом виконати розділ «Інженерно-технічних заходів цивільного захисту (цивільної оборони)» на особливий період виконати, згідно окремого завдання на проектування, з врахуванням рішень затверджених відповідних розділів проектів (схем) районного планування.
11. Особливі вимоги до забудови, інженерного обладнання, організації транспорту, пішоходів	1. Висотність забудови не повинна перевищувати 1 - 4 поверхи. 2. Переважним видом забудови прийняти садибну, з ділянками 0,25 га, в тому числі. 3. Надати пропозиції щодо розвитку внутрішньої мережі вулиць. 4. Надати пропозиції щодо охоронних та захисних зон з врахуванням містобудівних чинників. 5. Надати пропозиції щодо централізованого водопостачання для всієї забудови населеного пункту. Розмістити вузол водопідготовлення. 6. Надати пропозиції щодо централізованої каналізації для всієї забудови населеного пункту. 7. Передбачити резервування території під розміщення об'єктів культурно-побутового обслуговування населення, розміщення об'єктів торговельної інфраструктури. 8. Приділити особливу увагу межі зон охорони пам'яток культурної спадщини в обов'язковому порядку нанести на основний кресленик генерального плану села, земельні ділянки що містять пам'ятку місцевого та національного значення. 9. Передбачити зелені і паркові зони; 10. Передбачити спортивно-ігрові майданчики;
12. Вимоги щодо врахування державних інтересів	Зазначити згідно умов від центрального органу виконавчої влади, що забезпечує формування

	державної політики у сфері містобудування та архітектури.
13. Вимоги щодо розрахунків на першу чергу реалізації	На першу чергу реалізації генерального плану передбачити включення до території села Лукашеве прилеглих зон фермерських господарств, що встановлені органами державного земельного кадастру та надати пропозиції щодо комплексного благоустрою цих території.
14. Додаткові вимоги.	На підставі затвердженого Генерального плану населеного пункту та плану Зонування території подальшими етапами розробки містобудівної документації на місцевому рівні є «Детальні плани територій».
15. Кількість додаткових екземплярів графічних та текстових матеріалів.	Матеріали проектної документації виконати у 3-х примірниках, з яких – один примірник матеріалів проектної документації – для передачі відділу містобудування, архітектури та житлово-комунального господарства Запорізької райдержадміністрації, та на магнітних носіях. Для текстових матеріалів -.pdf, графічних -.tiff,
16.Основні вимоги до програмного забезпечення, в тому числі геоінформаційних систем та технологій	Для Замовника: для текстових матеріалів -*Adobe (Acrobat) Reader* . -для графічних - *Microsoft Windows Photo Viewer, , Adobe Illustrator, other image viewer.* Для розробника: OpenOffice,AutoCad, *ArcGIS, або Digitals*

Головний архітектор проекту Прудка І.А.

УКРАЇНА
ЗАПОРІЗЬКА ОБЛАСНА ДЕРЖАВНА АДМІНІСТРАЦІЯ
пр. Соборний, 164, м. Запоріжжя, 69107, тел/факс: (061) 224-63-81
E-mail: adm@zoda.gov.ua; www.zoda.gov.ua Код ЄДРПОУ 00022504

Шанов в розгляд 05.02.2018

06.02.2018 № 00158/08-27 На № 01-48/16 від 03.07.2018

Широківському сільському голові

Коротенку Д.О.

вул. Центральна, 1, с. Широке,
Запорізький район, 70413

Про визначення та врахування державних та регіональних інтересів під час розроблення генерального плану села Лукашеве

Шановний Денисе Олександровичу!

Обласна державна адміністрація розглянула лист Широківської сільської ради Запорізького району Запорізької області від 03.01.2018 № 01-48/16 щодо визначення державних та регіональних інтересів при розробленні містобудівної документації «Генеральний план села Лукашеве Запорізького району Запорізької області. Оновлення з розширенням меж населеного пункту та План зонування села Лукашеве Запорізького району Запорізької області (у складі Генерального плану)» та повідомляє про таке.

Відповідно до планувальних рішень Схеми планування території Запорізької області, яка затверджена рішенням Запорізької обласної ради від 29.12.2011 № 4, територія села Лукашеве за функціональним зонуванням відноситься до території з пріоритетним розвитком логістичних центрів складування, доробки та сортування вантажів та до Північної (Запорізької) підзони урбанізації - з критичним рівнем виробничо-містобудівного освоєння території.

На території рекомендується жорстке регулювання містобудівного розвитку з першочерговою реструктуризацією економічної бази та екологічною реабілітацією території.

Відповідно до аналізу рівня соціально-економічного розвитку окремих таксонів Запорізької області Запорізький район відноситься до 3 типу таксонів із середнім показником потенціалу та середнім рівнем соціально-економічного та містобудівного розвитку. Перспективи розвитку району цього типу пов'язано із використанням його переваг транспортно-географічного положення.

В районі планується розвиток багатоступеневої системи громадського обслуговування населення з розміщенням підприємств повсякденного та періодичного обслуговування.

Вх. 02-01-22/581
«07» 02 2018 р.

КП "ЗМД "ДМ". Зам. № 776 – 1000

Планувальними рішеннями Схеми планування території Запорізької області на території села Лукашеве передбачено:

зона впливу автомобільного транспортного коридору Європа-Азія;

розчистка р. Томаківка.

Необхідно виконати роботи з розробки розділу «Інженерно-технічні заходи цивільного захисту» (далі – ІТЗ ЦЗ), який є складовою частиною містобудівної документації (схеми планування території або генерального плану). Головним завданням розділу ІТЗ ЦЗ при плануванні території є створення містобудівних умов, забезпечення захисту населення і територій від надзвичайних ситуацій техногенного та природного характеру, їх наслідків з урахуванням особливостей соціально-економічного розвитку та природно-кліматичних умов. Розділ розробити згідно ДБН Б.1.1-5:2007 Склад, зміст, порядок розроблення, погодження та затвердження розділу інженерно-технічних заходів цивільного захисту (цивільної оборони) у містобудівній документації (перша та друга частини), де визначити конкретні рішення щодо забезпечення захисту населення і територій від надзвичайних ситуацій техногенного і природного характеру та їх наслідків.

Врахувати реконструкцію водопровідних мереж села Лукашеве.

При розроблені містобудівної документації необхідно врахувати розташування комплексної пам'ятки природи місцевого значення – «Балка Лукашева», що знаходиться на північний захід від с. Лукашеве, обмеження господарської діяльності в межах прибережної захисної смуги в складі водоохоронної зони р. Томаківка та ст. 59 Закону України «Про охорону навколишнього природного середовища», п. «г» ст. 32 Закону України «Про відходи», ст. 87, 88, 89 Водного кодексу України, ст. 60, 61 Земельного кодексу України.

На території та поблизу с. Лукашеве Запорізького району розташовані наступні пам’ятки культурної спадщини місцевого значення, які перебувають на державному обліку, та взяті на облік відповідно до Закону Української РСР «Про охорону і використання пам’яток історії та культури»:

Пам’ятки археології:

1. Курган «Могила Весела», охоронний № 1911, с. Лукашеве, за 1,0 км на північний захід від північної околиці села. Взятий на облік рішенням виконкому Запорізької обласної ради народних депутатів від 23.10.1984 № 354.

2. Курган, охоронний № 4023, с. Лукашеве, за 1,1 км на південний захід від південно-західної околиці села. Взятий на облік розпорядженням голови Запорізької облдержадміністрації від 11.03.1996 № 161.

3. Курганний могильник з 3 курганів, охоронний № 4028, с. Лукашеве, за 1,5 км на схід від північно-східної околиці села. Взятий на облік розпорядженням голови Запорізької облдержадміністрації від 11.03.1996 № 161.

4. Курган, охоронний № 1909, с. Лукашеве, за 1,7 км на північний схід від північно-східної околиці села. Взятий на облік рішенням виконкому Запорізької обласної ради народних депутатів від 23.10.1984 № 354.

5. Курган, охоронний № 4025, с. Лукашеве, за 2,0 км на південний схід від південно-східної околиці села. Взятий на облік розпорядженням голови Запорізької облдержадміністрації від 11.03.1996 № 161.

6. Курган, охоронний № 4026, с. Лукашеве, за 2,0 км на схід від південно-східної околиці села. Взятий на облік розпорядженням голови Запорізької облдержадміністрації від 11.03.1996 № 161.

7. Курганний могильник з 2 курганів, охоронний № 4024, с. Лукашеве, за 2,3 км на північний схід від північно-східної околиці села. Взятий на облік розпорядженням голови Запорізької облдержадміністрації від 11.03.1996 № 161.

8. Курган, охоронний № 1907, с. Лукашеве, на південно-східній околиці села. Взятий на облік рішенням виконкому Запорізької обласної ради народних депутатів від 23.10.1984 № 354.

9. Курганний могильник з 2 курганів, охоронний № 1905, с. Лукашеве, за 2,9 км на північний схід від північно-східної околиці села. Взятий на облік рішенням виконкому Запорізької обласної ради народних депутатів від 23.10.1984 № 354.

10. Курган, охоронний № 1906, с. Лукашеве, за 3,0 км на північний захід від західної околиці села. Взятий на облік рішенням виконкому Запорізької обласної ради народних депутатів від 23.10.1984 № 354.

11. Курганний могильник з 5 курганів, охоронний № 1910, с. Лукашеве, за 3,0 км на схід від східної околиці села. Взятий на облік рішенням виконкому Запорізької обласної ради народних депутатів від 23.10.1984 № 354.

12. Курганний могильник з 3 курганів, охоронний № 4027, с. Лукашеве, за 1,5 км на захід від південно-західної околиці села. Взятий на облік розпорядженням голови Запорізької облдержадміністрації від 11.03.1996 № 161.

Рішенням виконкому Запорізької районної ради народних депутатів від 13.06.1985 № 225 для пам'яток археології затверджено охорону зону в радіусі 5 м від підніжжя курганів.

Для пам'яток археології під охоронними №№ 4023, 4024, 4025, 4026, 4027, 4028 затверджено охоронну зону розміром 5 м від підніжжя курганів.

Пам'ятка історії:

Братська могила радянських воїнів та пам'ятник воїнам-односельцям, охоронний № 410, с. Лукашеве, у сквері в центрі села, яка взята на облік рішенням виконкому Запорізької обласної ради депутатів трудящих від 10.02.1971 № 55.

Пам'ятки монументального мистецтва:

Пам'ятник Шевченку Т.Г. - українському поету, охоронний № 1498, с. Лукашеве, в центрі села. Взятий на облік рішенням виконкому Запорізької обласної ради народних депутатів від 22.12.1982 № 580.

Під час виконання робіт з розробки містобудівної документації «Генеральний план села Лукашеве Запорізького району Запорізької області. Оновлення з розширенням меж населеного пункту та План зонування села Лукашеве Запорізького району Запорізької області (у складі Генерального плану)» необхідним є врахування та дотримання вимог Законів України «Про охорону культурної спадщини» і «Про охорону археологічної спадщини».

Необхідно врахувати та відобразити інформацію про:

об'єкти державного земельного кадастру які входять до Генерального плану;

структуру і характеристику земель та віднесення їх до особливо цінних земель;

врахування вимог статті 23 Земельного кодексу України;

суб'єктів підприємницької діяльності у галузі топографо-геодезичної і картографічної діяльності, задіяних для оновлення (створення) картографічної основи;

систему географічних координат, в якій виконано оновлення картографічної основи, а також пункти Державної геодезичної мережі, використані при топографо-геодезичних і картографічних роботах;

передачу до Державного картографо-геодезичного фонду України копій геодезичних, топографічних, картографічних, гідрографічних, аерозйомочних матеріалів, що передбачено статтею 19 Закону України «Про топографо-геодезичну і картографічну діяльність».

Примірники креслень графічних матеріалів містобудівної документації на оптичних дисках повинні бути виконані у форматі геоінформаційних систем, що підтримують об'єктне представлення геопросторових даних.

Профільні геопросторові дані не пізніше 30 робочих днів після затвердження містобудівної документації повинні бути внесені до містобудівного кадастру Запорізького району. У разі не створення містобудівного кадастру Запорізького району, на час затвердження містобудівної документації місцевого рівня, зазначені матеріали повинні бути передані до Управління містобудування та архітектури облдержадміністрації та до відділу містобудування, архітектури та житлово-комунального господарства Запорізької райдержадміністрації.

Обласна державна адміністрація просить Вас врахувати державні та регіональні інтереси під час виконання робіт з розробки містобудівної документації «Генеральний план села Лукашеве Запорізького району Запорізької області. Оновлення з розширенням меж населеного пункту та План зонування села Лукашеве Запорізького району Запорізької області (у складі Генерального плану)».

З повагою

керівник апарату
обласної державної адміністрації З.М. Бойко

Билим
Осадча 239 01 43

МІНІСТЕРСТВО РЕГІОНАЛЬНОГО РОЗВИТКУ, БУДІВНИЦТВА ТА ЖИТЛОВО-КОМУНАЛЬНОГО ГОСПОДАРСТВА УКРАЇНИ

АТЕСТАЦІЙНА АРХІТЕКТУРНО-БУДІВЕЛЬНА КОМІСІЯ

Серія АА №003280

КВАЛІФІКАЦІЙНИЙ СЕРТИФІКАТ

відповідального виконавця окремих видів робіт (послуг), пов'язаних із створенням об'єкта архітектури

архітектор
(найменування професії)

Виданий про те, що **Прудка Ірина Анатоліївна**
(прізвище, ім'я, по батькові)

пройшов(ла) професійну атестацію, що підтверджує його (її) відповідність кваліфікаційним вимогам у сфері діяльності, пов'язаної із створенням об'єктів архітектури, професійну спеціалізацію, необхідний рівень кваліфікації і знань.

Категорія: **архітектор**.

Кваліфікаційний сертифікат видано згідно з рішенням Атестаційної архітектурно-будівельної комісії (далі - Комісія) від _____ № _____
(рішенням **відповідної** секції Комісії
від **13.07.2016** № **8-16**, затвердженим президією
Комісії **14.07.2016 № 54-А**).

Зареєстрований у реєстрі атестованих осіб **14 липня** 20**16** року
за № **3280**.

Роботи (послуги), пов'язані із створенням об'єктів архітектури, спроможність виконання яких визначено кваліфікаційним сертифікатом:

Розроблення містобудівної документації

Дата видачі **15 липня** 20**16** року

Голова Атестаційної архітектурно-будівельної комісії _____ **Білоус Сергій Ярославович**
(підпис) *(прізвище, ім'я, по батькові)*

М.П.

Держзнак. КОФ. Зам. 3564 2012 р. IV кв.